




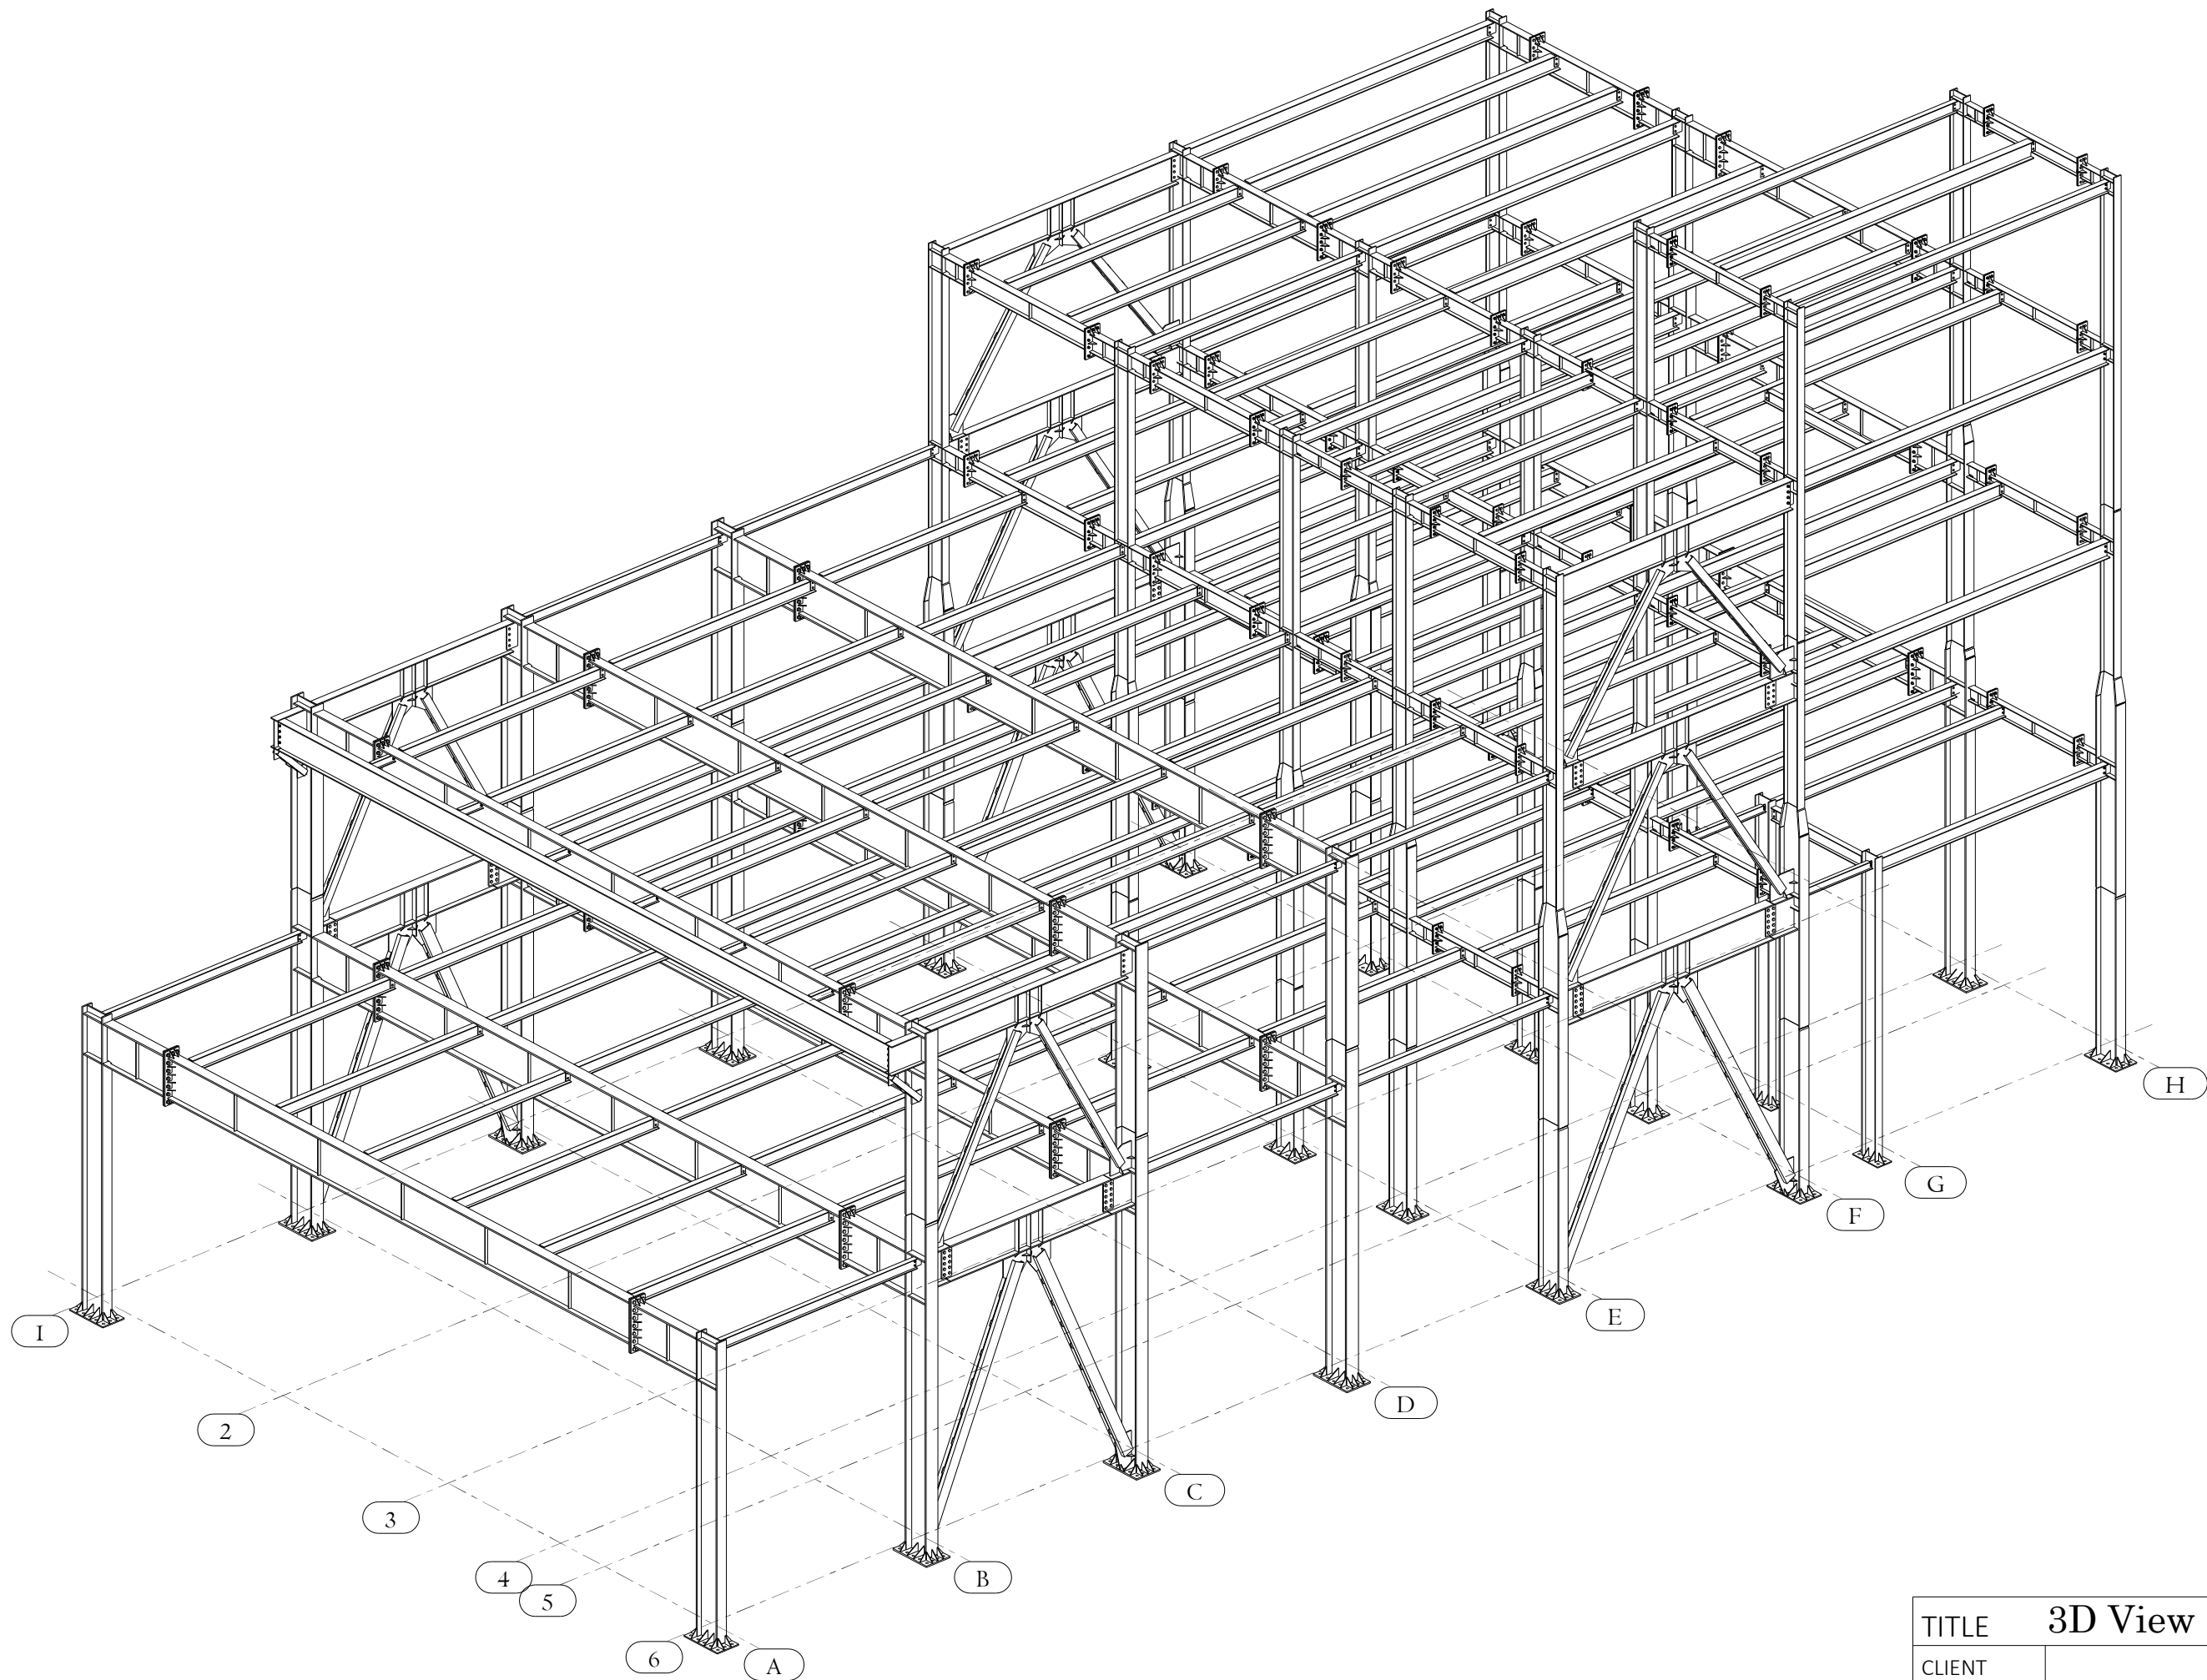


TITLE		3D View		
CLIENT				
CONTRACTOR		ISSUED		
MODELLED BY	EN ALMASI	SCALE 1:100		A3
DRAWING No	[1]	REVISION No. 0		

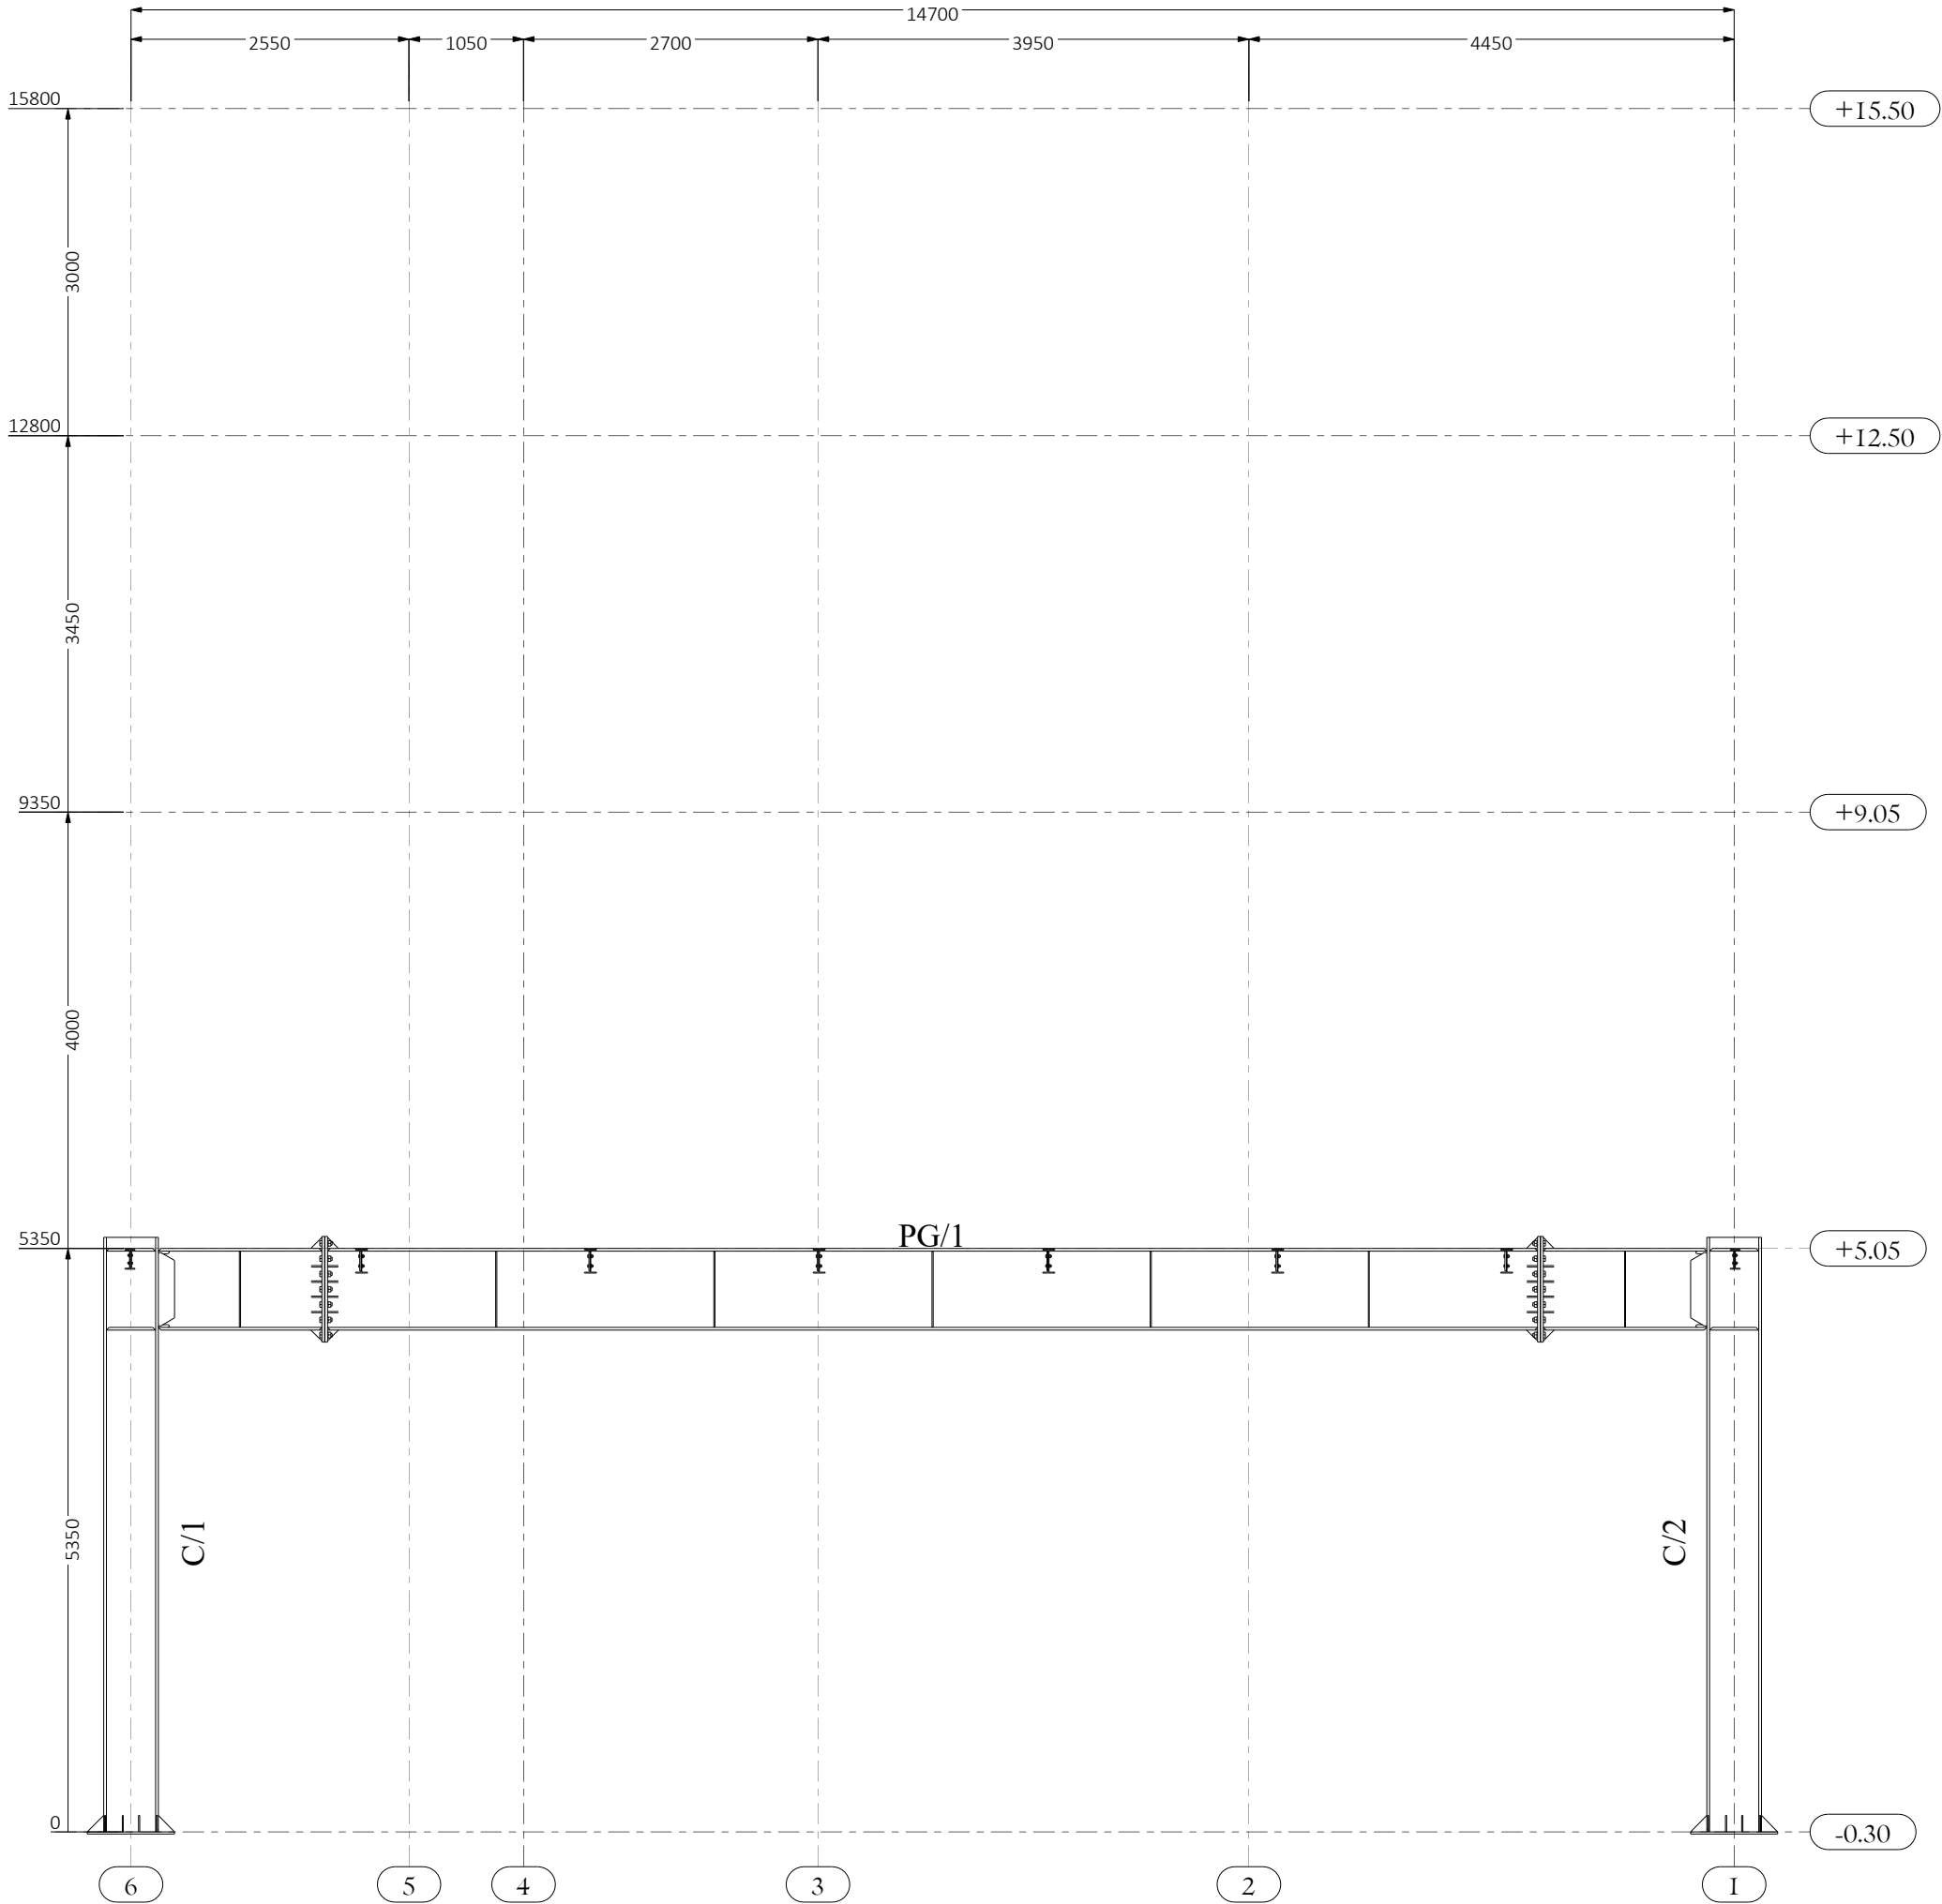


TITLE		Axe A		
CLIENT				
CONTRACTOR		ISSUED		
MODELLED BY	EN ALMASII	SCALE	1:65	
DRAWING No	[2]	REVISION No.	0	A3

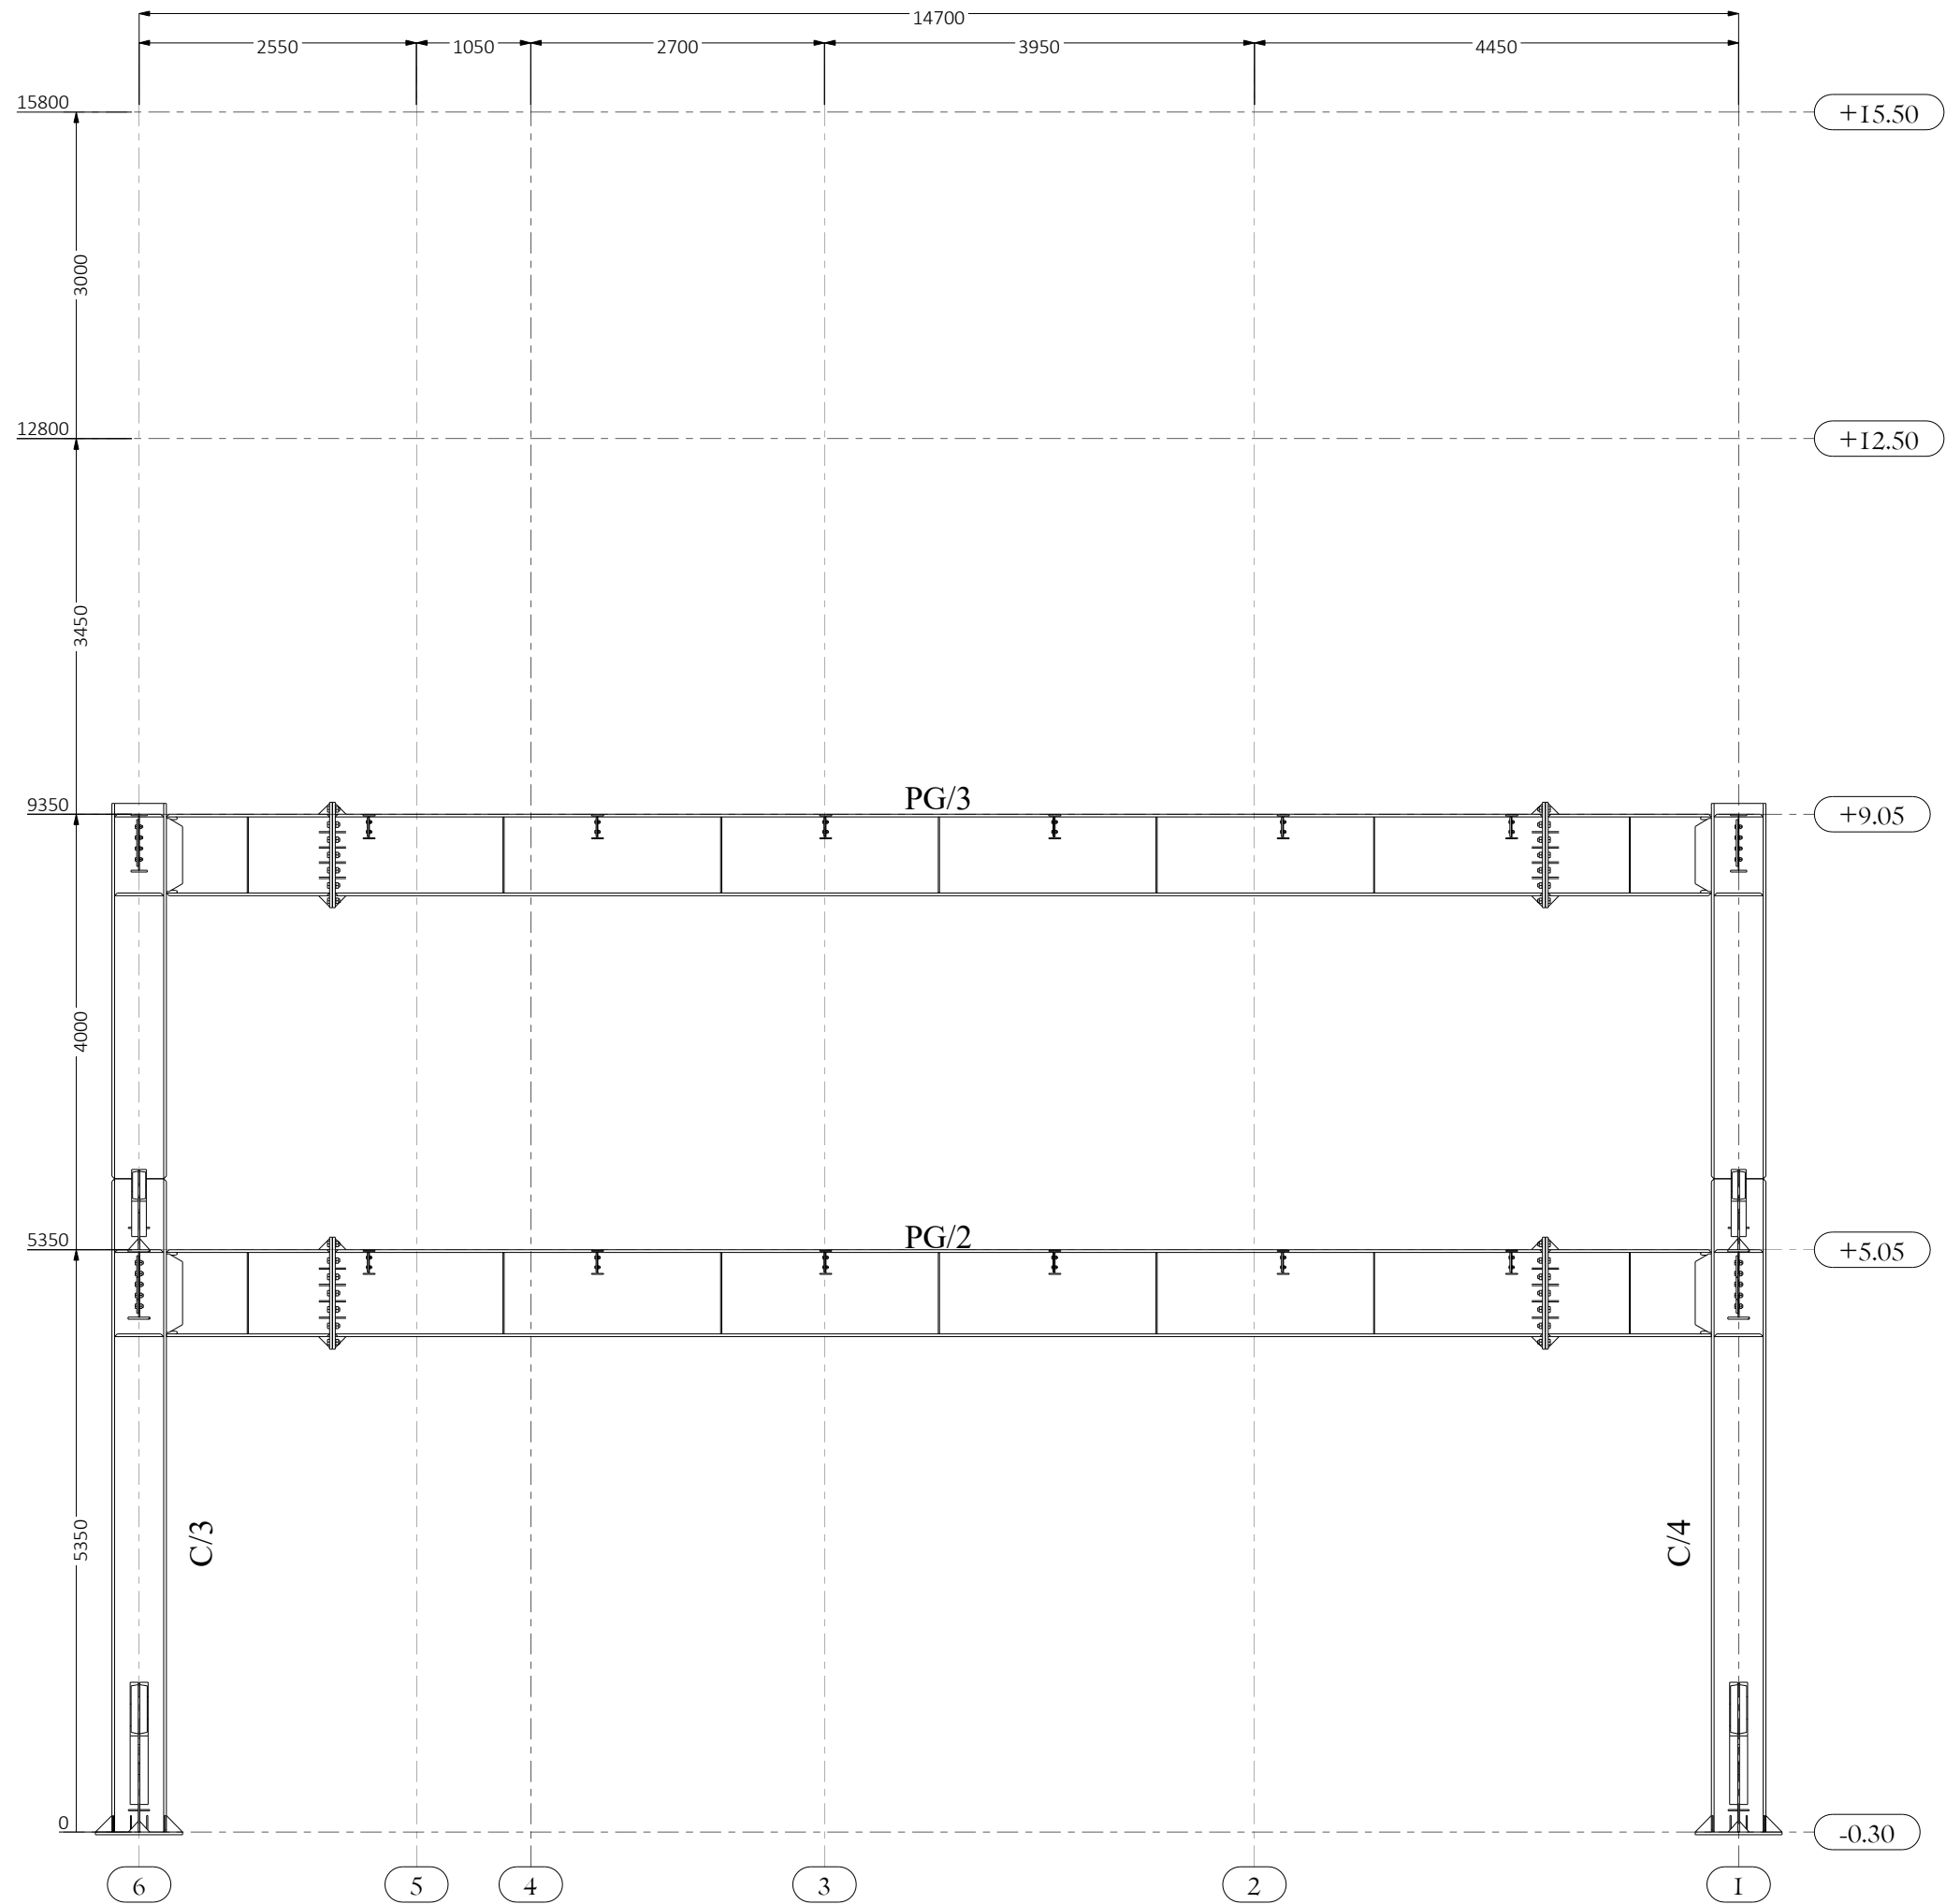


TITLE		Axe B		
CLIENT				
CONTRACTOR			ISSUED	
MODELLED BY		EN ALMASI	SCALE 1:65	
DRAWING No		[3]	REVISION No. 0	A3

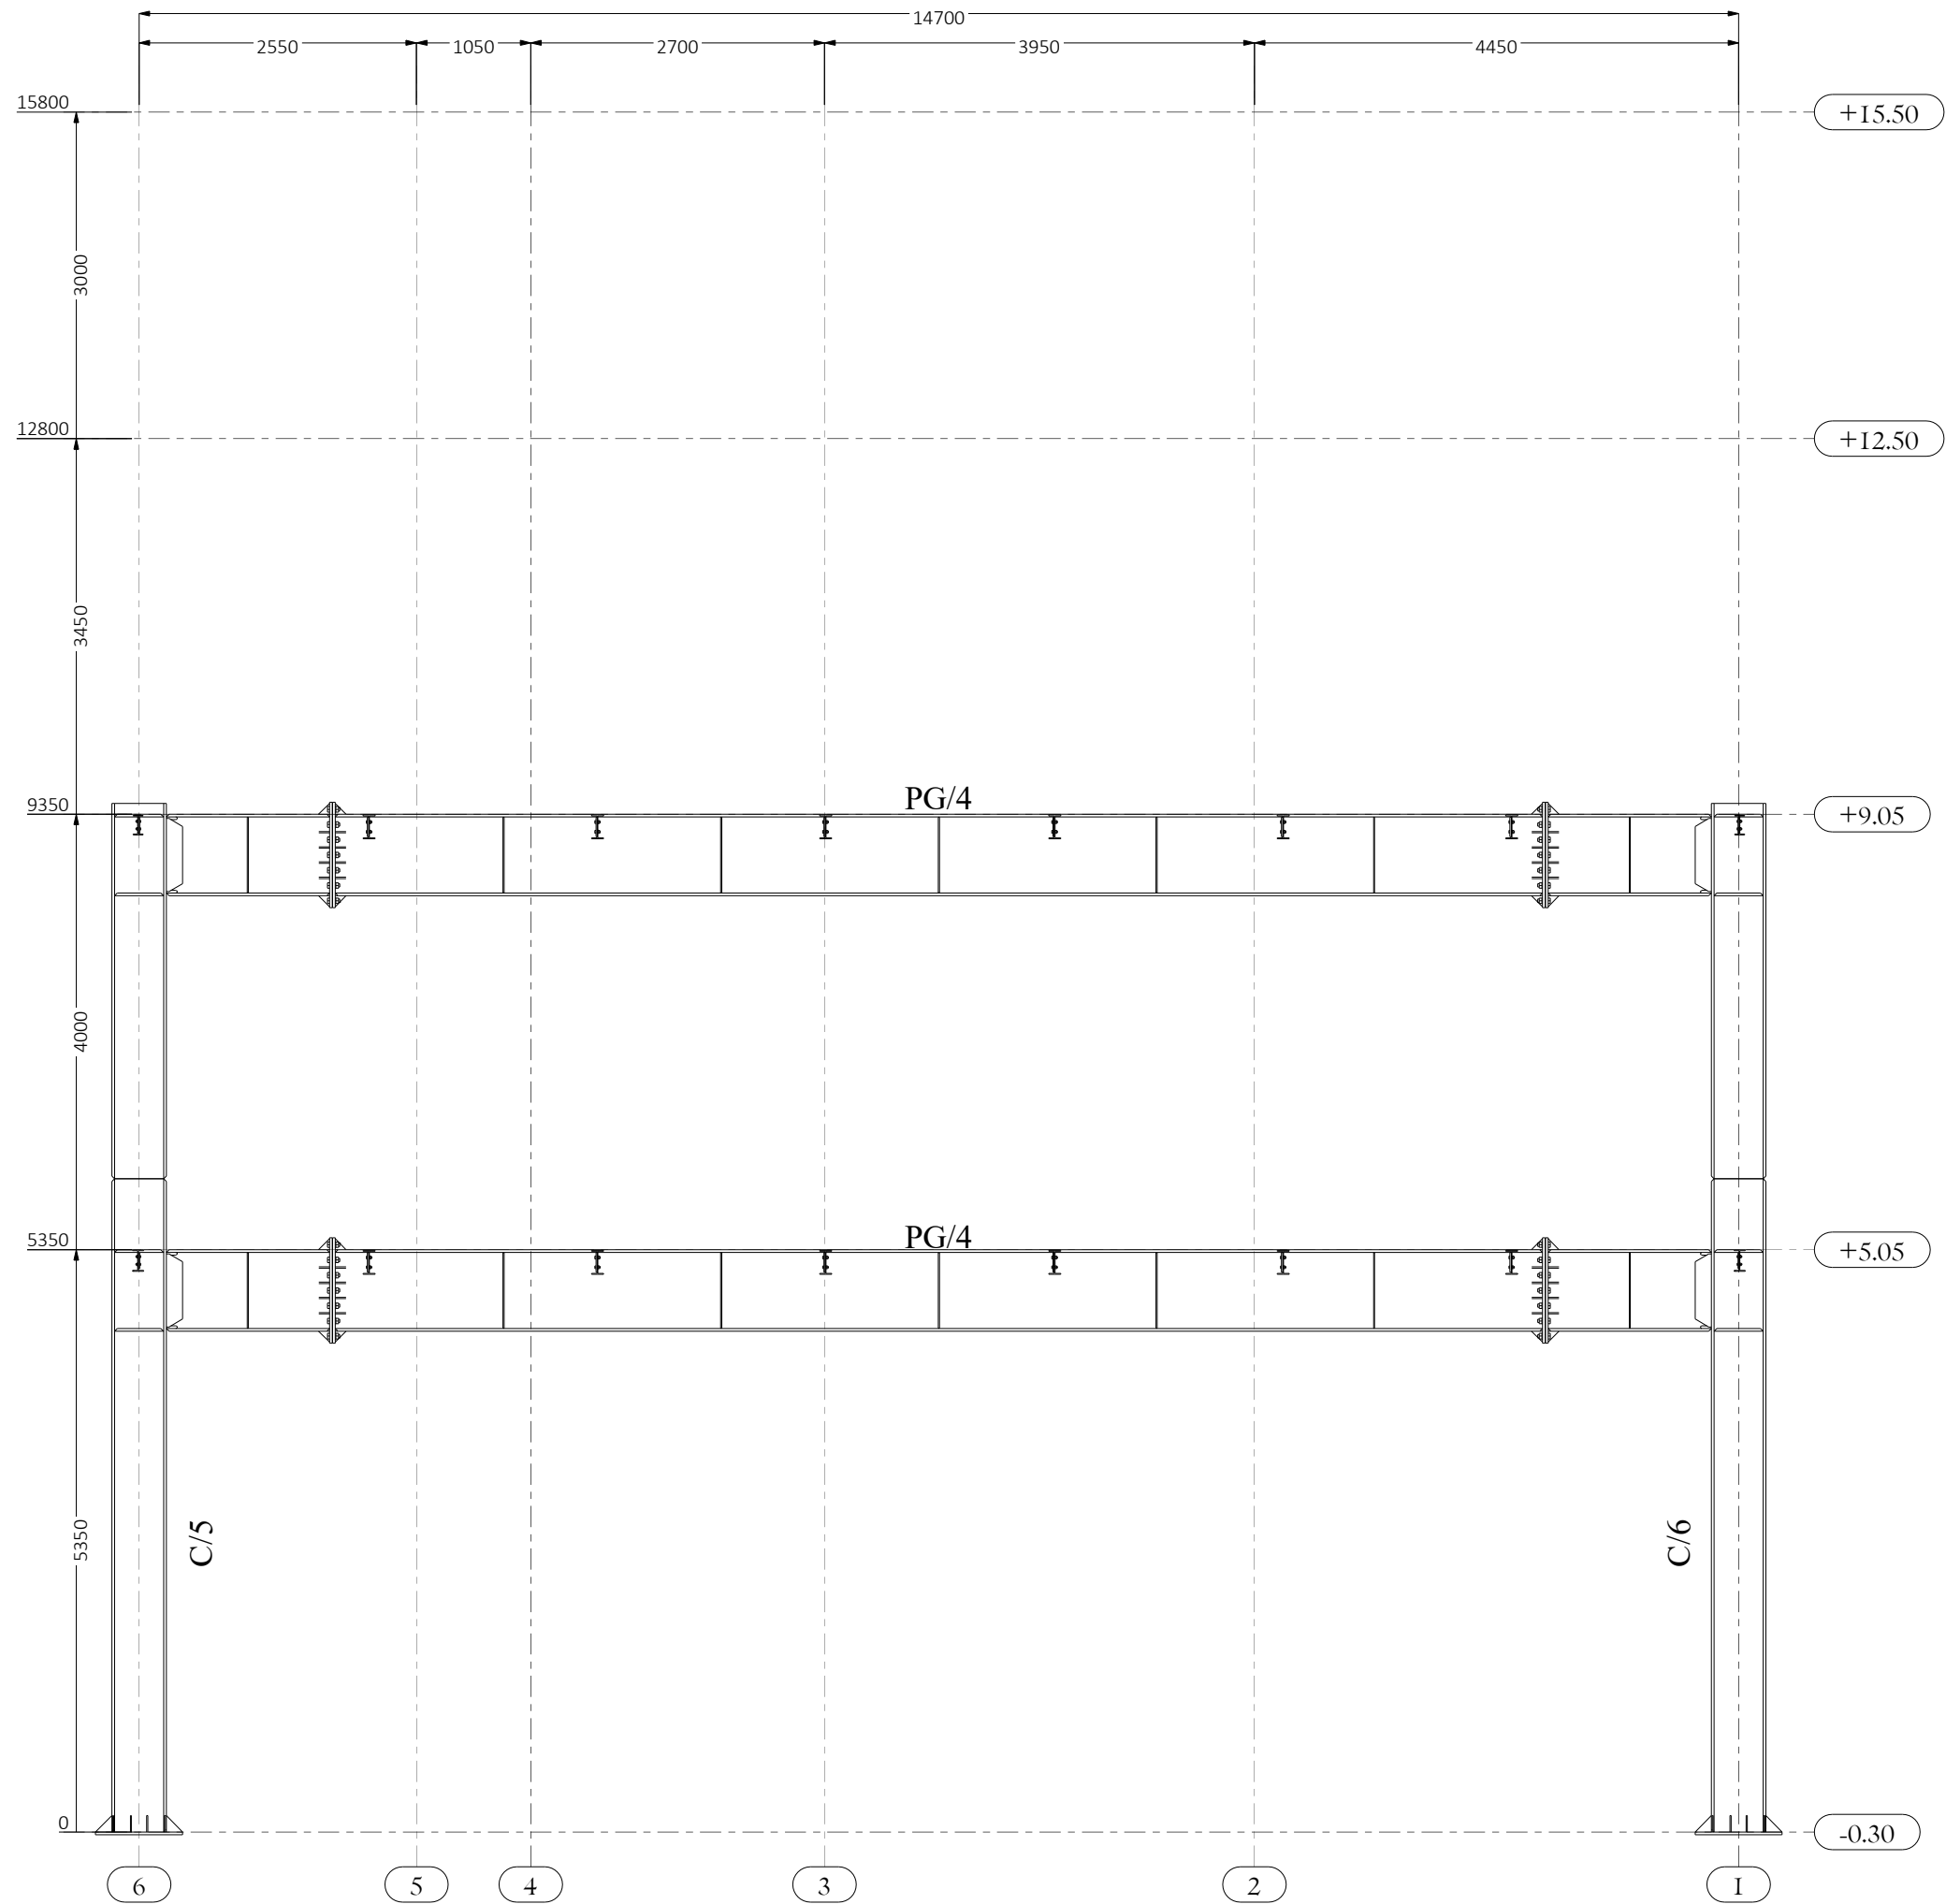


TITLE		Axe C		
CLIENT				
CONTRACTOR			ISSUED	
MODELLED BY		EN ALMASI	SCALE 1:65	
DRAWING No		[4]	REVISION No. 0	A3

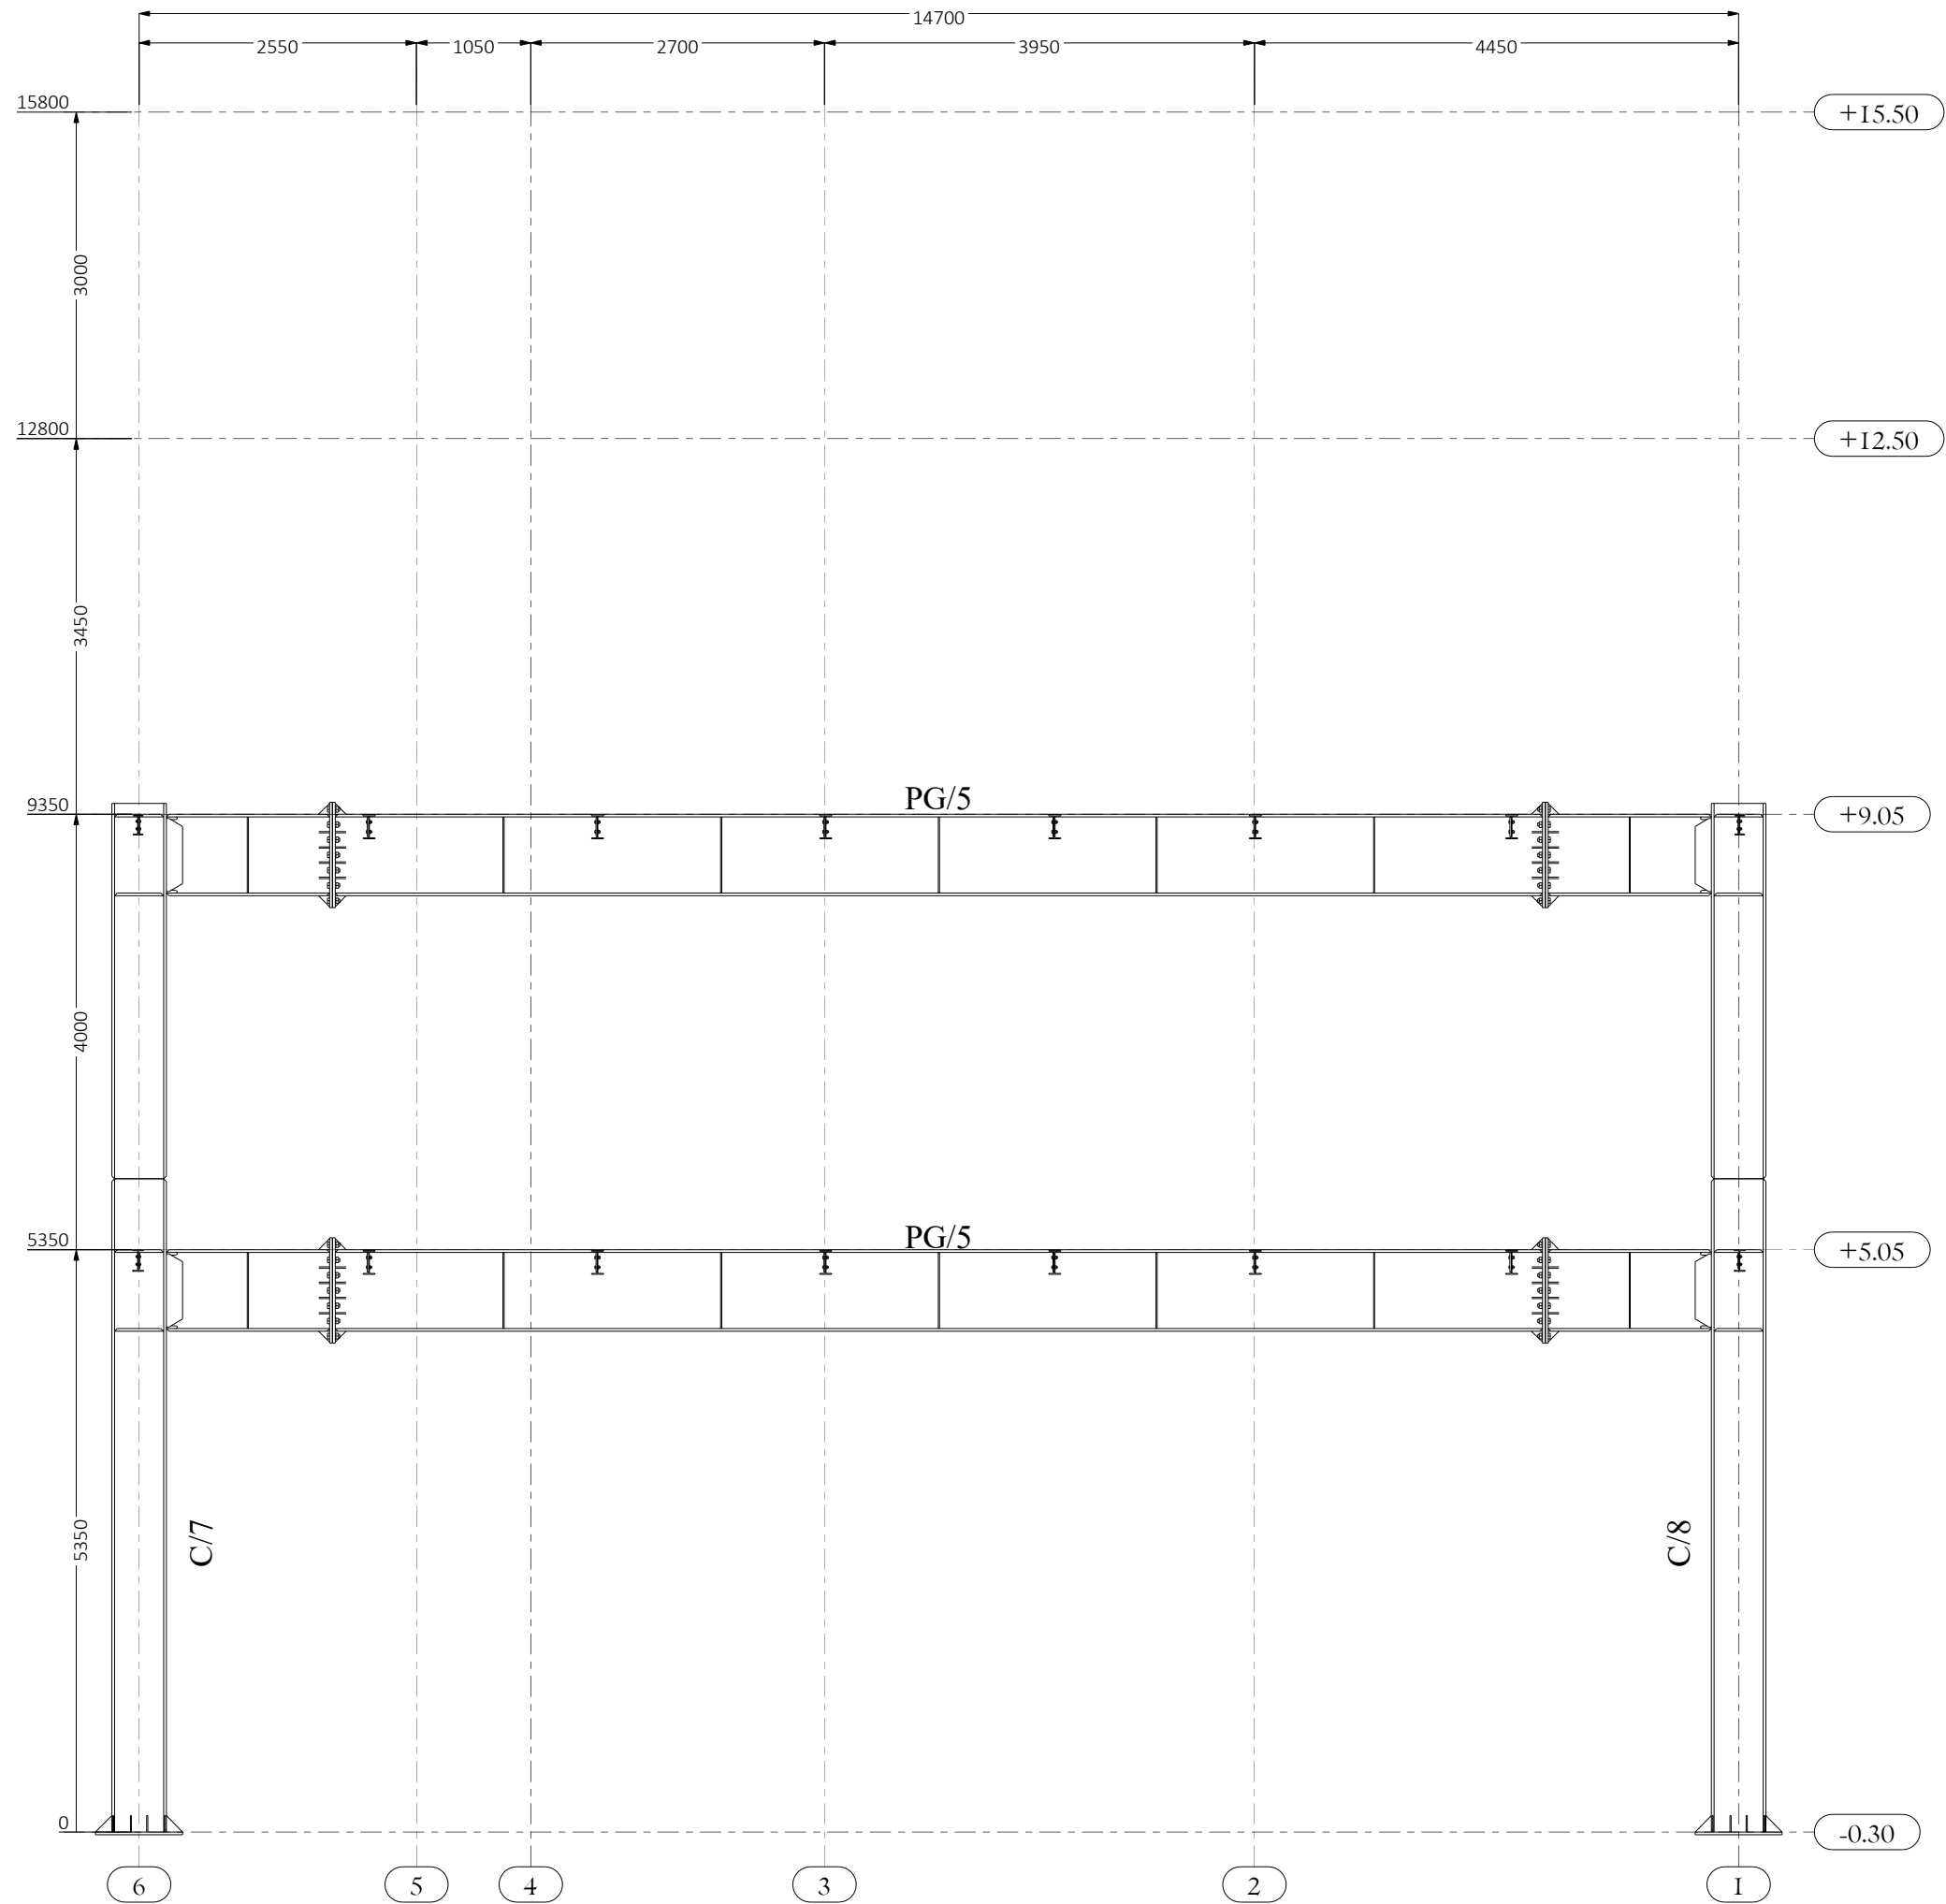


TITLE		Axe D		
CLIENT				
CONTRACTOR		ISSUED		
MODELLED BY		SCALE 1:65		
DRAWING No		[5]	REVISION No. 0	A3

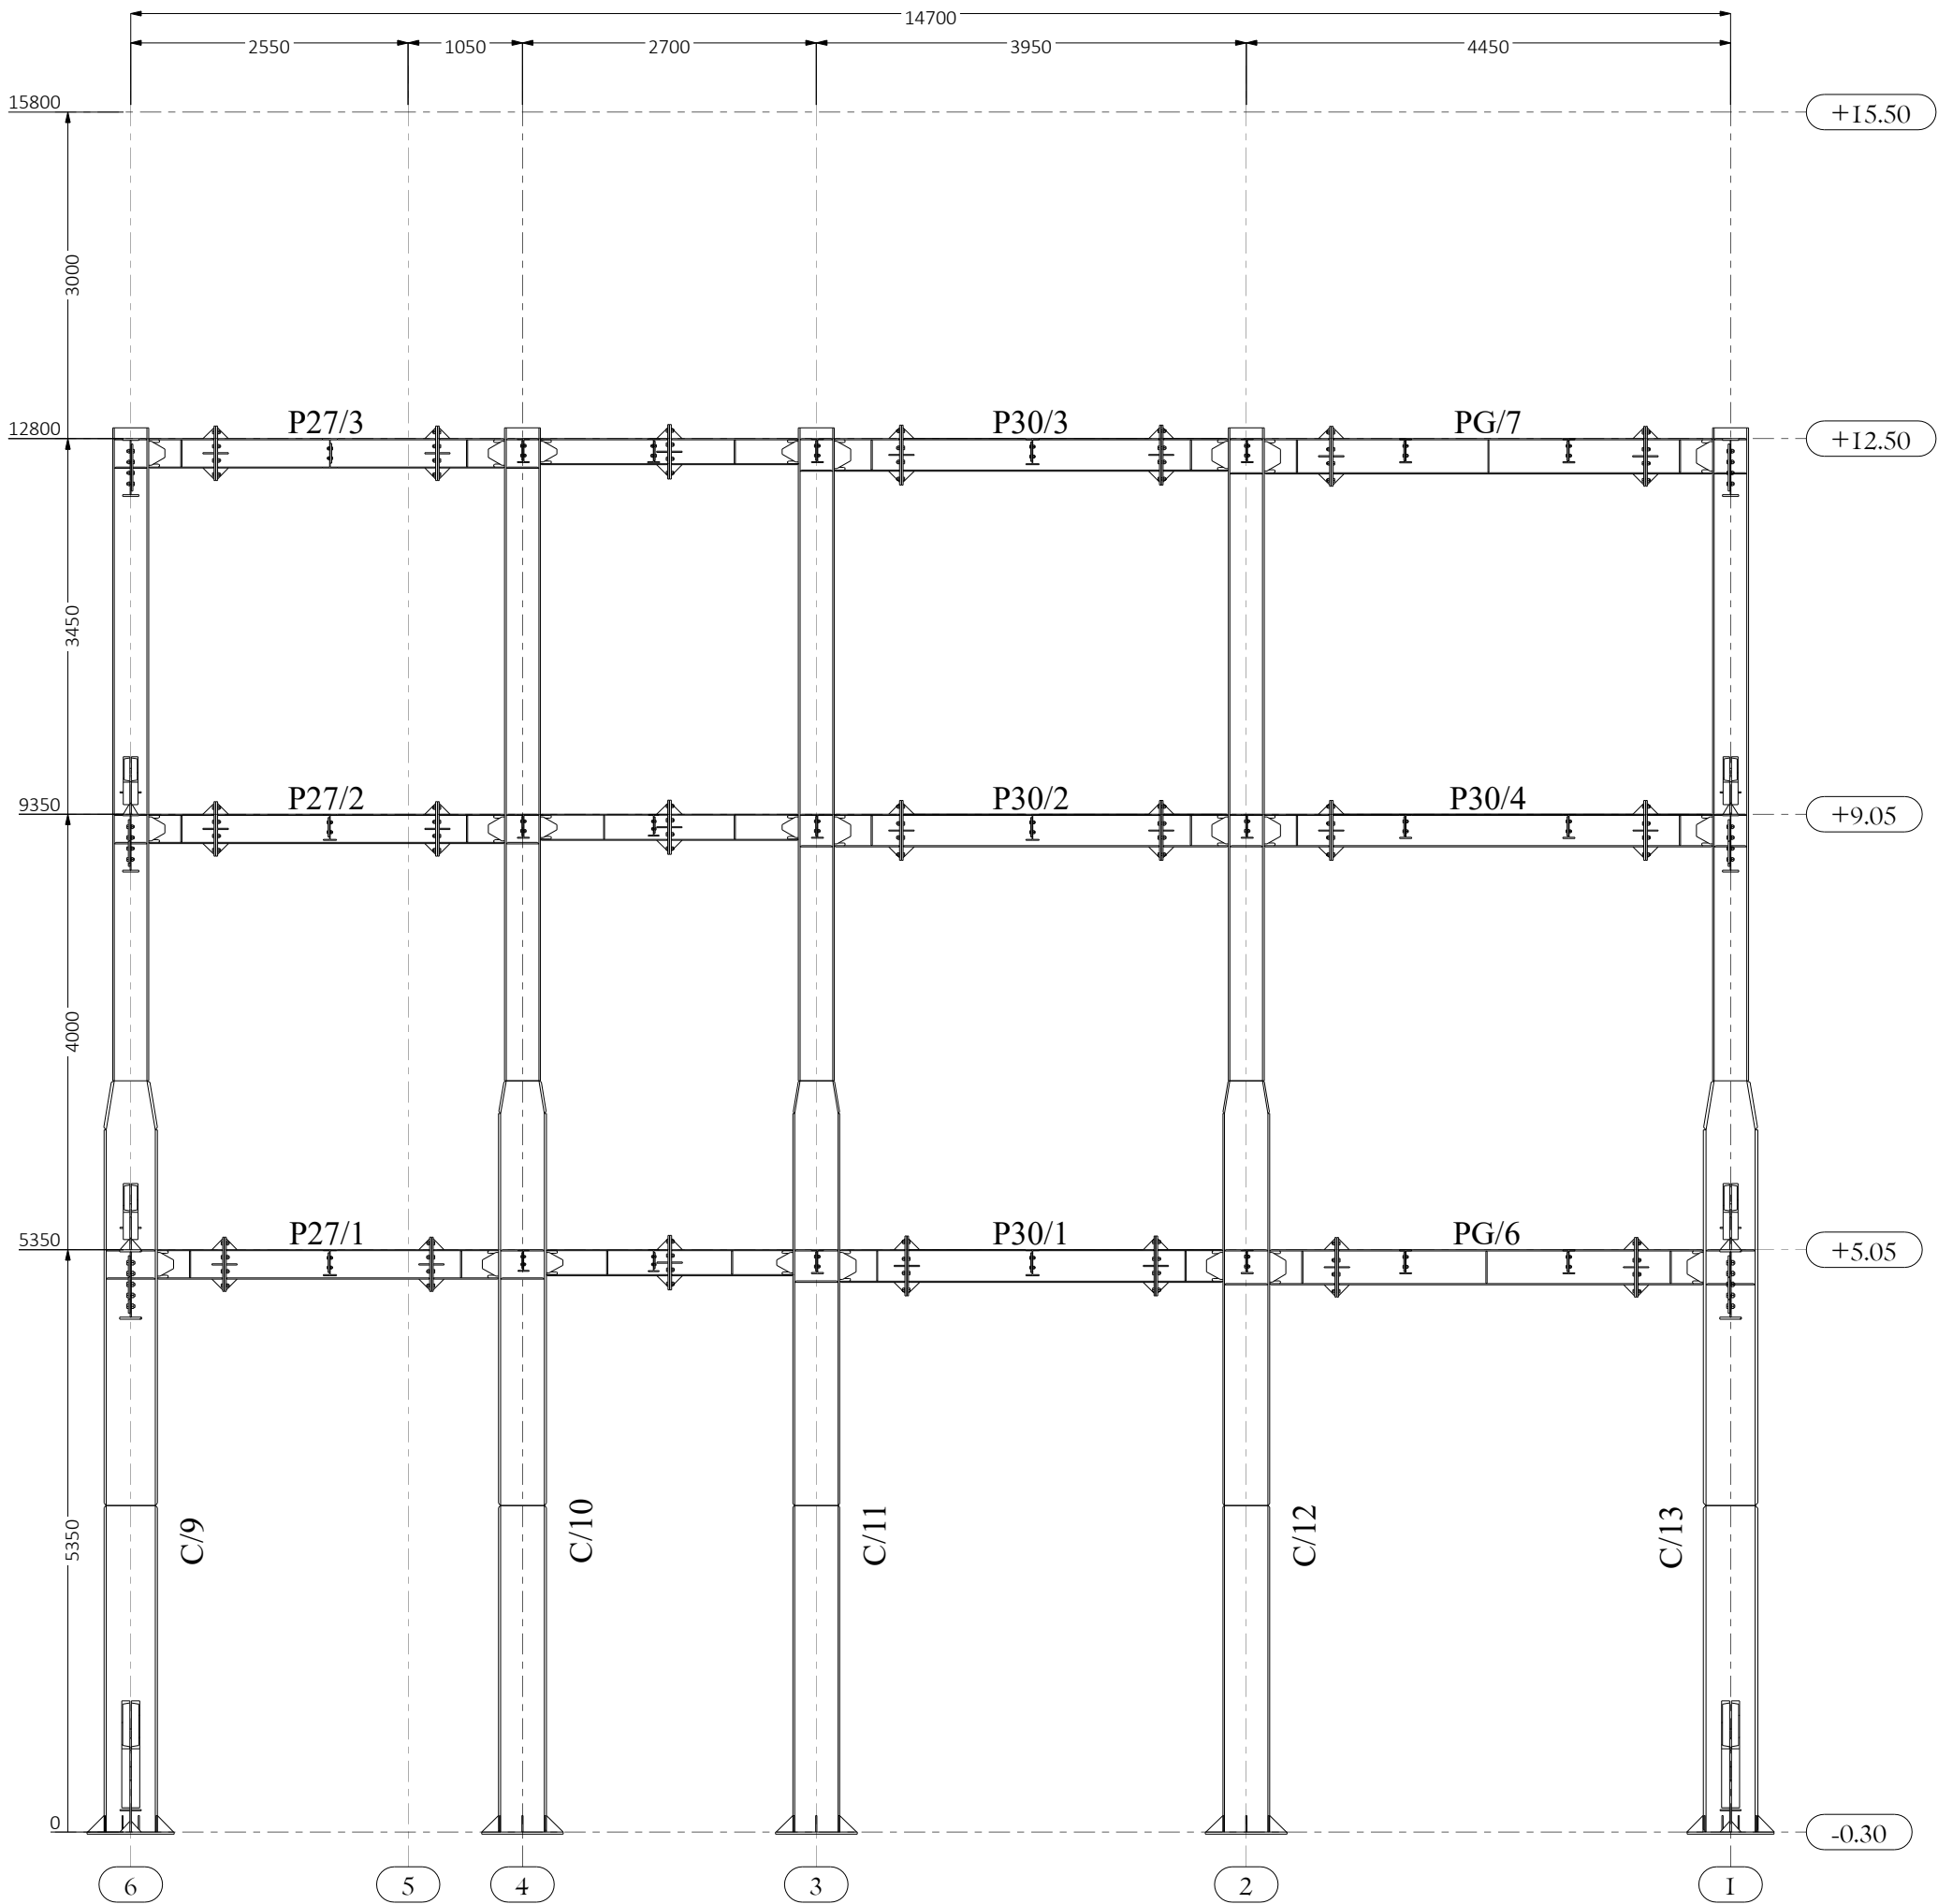


TITLE		Axe E		
CLIENT				
CONTRACTOR		ISSUED		
MODELLED BY	EN ALMASI	SCALE	1:65	
DRAWING No	[6]	REVISION No.	0	A3

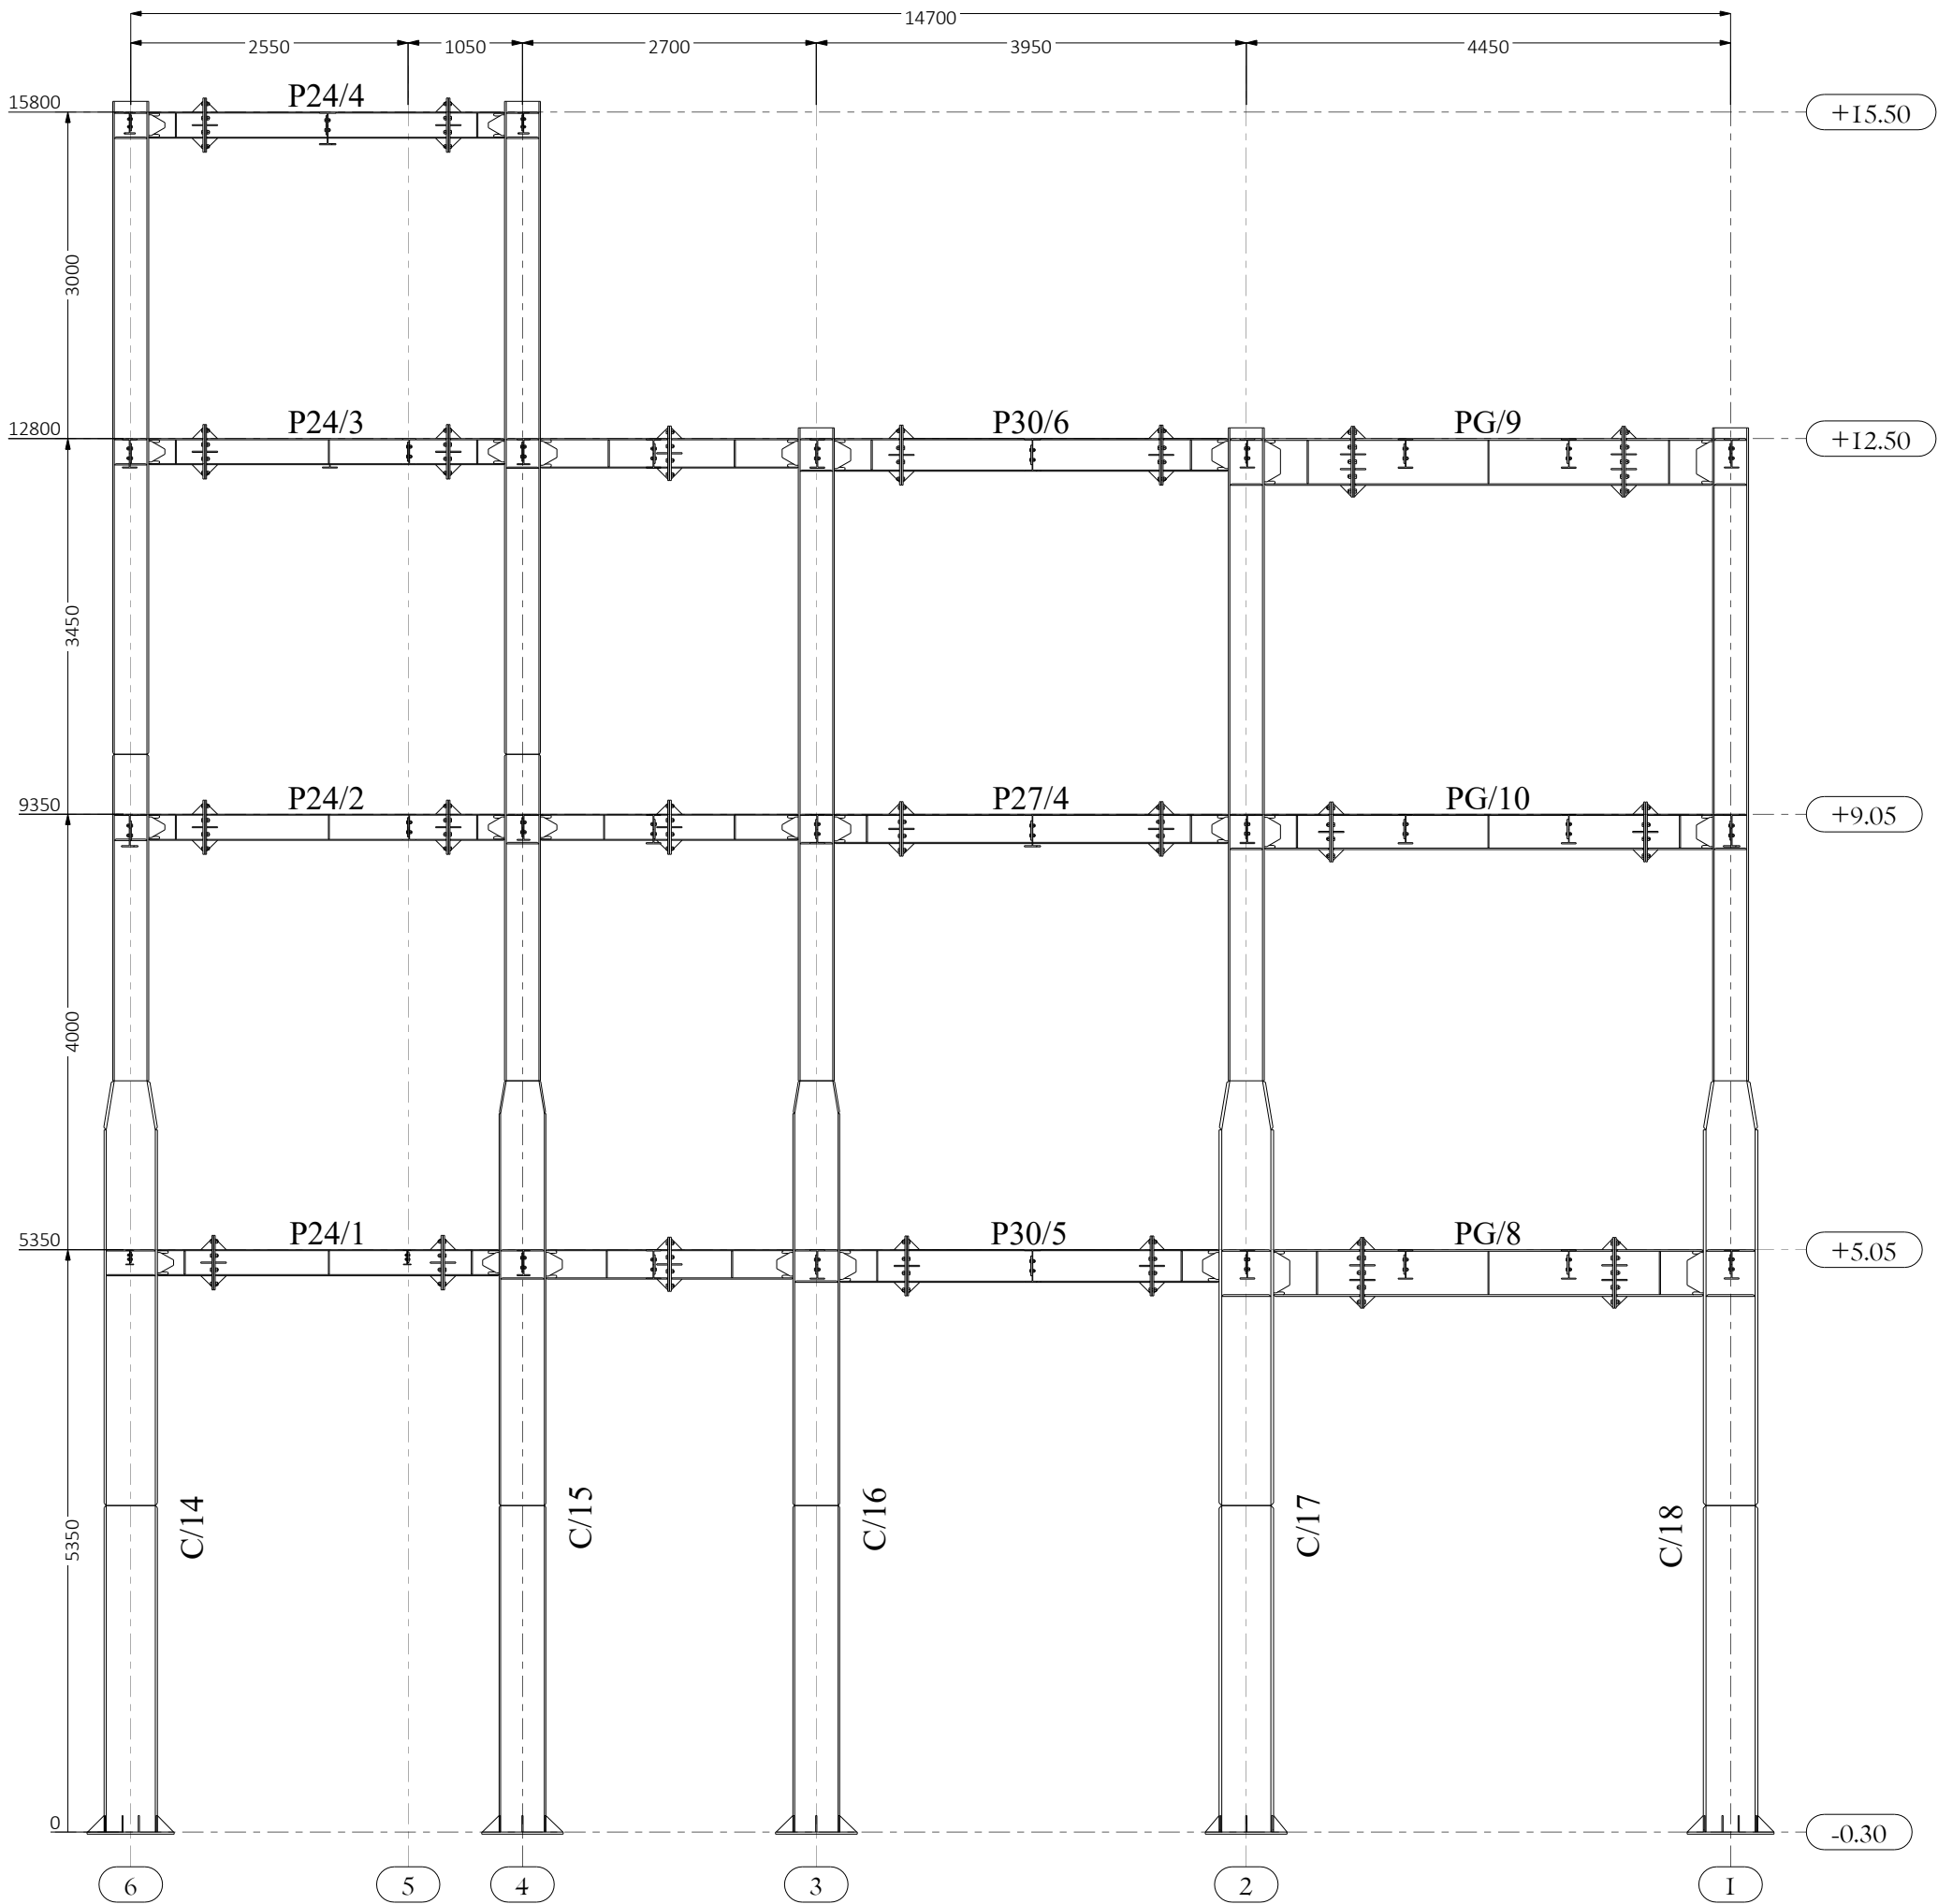


TITLE		Axe F		
CLIENT				
CONTRACTOR			ISSUED	
MODELLED BY		EN ALMASI	SCALE 1:65	
DRAWING No		[7]	REVISION No. 0	A3

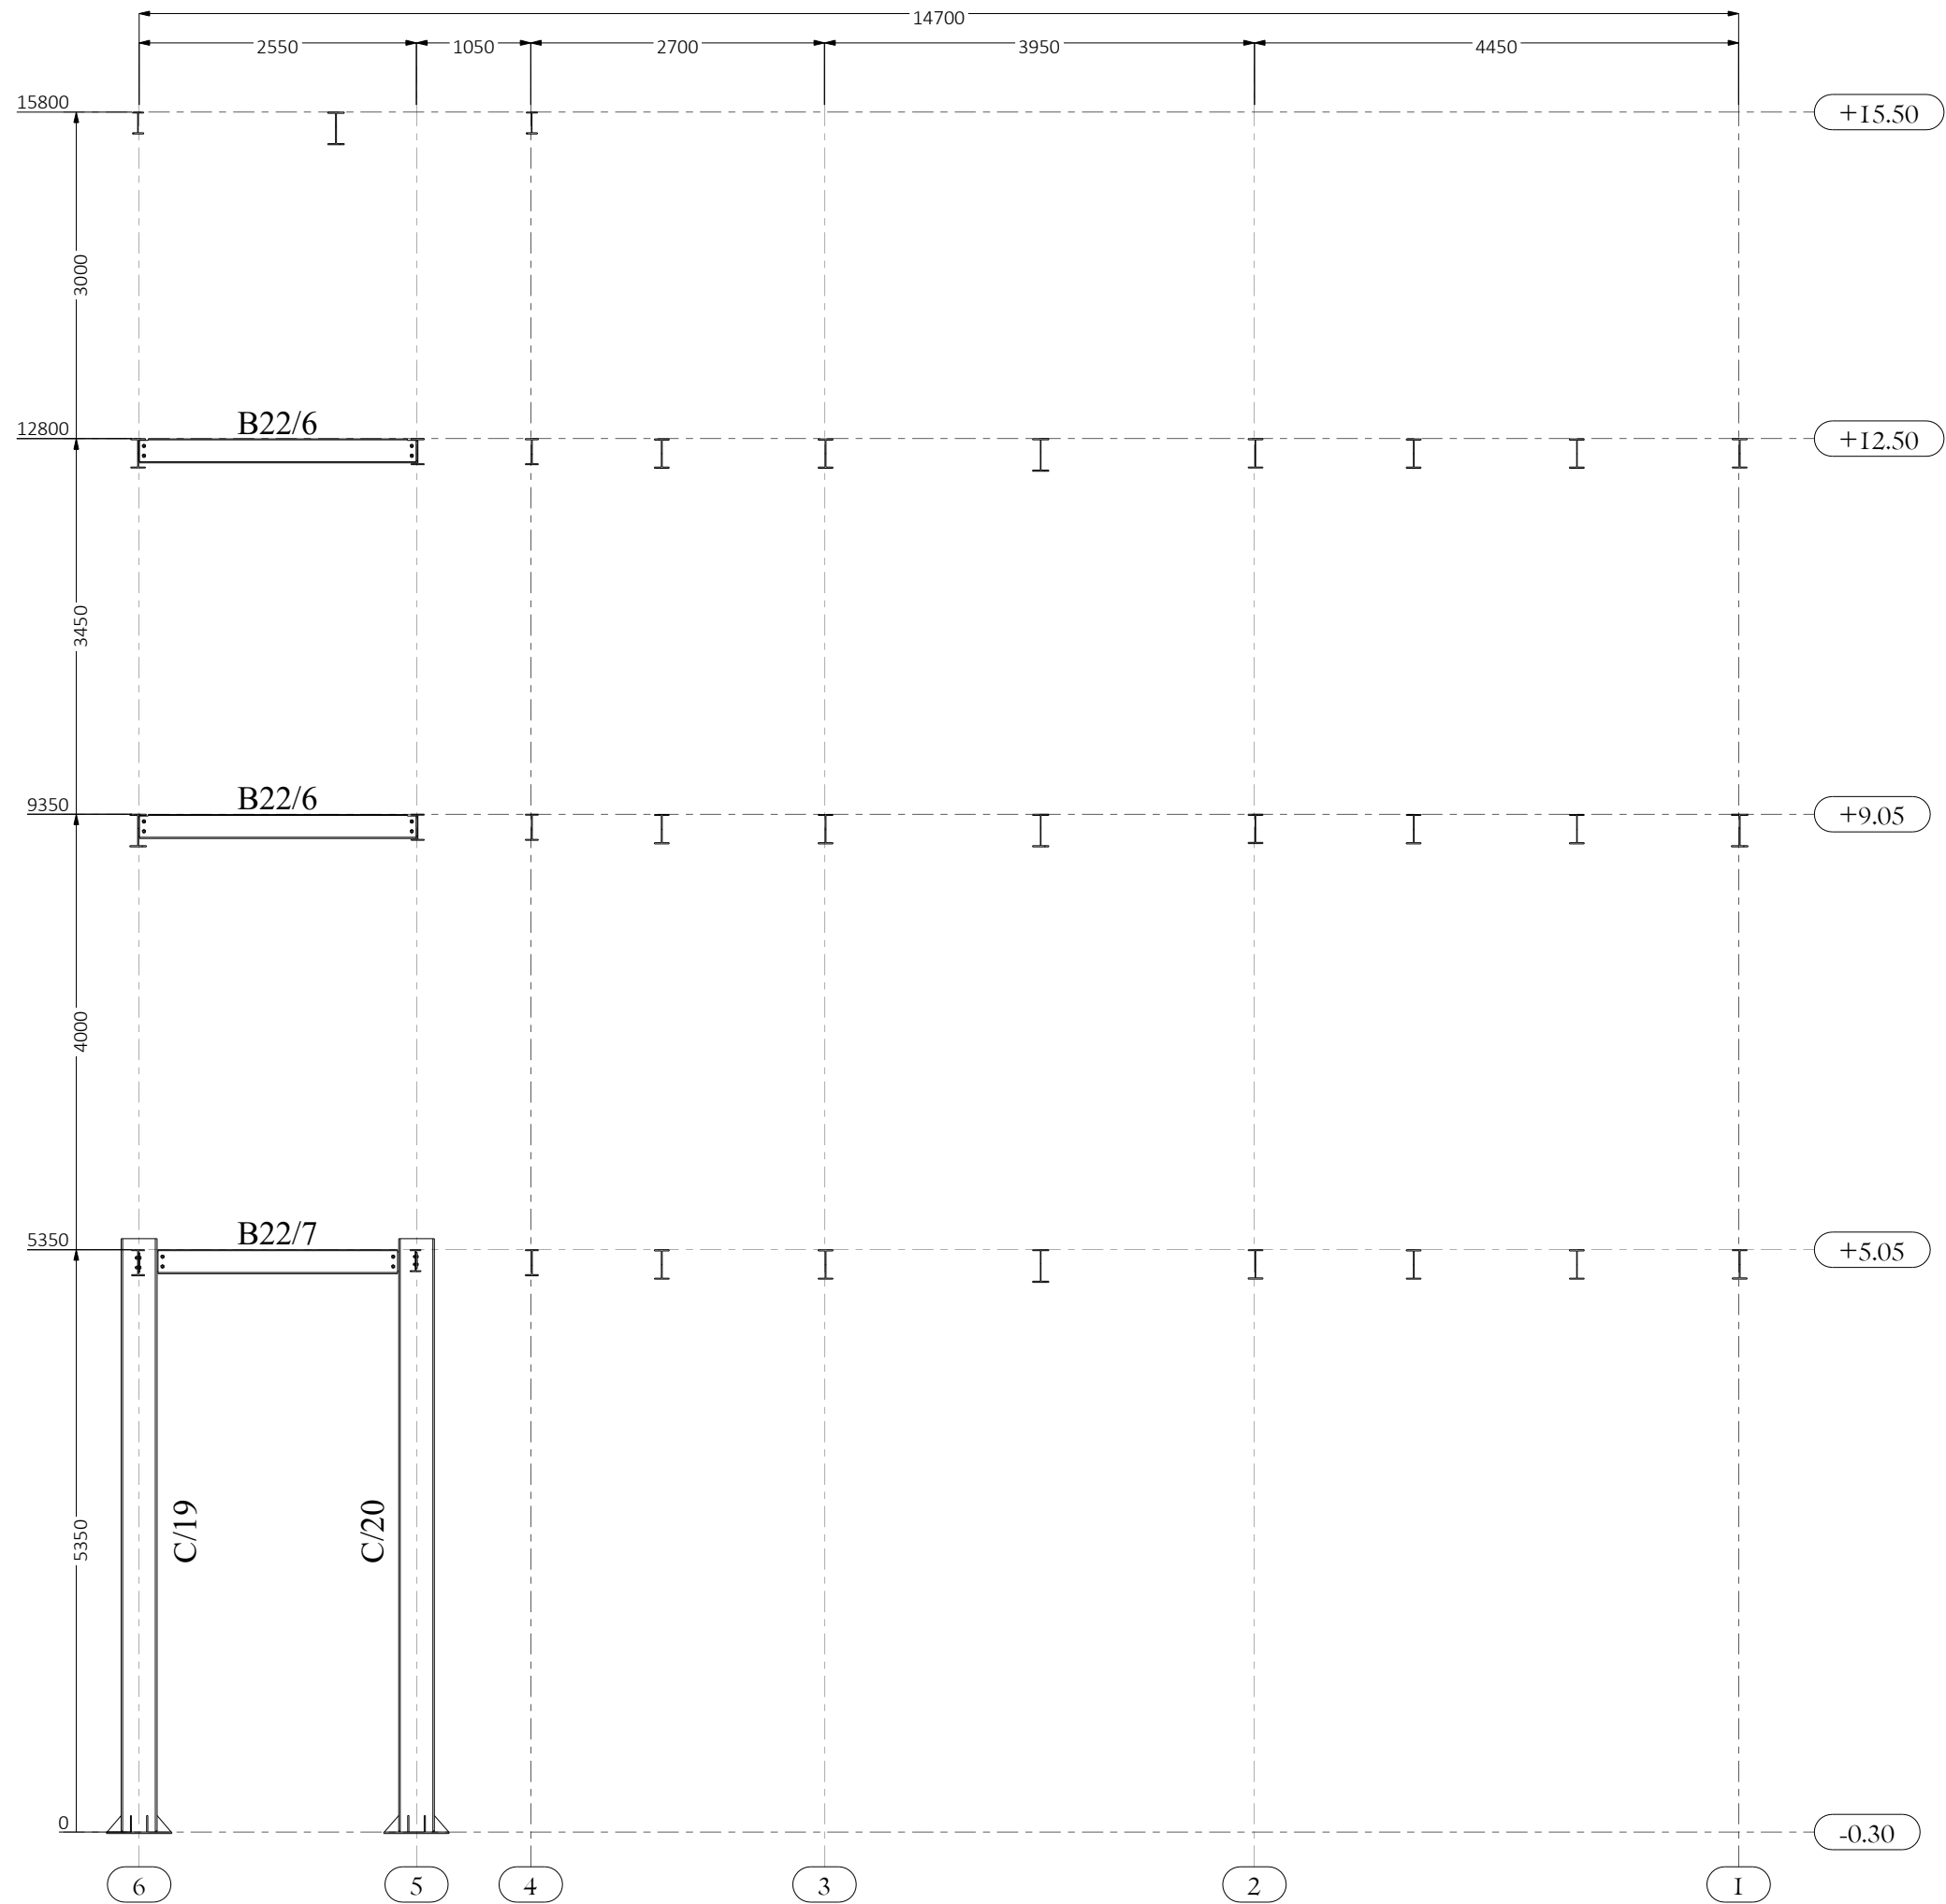


TITLE		Axe G		
CLIENT				
CONTRACTOR		ISSUED		
MODELLED BY	EN ALMASI	SCALE 1:65		A3
DRAWING No	[8]	REVISION No. 0		

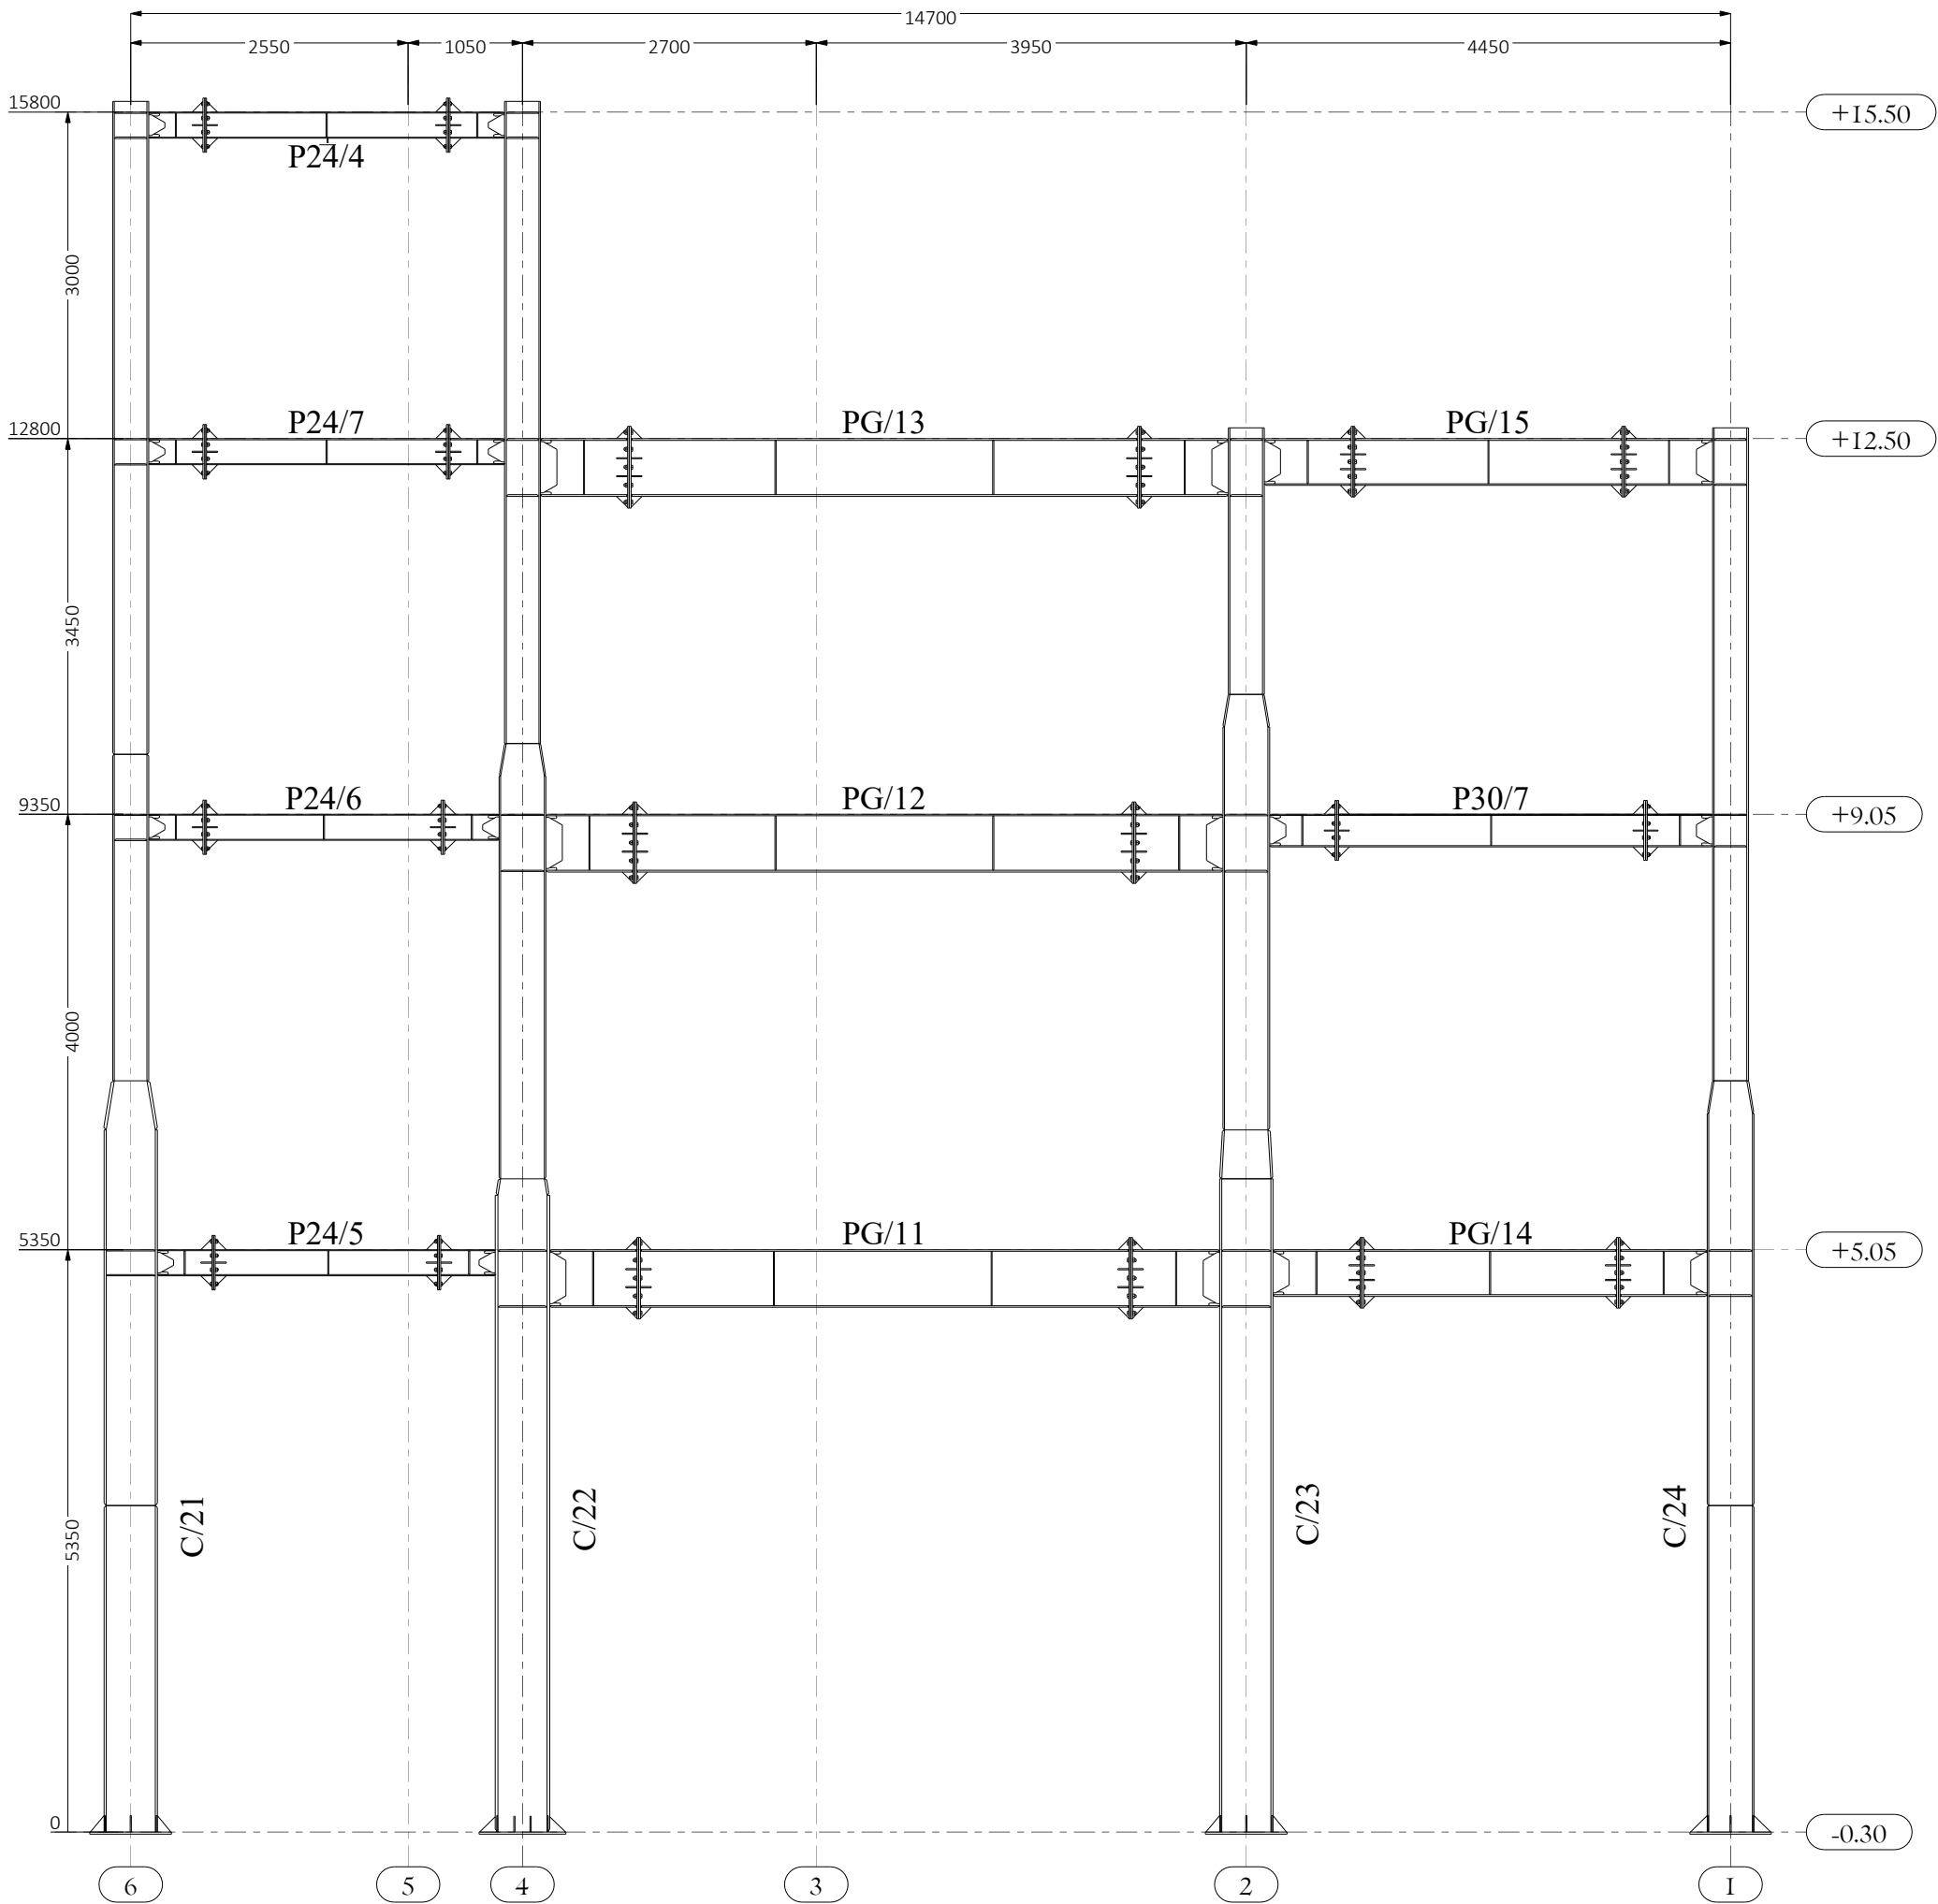


TITLE		Axe H		
CLIENT				
CONTRACTOR			ISSUED	
MODELLED BY		EN ALMASI	SCALE 1:65	
DRAWING No		[9]	REVISION No. 0	A3

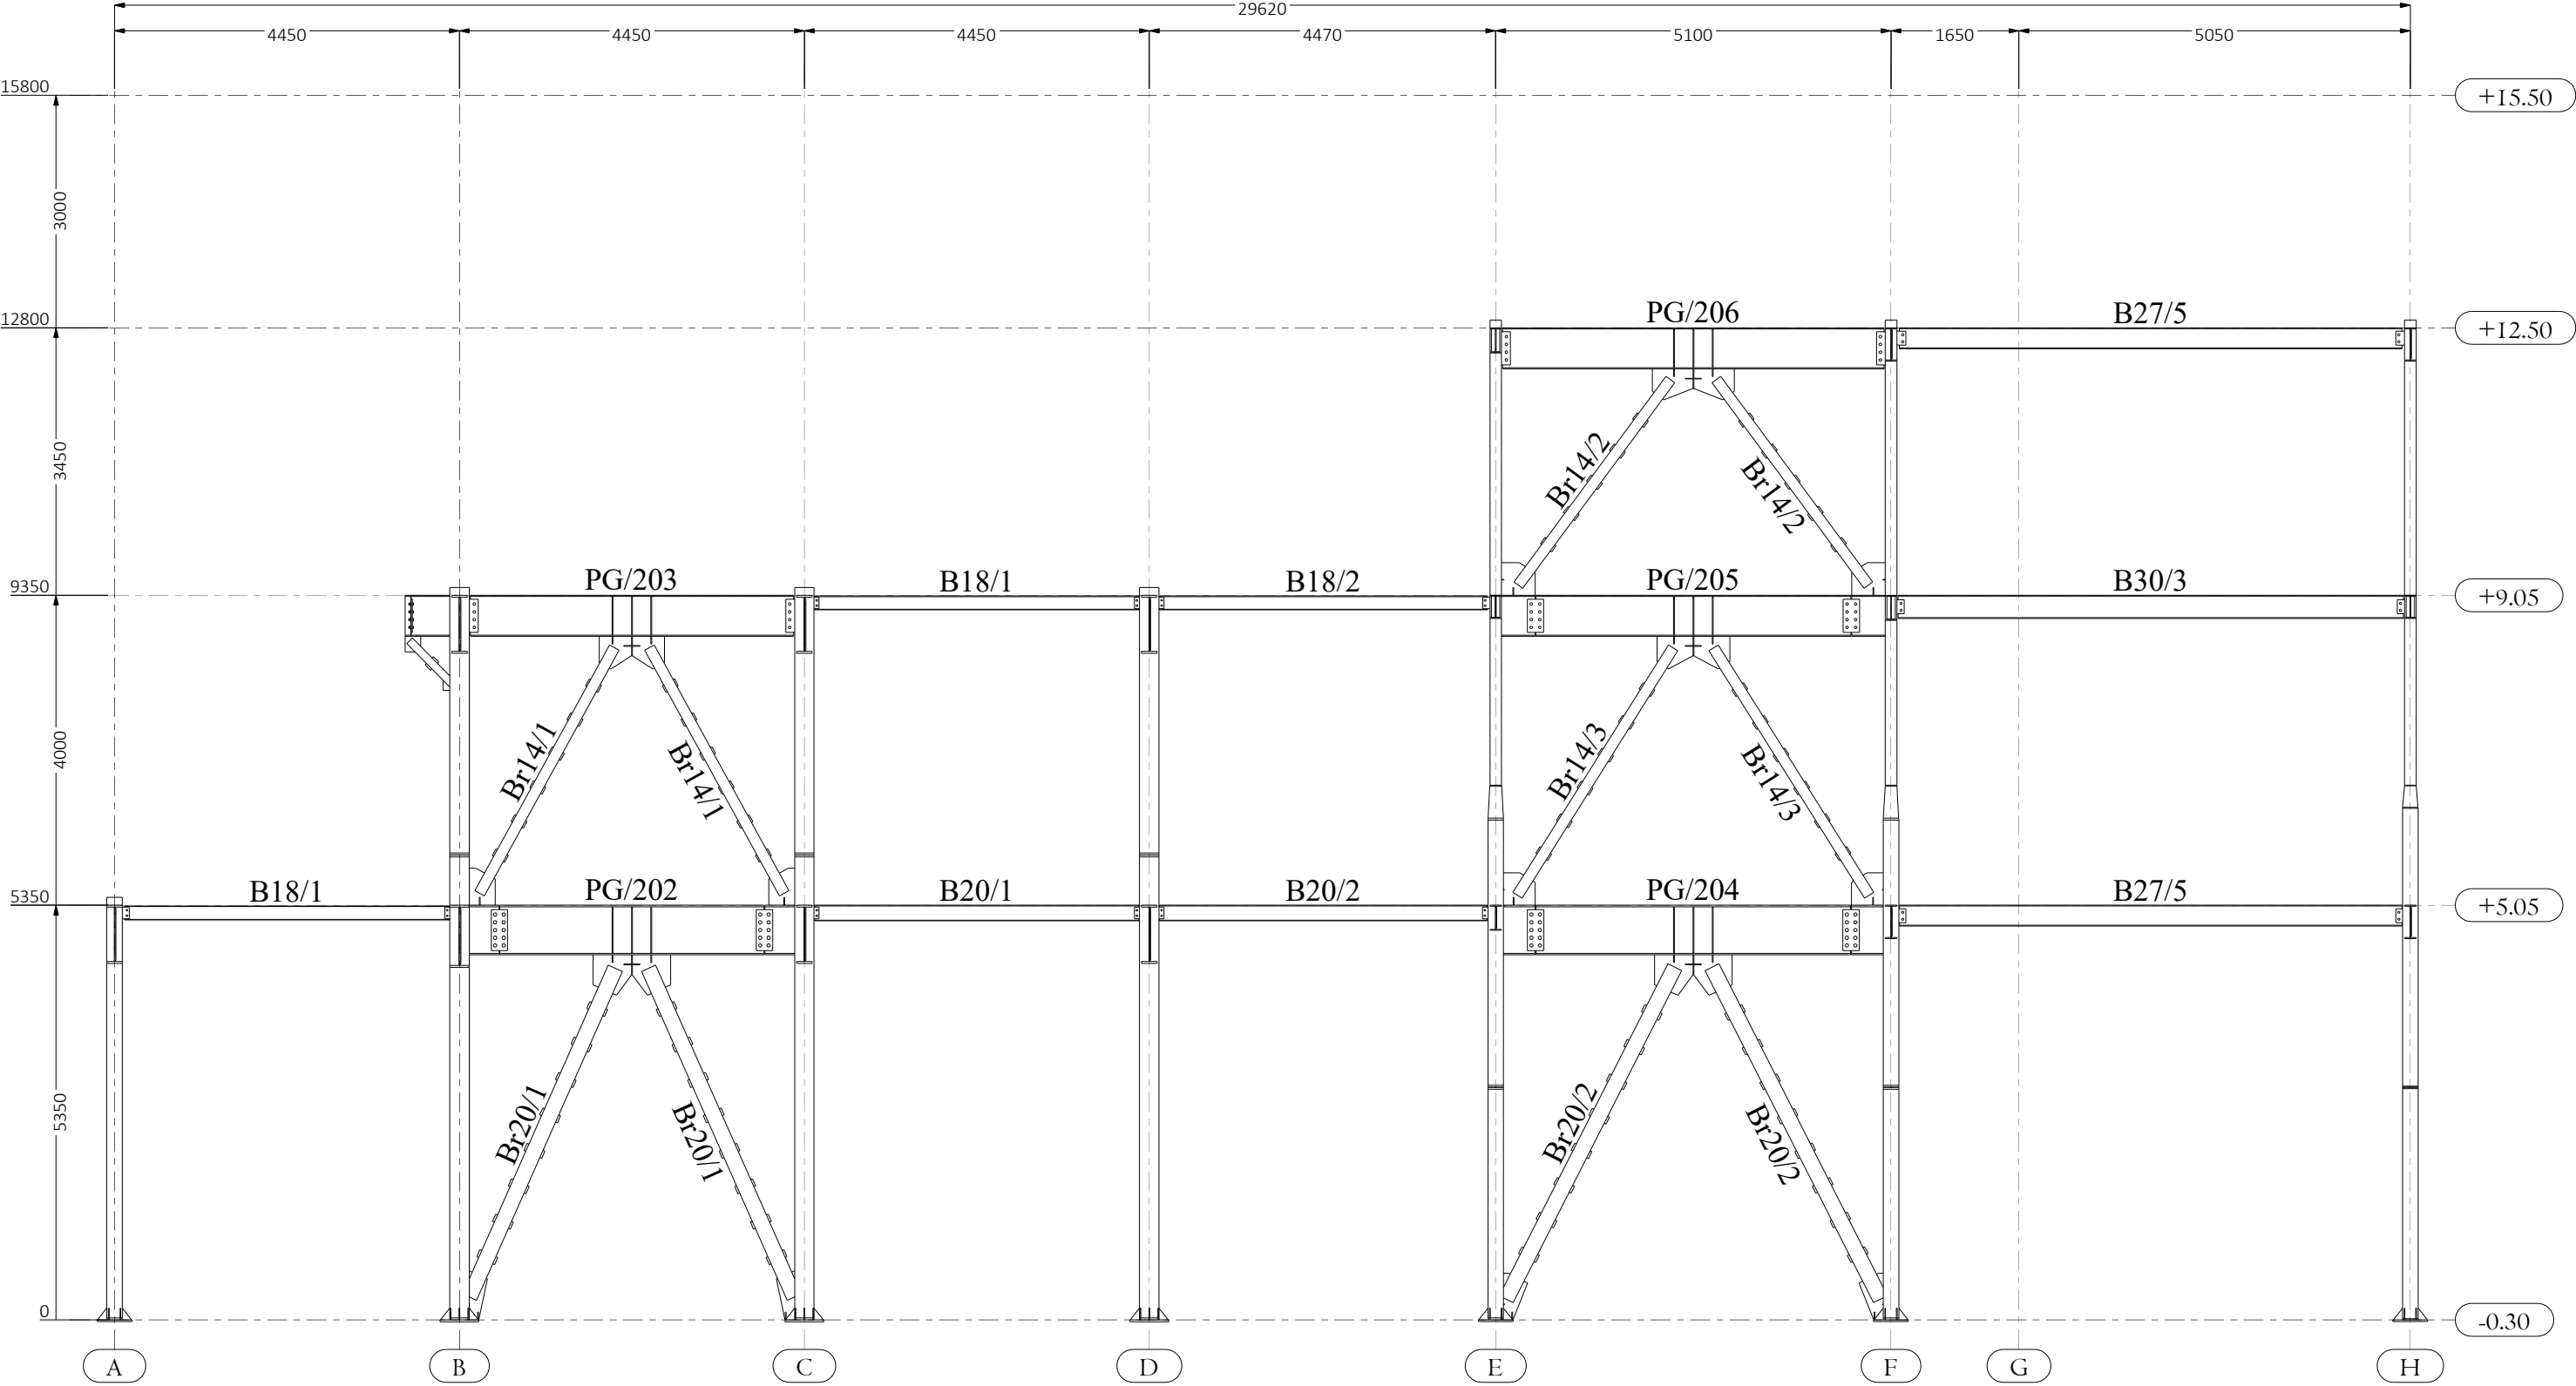


TITLE		Axe 1		
CLIENT				
CONTRACTOR			ISSUED	
MODELLED BY		EN ALMASI	SCALE 1:85	
DRAWING No		[10]	REVISION No. 0	
A3				

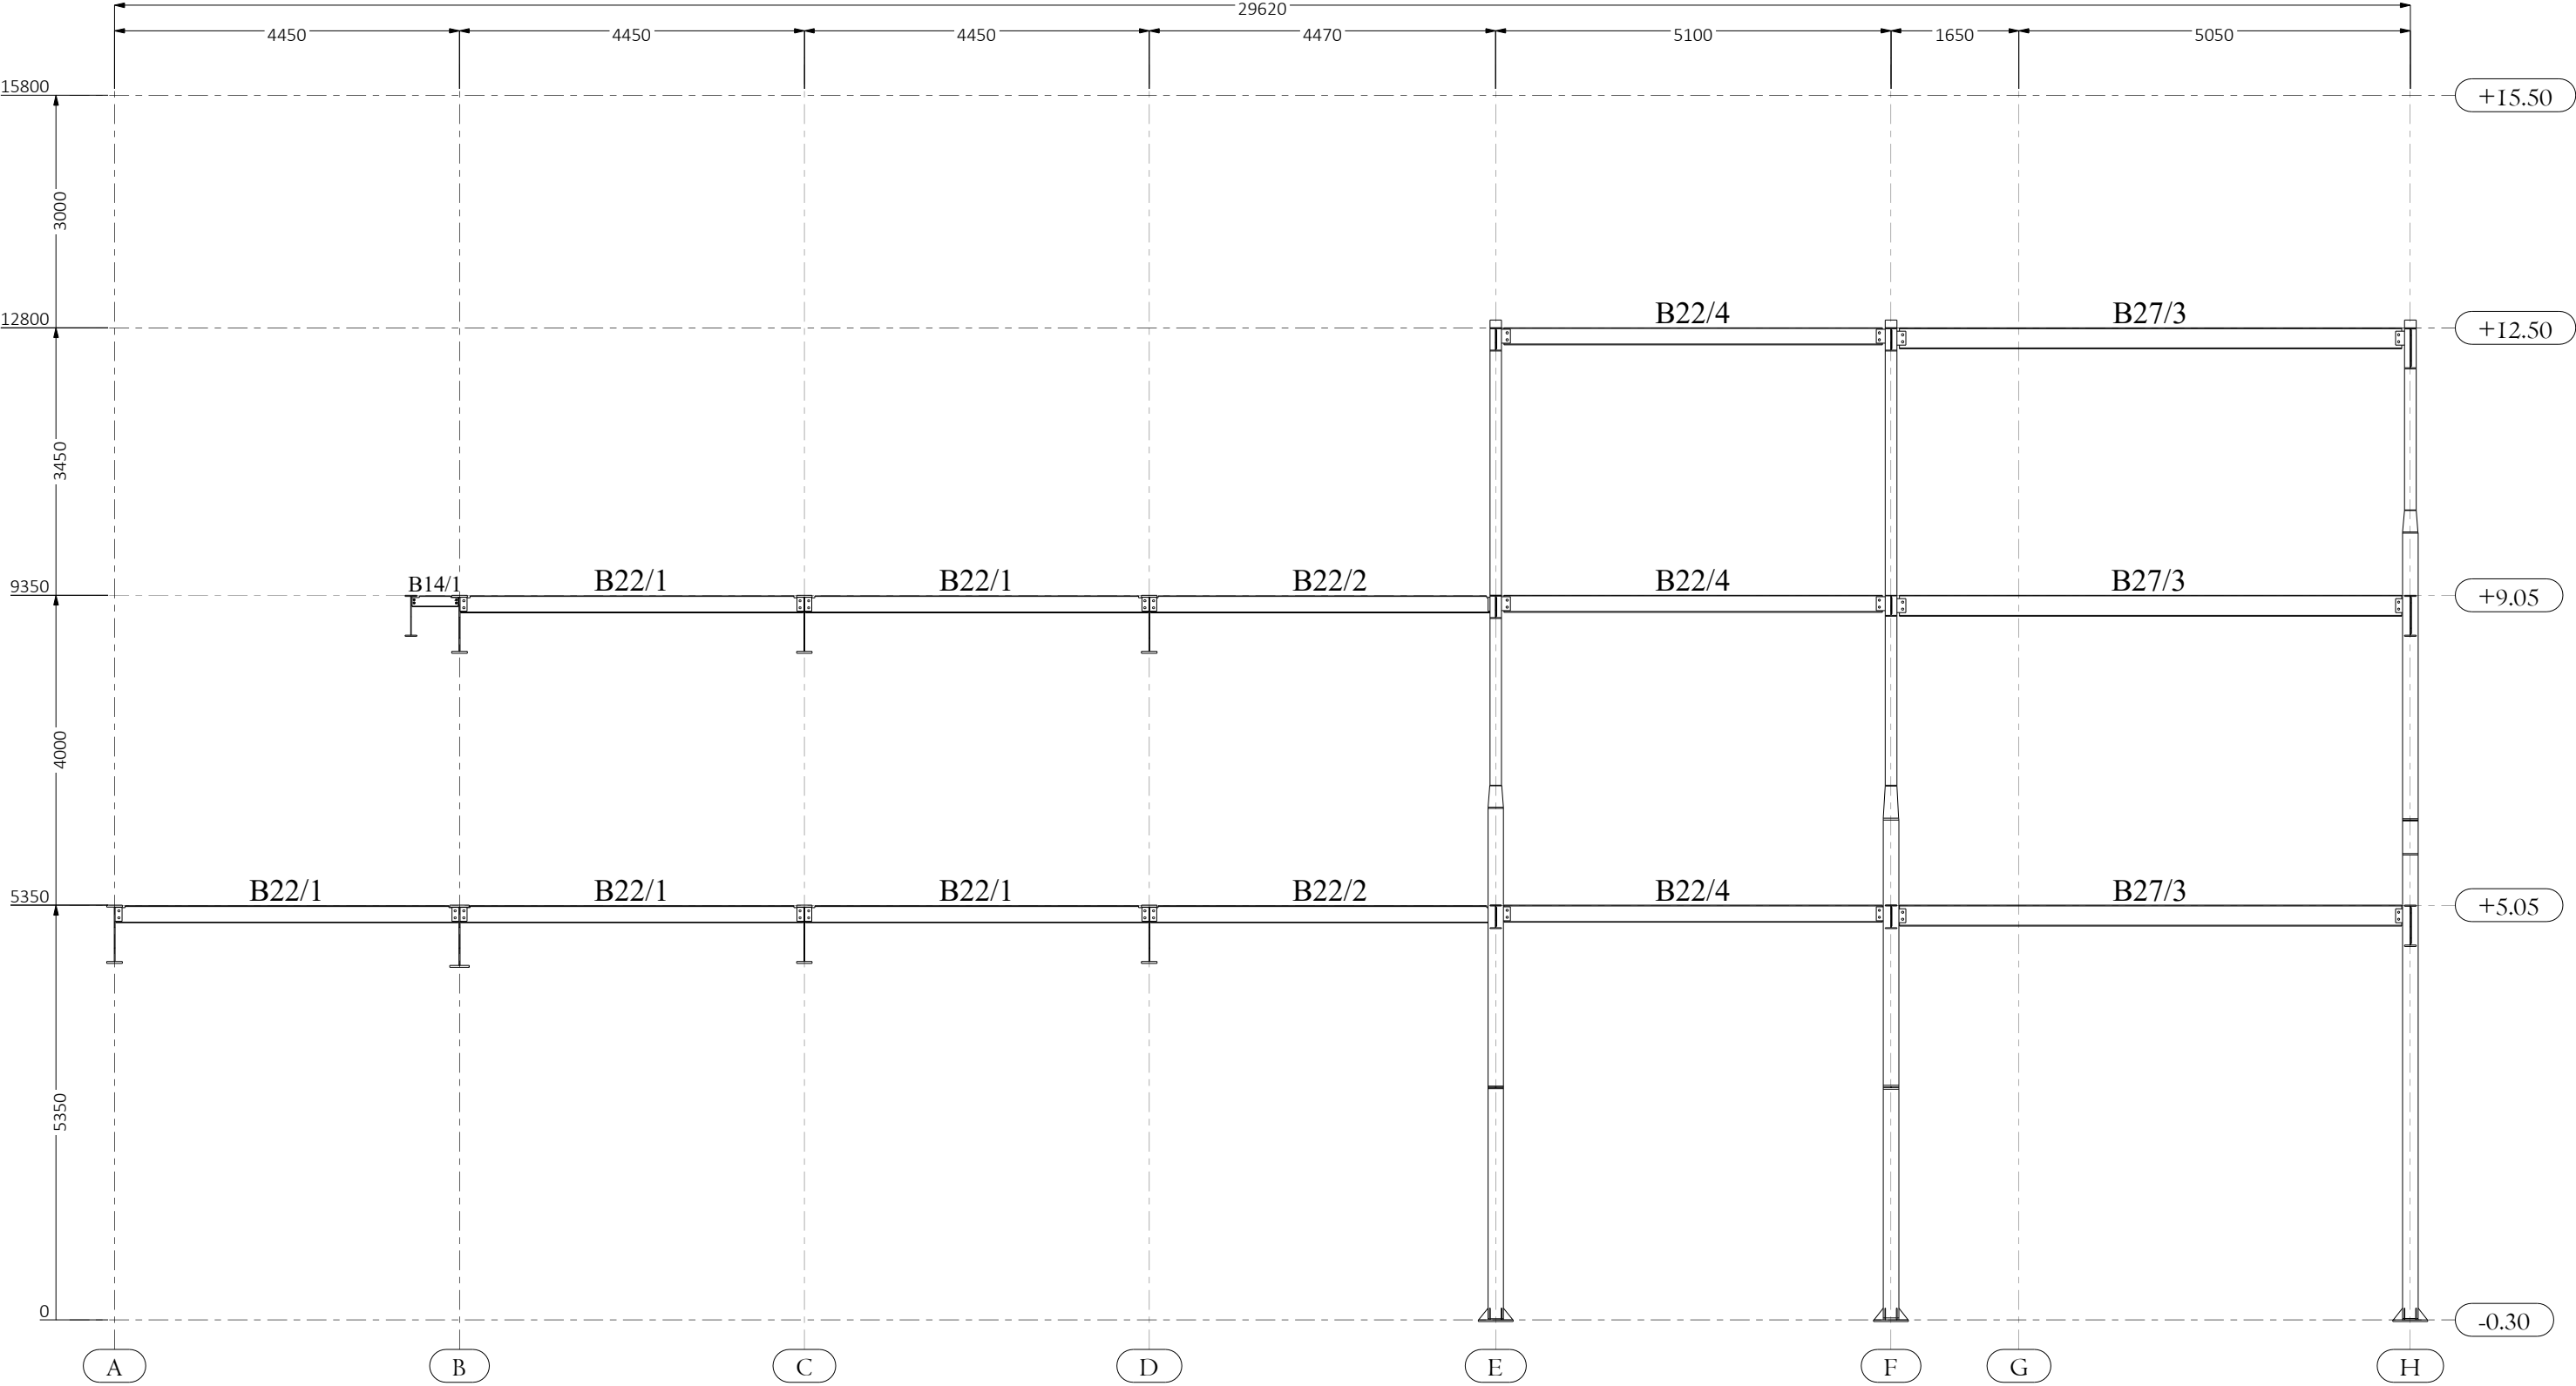


TITLE		Axe 2		
CLIENT				
CONTRACTOR			ISSUED	
MODELLED BY		EN ALMASI	SCALE 1:85	
DRAWING No		[11]	REVISION No. 0	
A3				

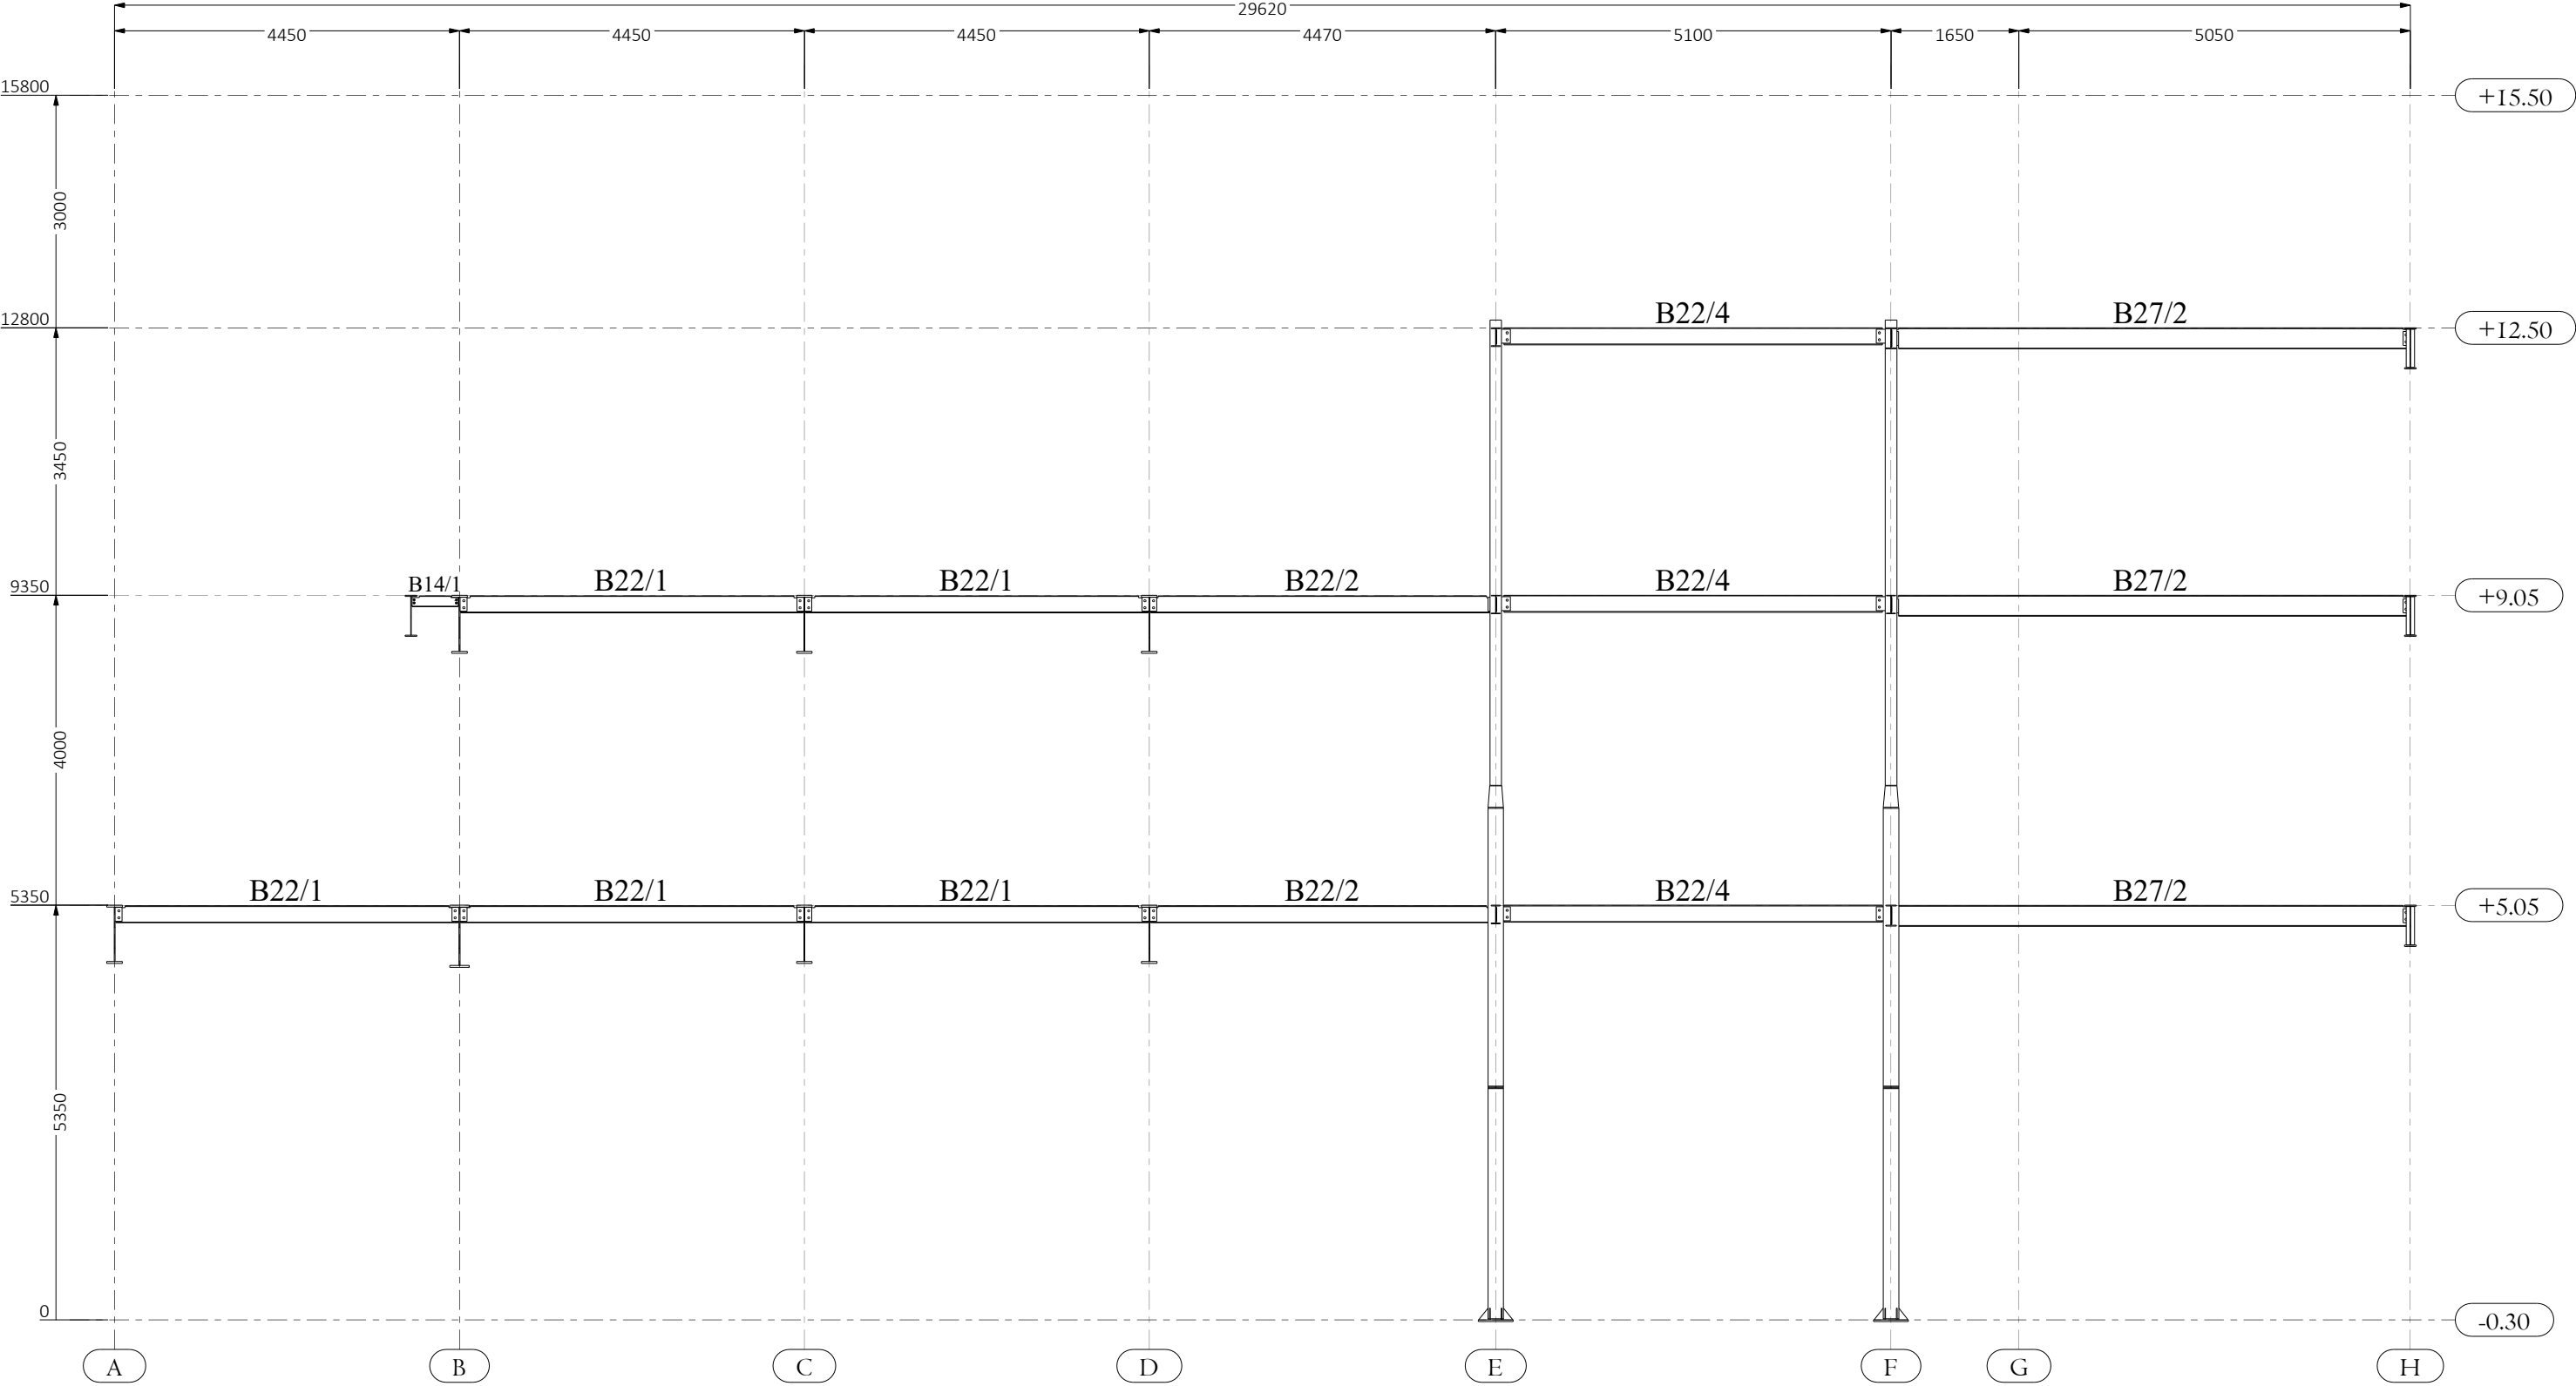


TITLE		Axe 3		
CLIENT				
CONTRACTOR			ISSUED	
MODELLED BY		EN ALMASI	SCALE 1:85	
DRAWING No		[12]	REVISION No. 0	
A3				

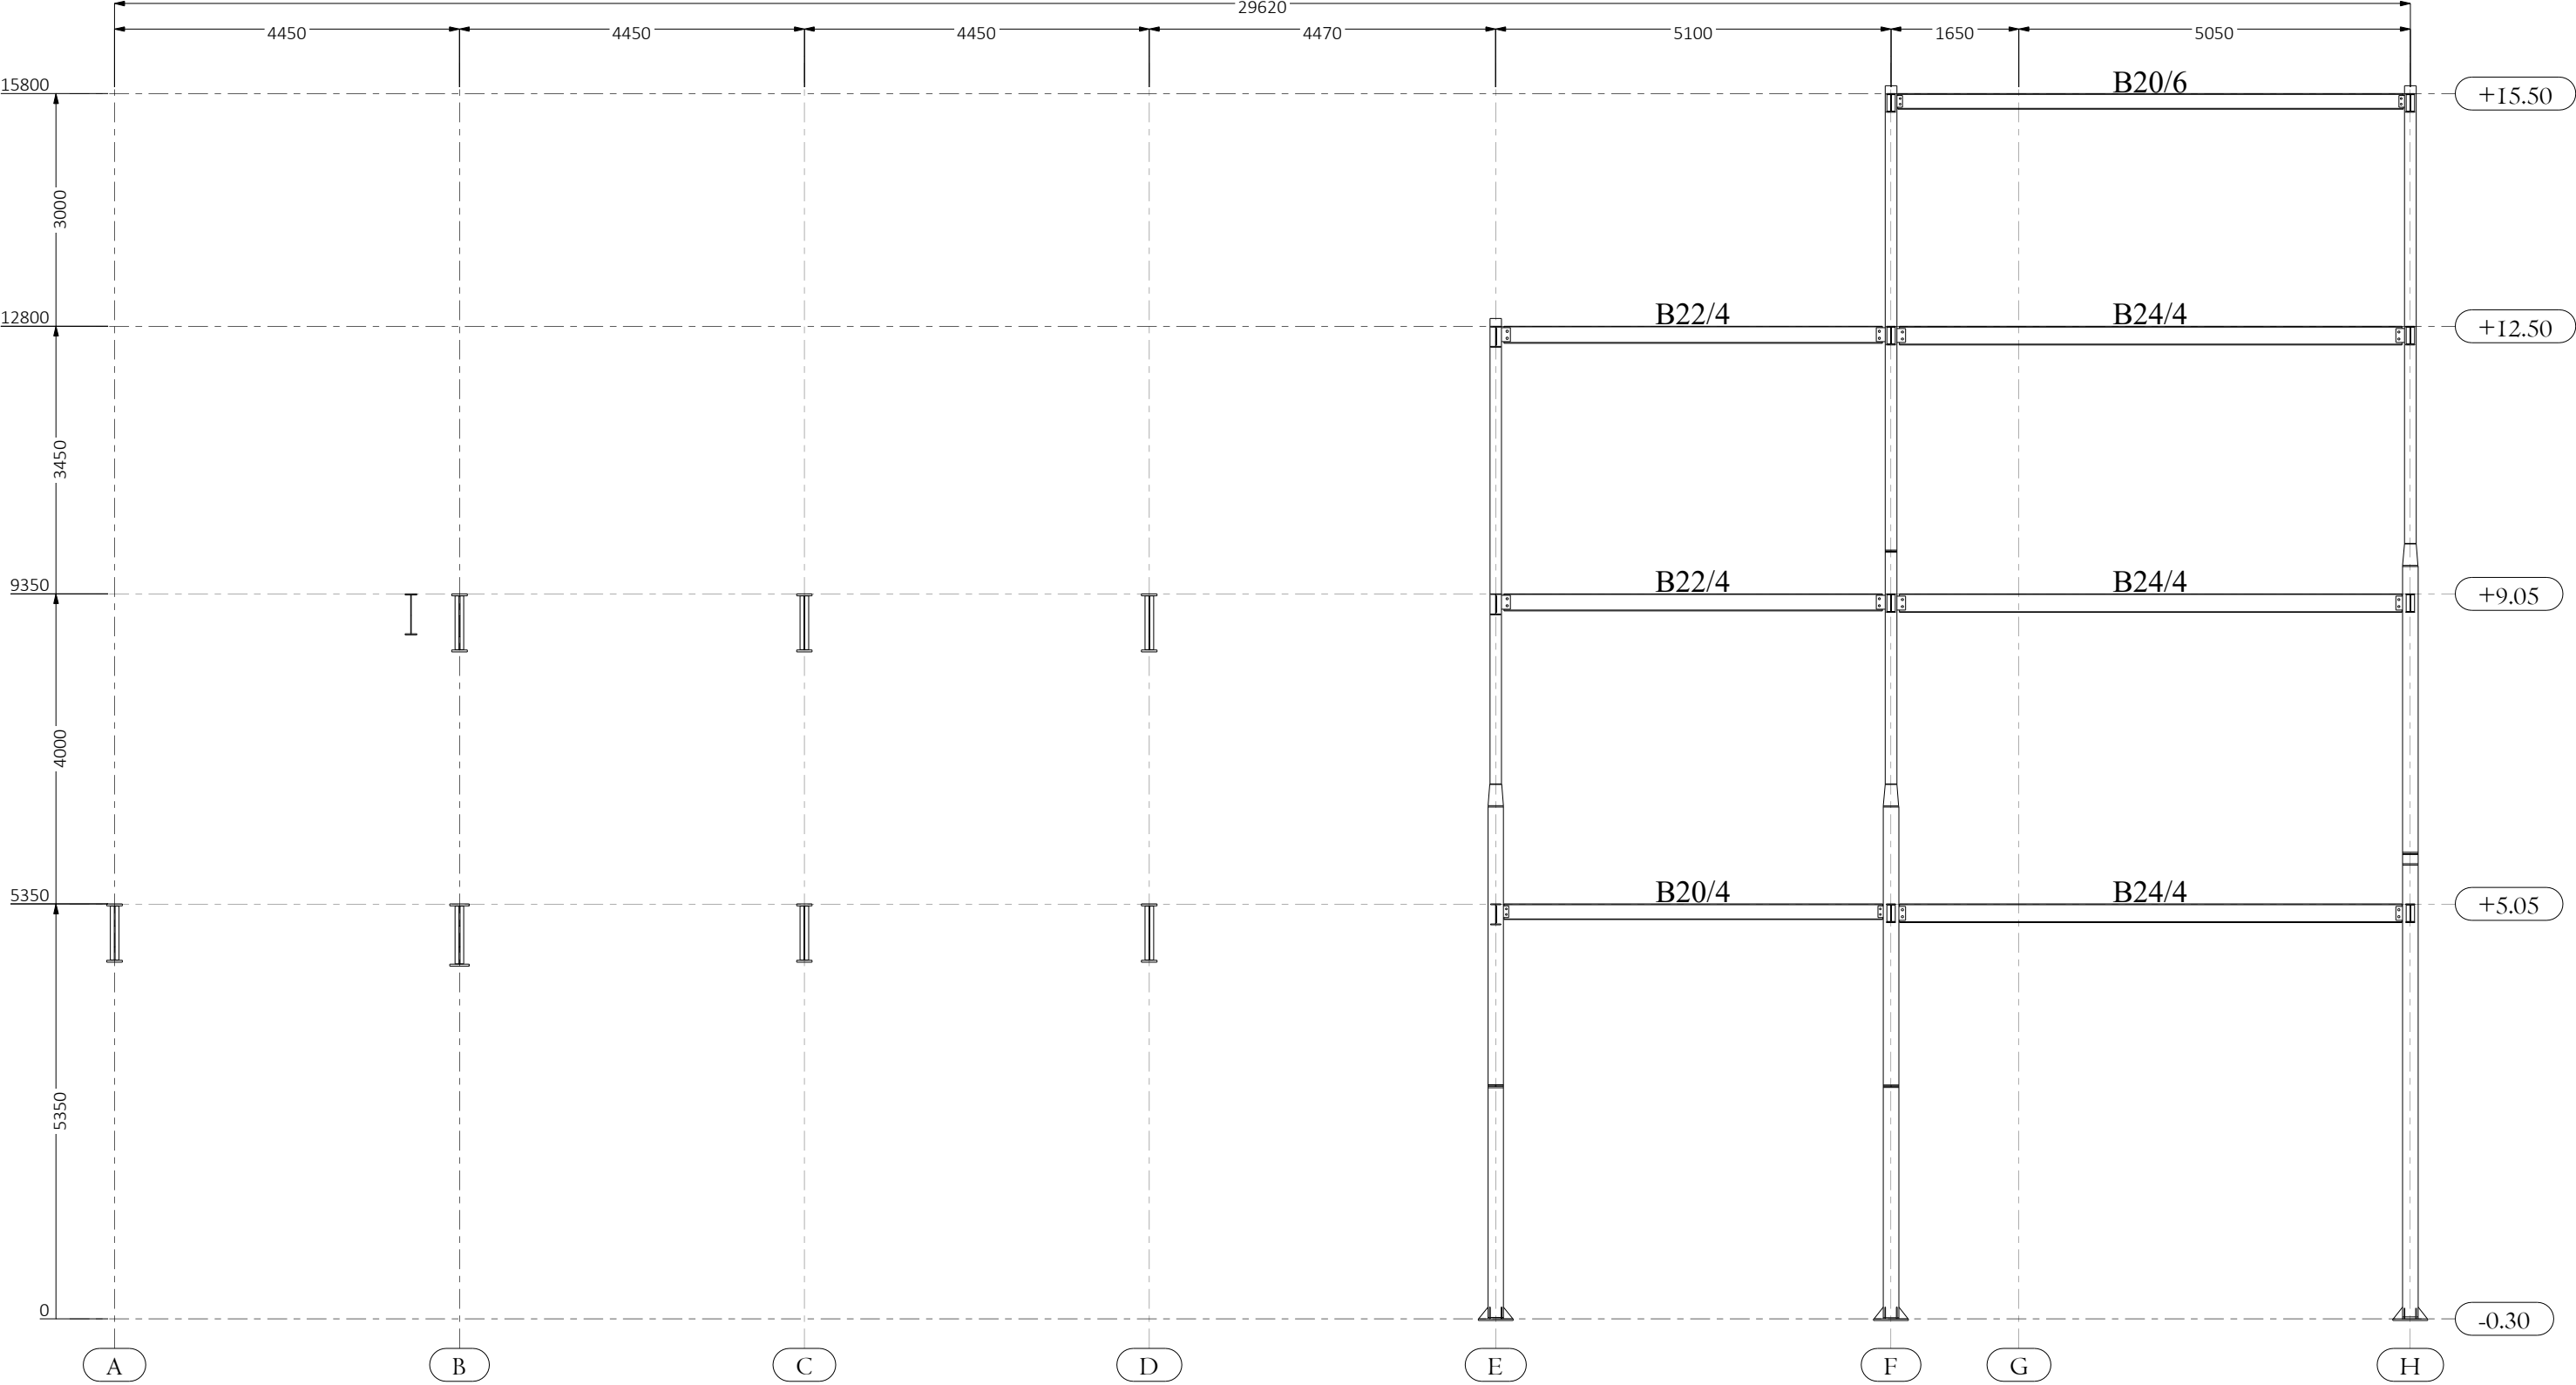

TITLE		Axe 4		
CLIENT				
CONTRACTOR			ISSUED	
MODELLED BY		EN ALMASI	SCALE 1:85	
DRAWING No		[13]	REVISION No. 0	
			A3	

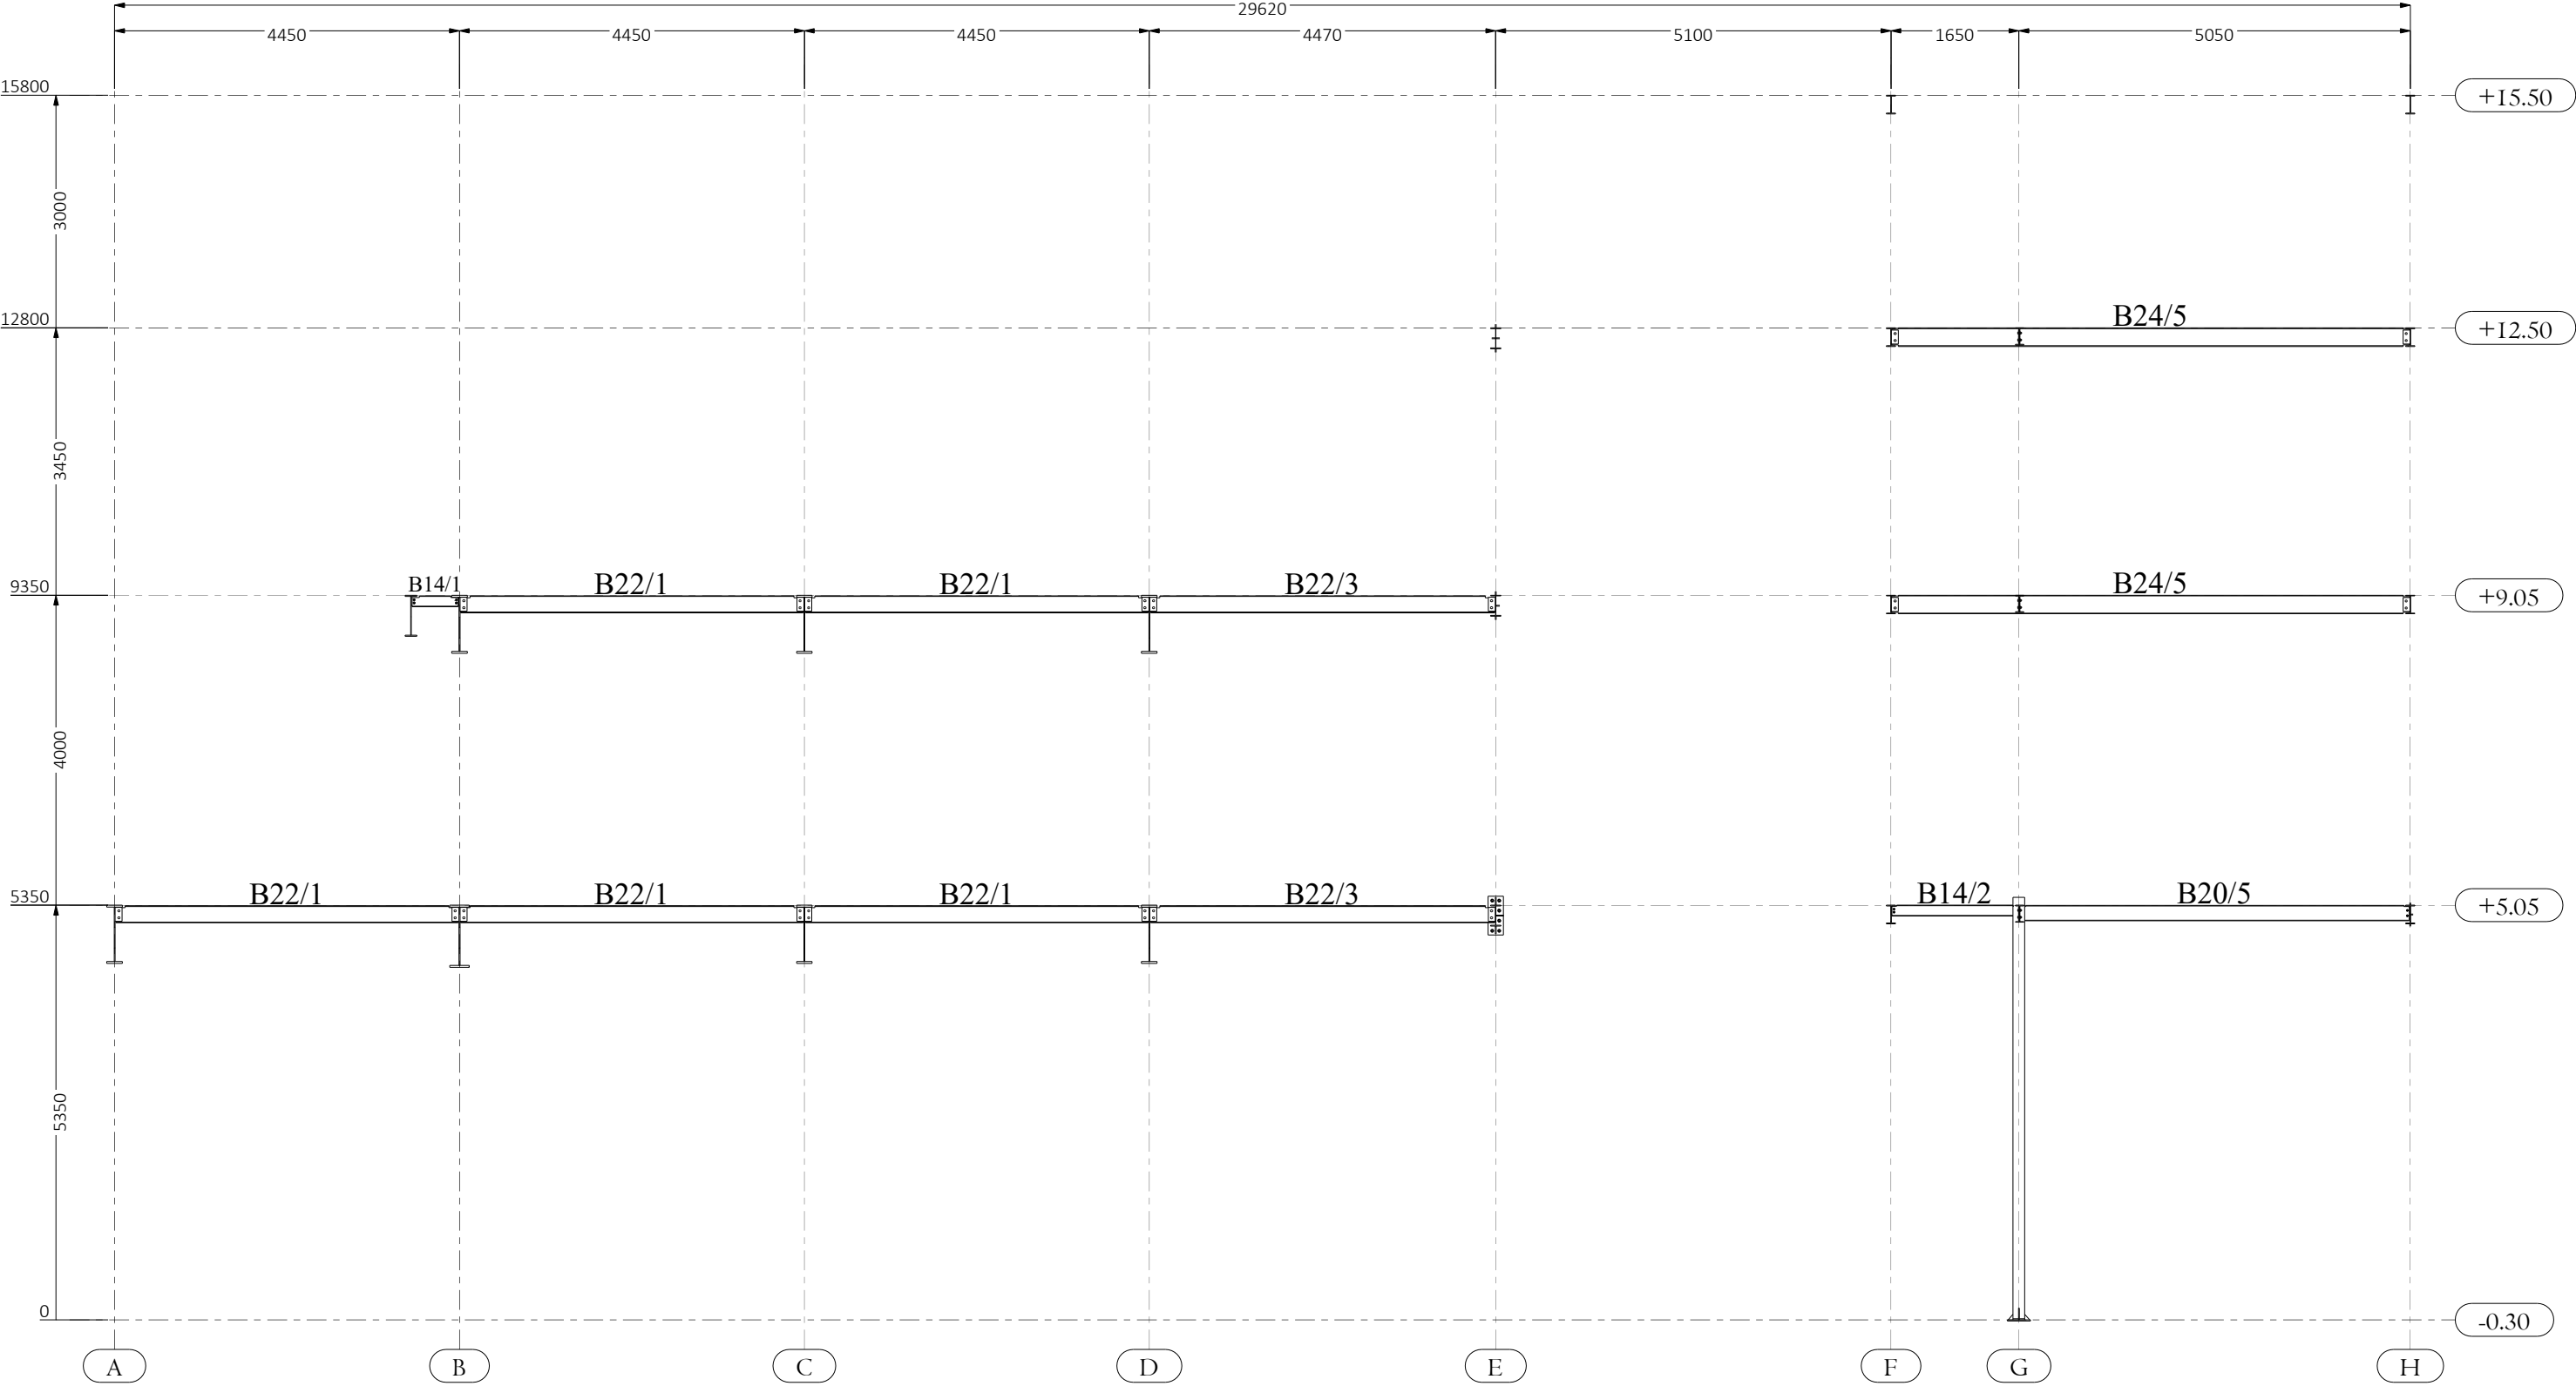


TITLE		Axe 5		
CLIENT				
CONTRACTOR			ISSUED	
MODELLED BY		EN ALMASI	SCALE 1:85	
DRAWING No		[14]	REVISION No. 0	
A3				

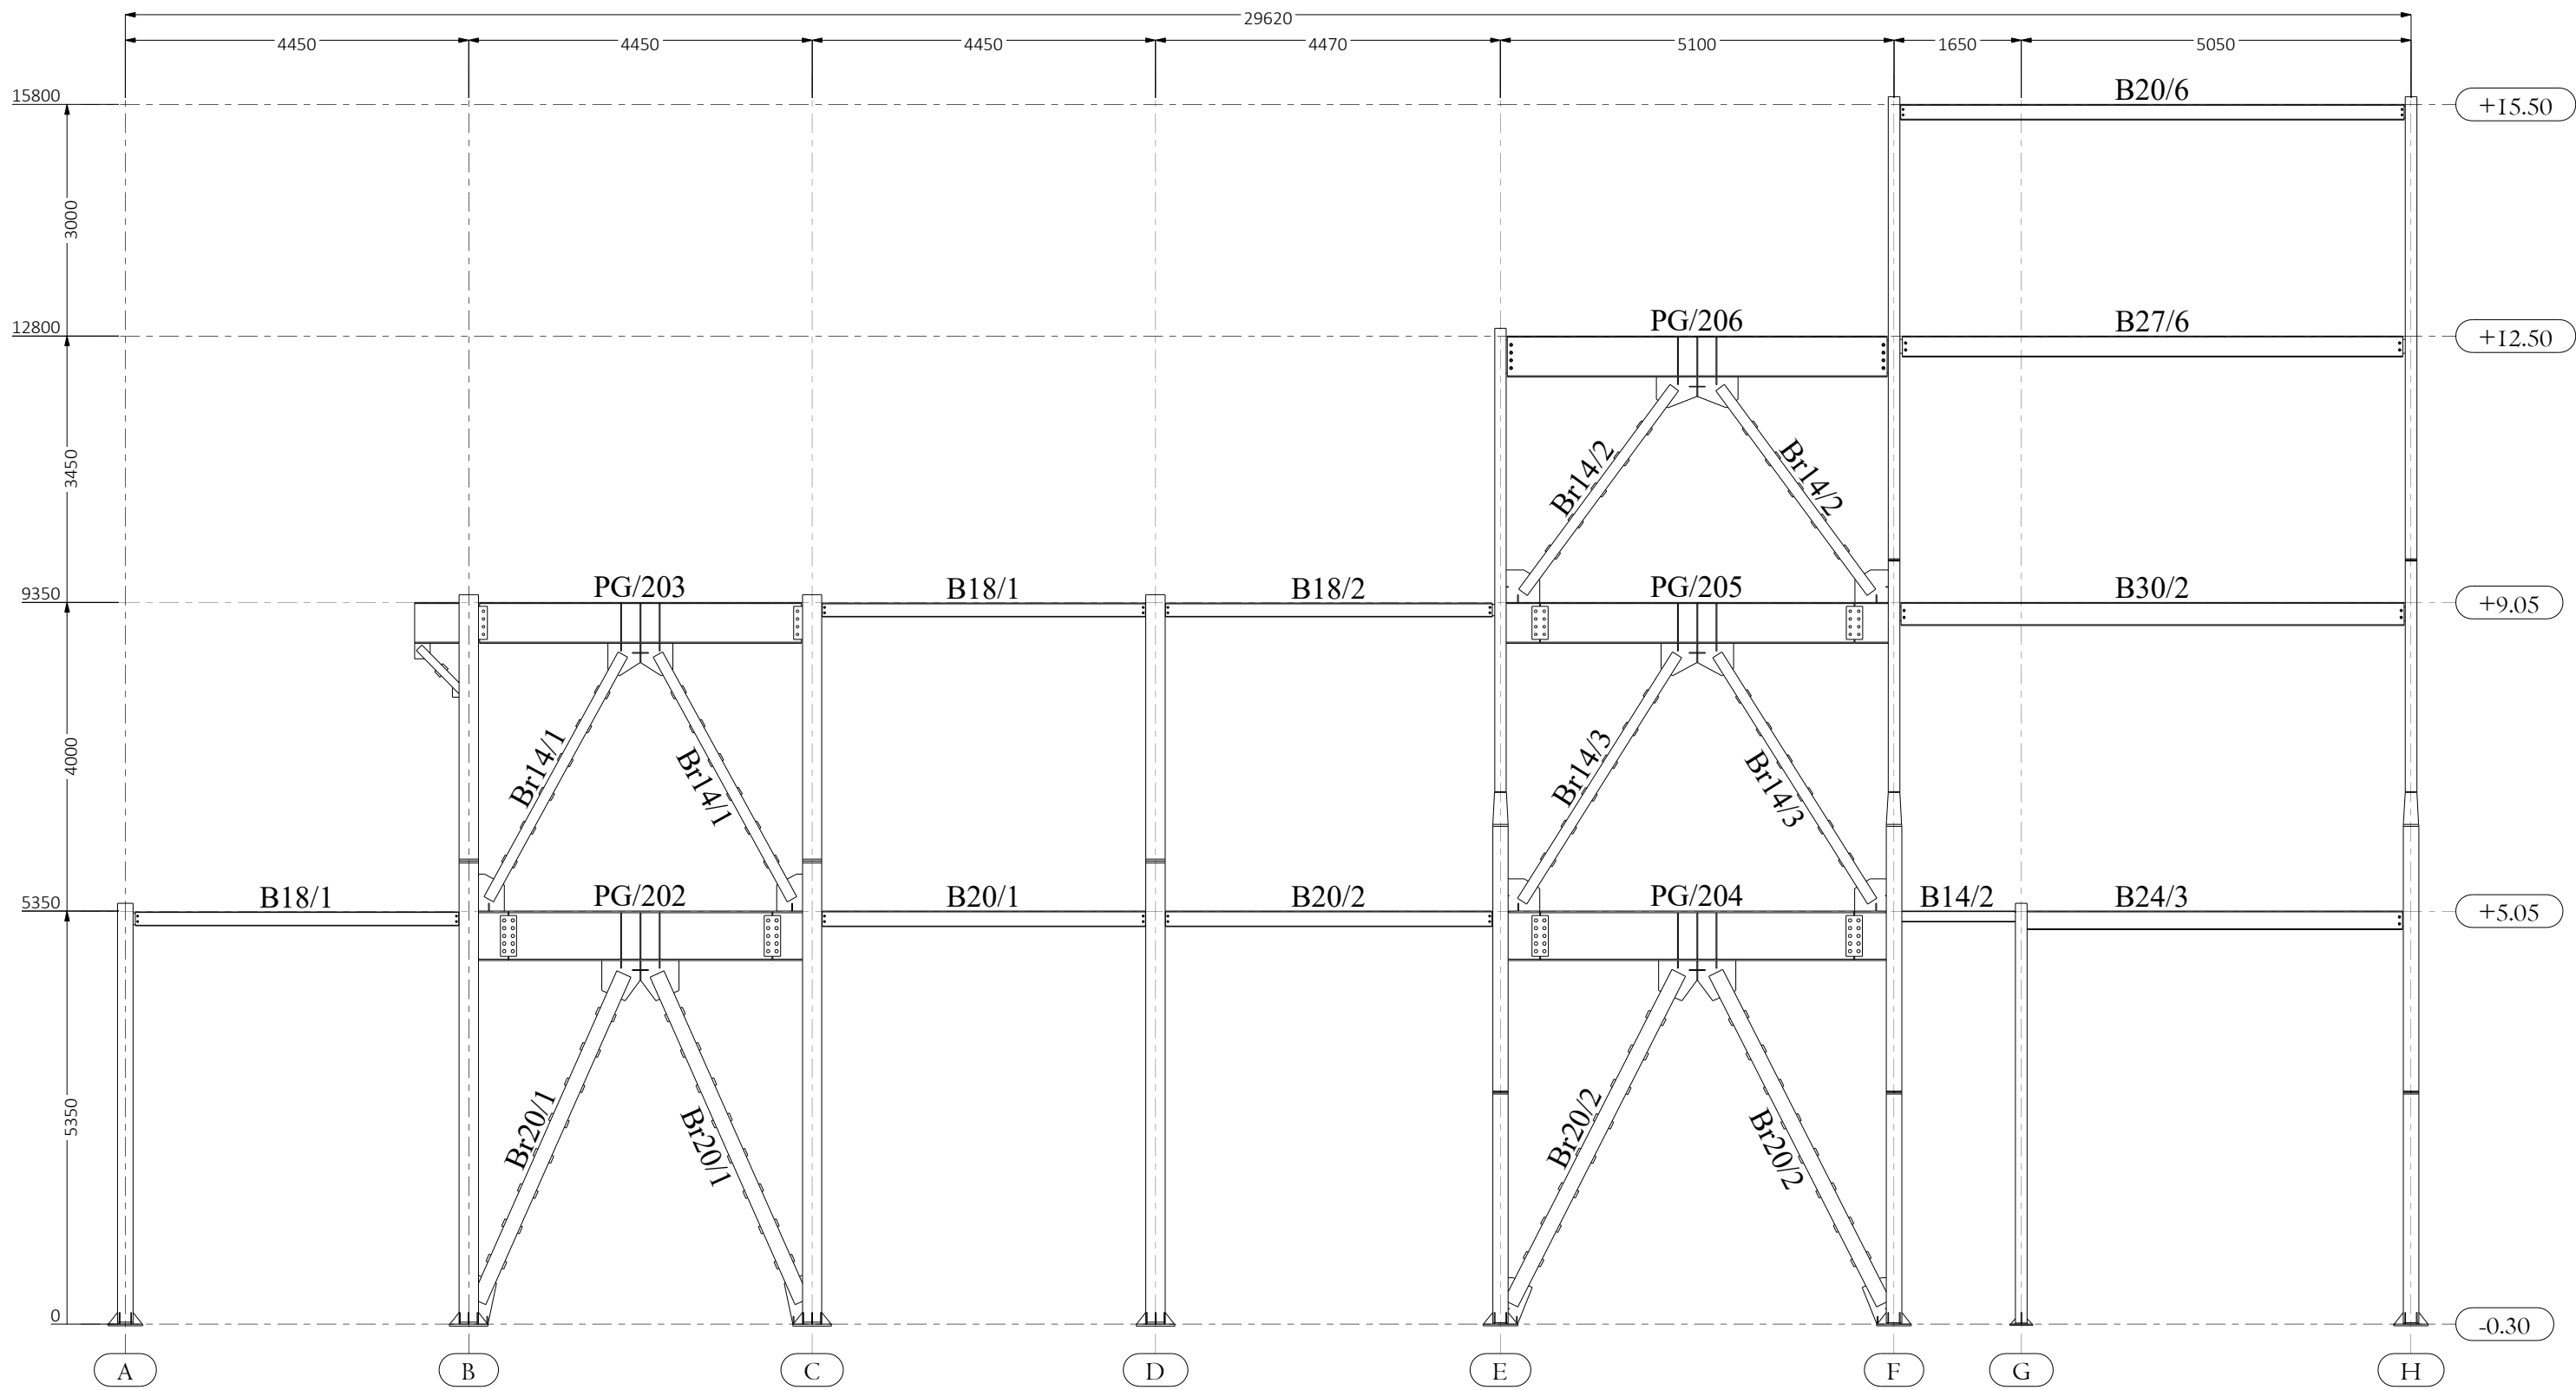


TITLE		Axe 6			
CLIENT					
CONTRACTOR			ISSUED		
MODELLED BY		EN ALMASI	SCALE 1:85		
DRAWING No		[15]	REVISION No.	0	A3




TITLE		EL -0.30		
CLIENT				
CONTRACTOR			ISSUED	
MODELLED BY		EN ALMASI	SCALE 1:85	
DRAWING No		[16]	REVISION No. 0	
A3				

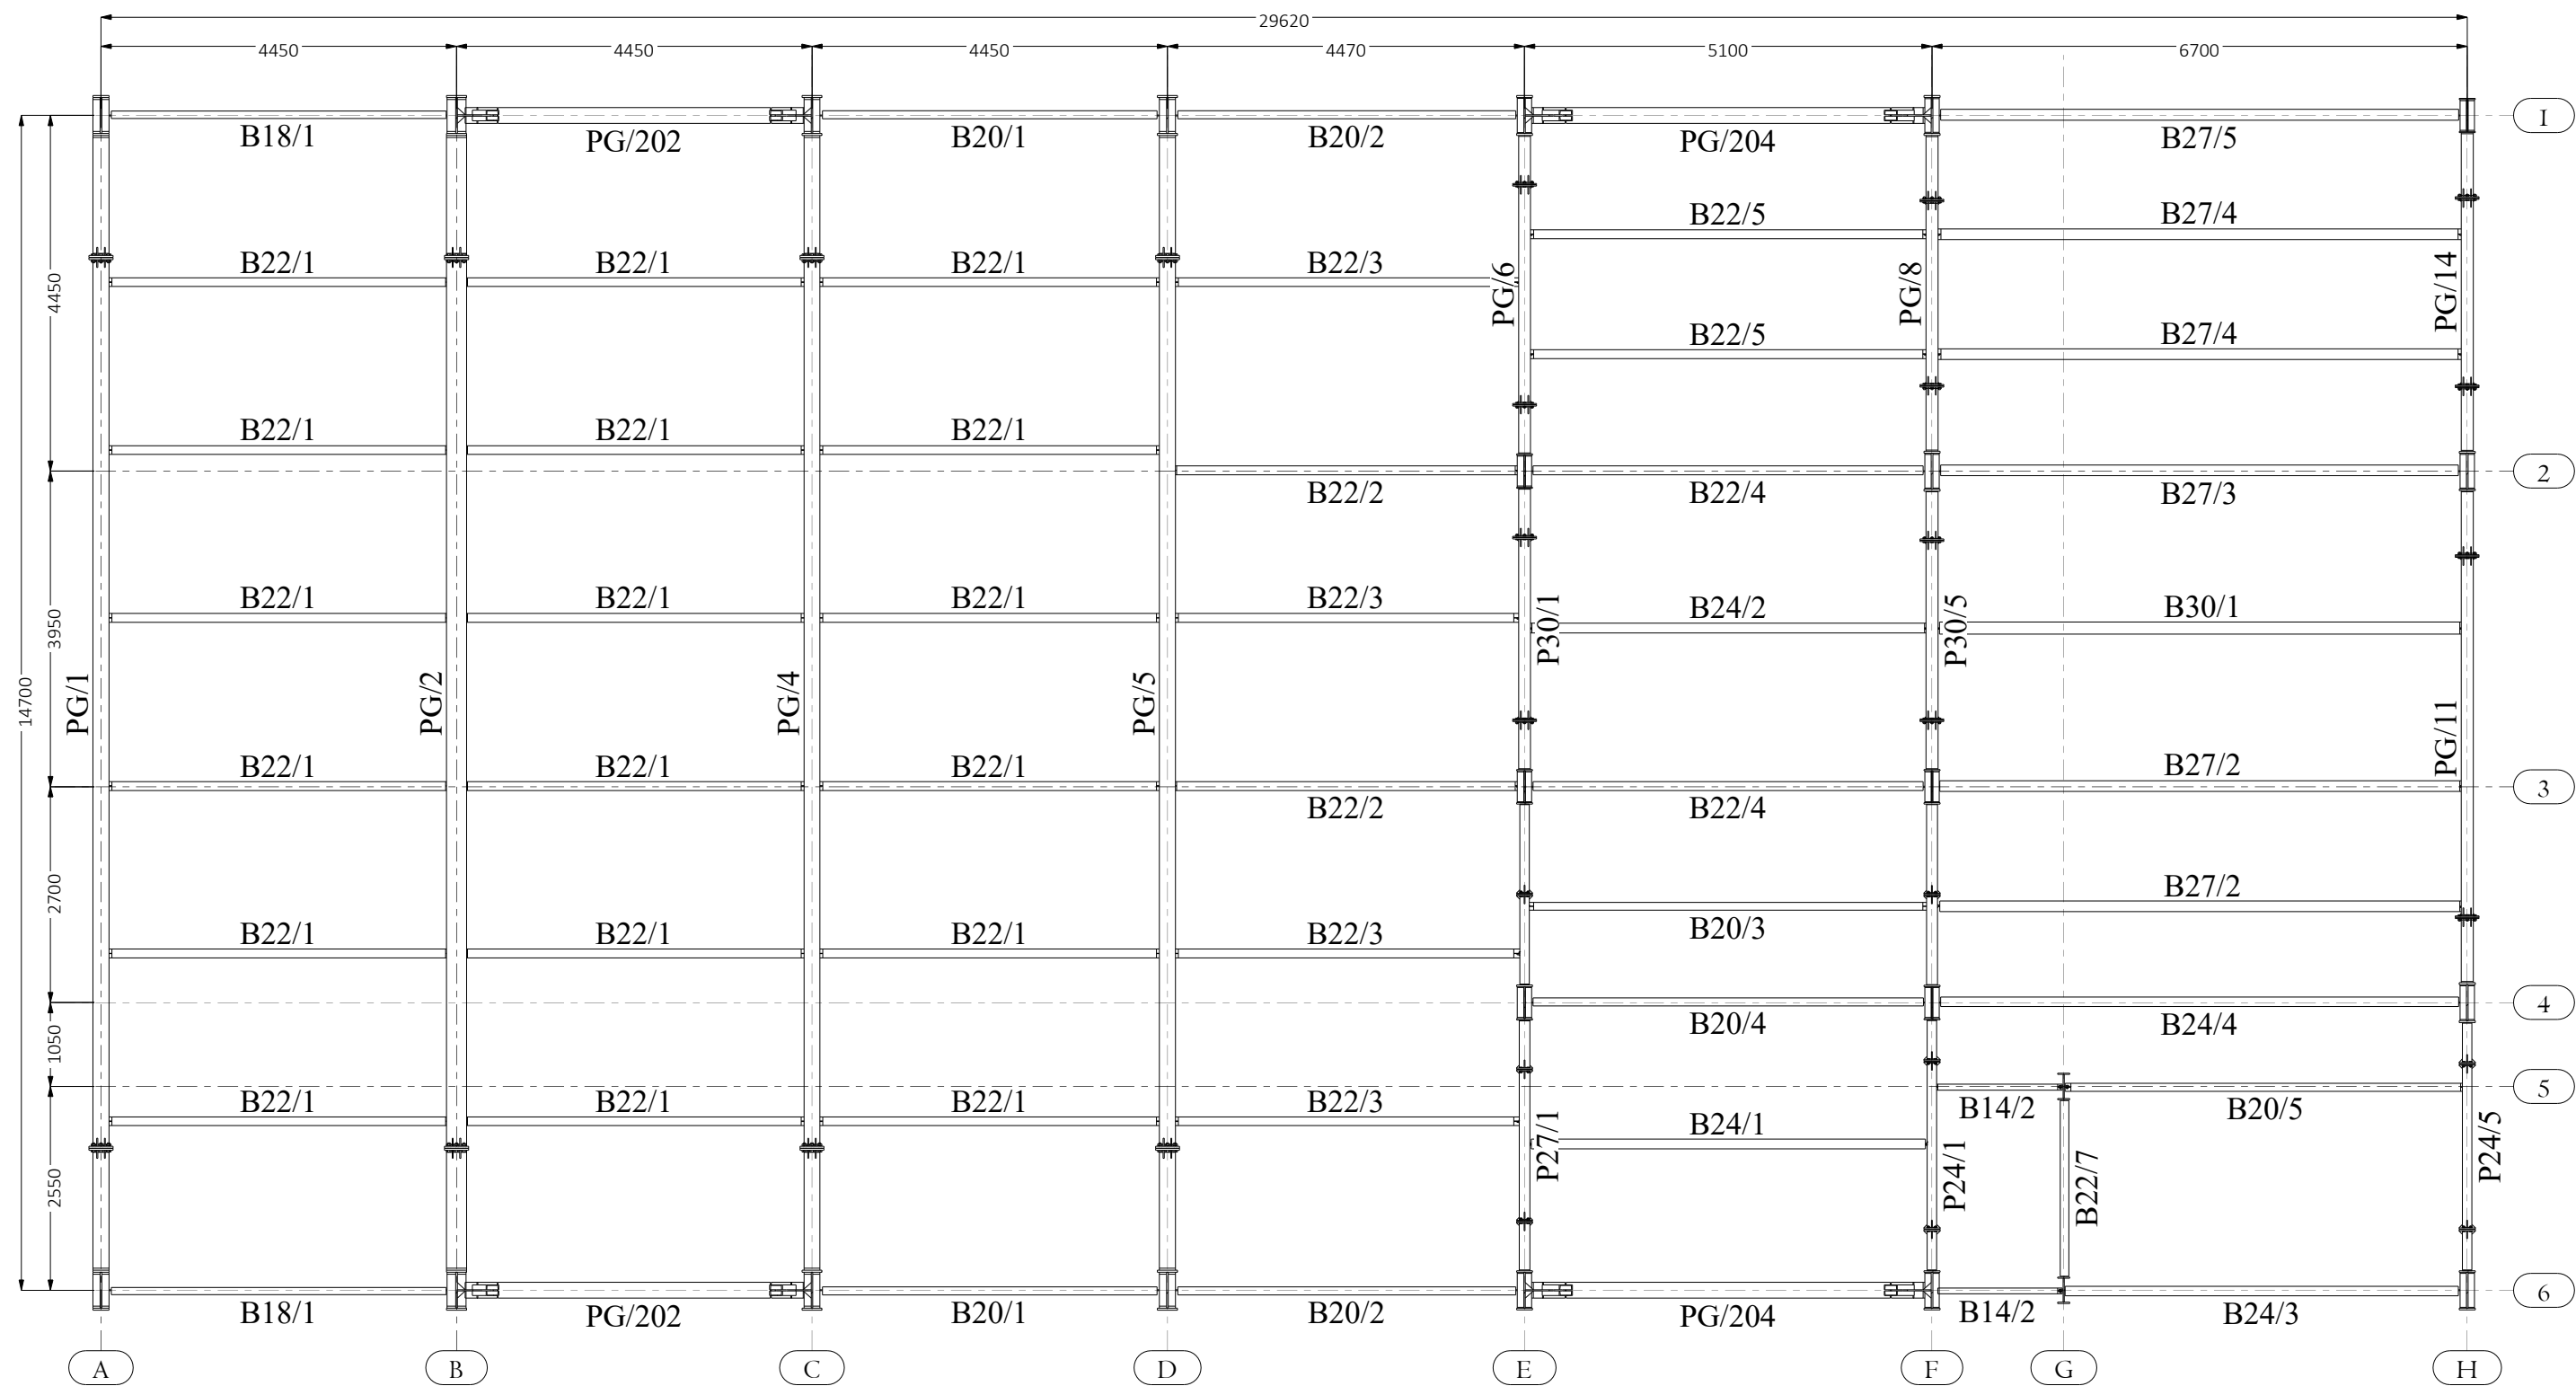


TITLE		EL +5.05		
CLIENT				
CONTRACTOR			ISSUED	
MODELLED BY		EN ALMASI		SCALE 1:85
DRAWING No		[17]		REVISION No. 0
A3				

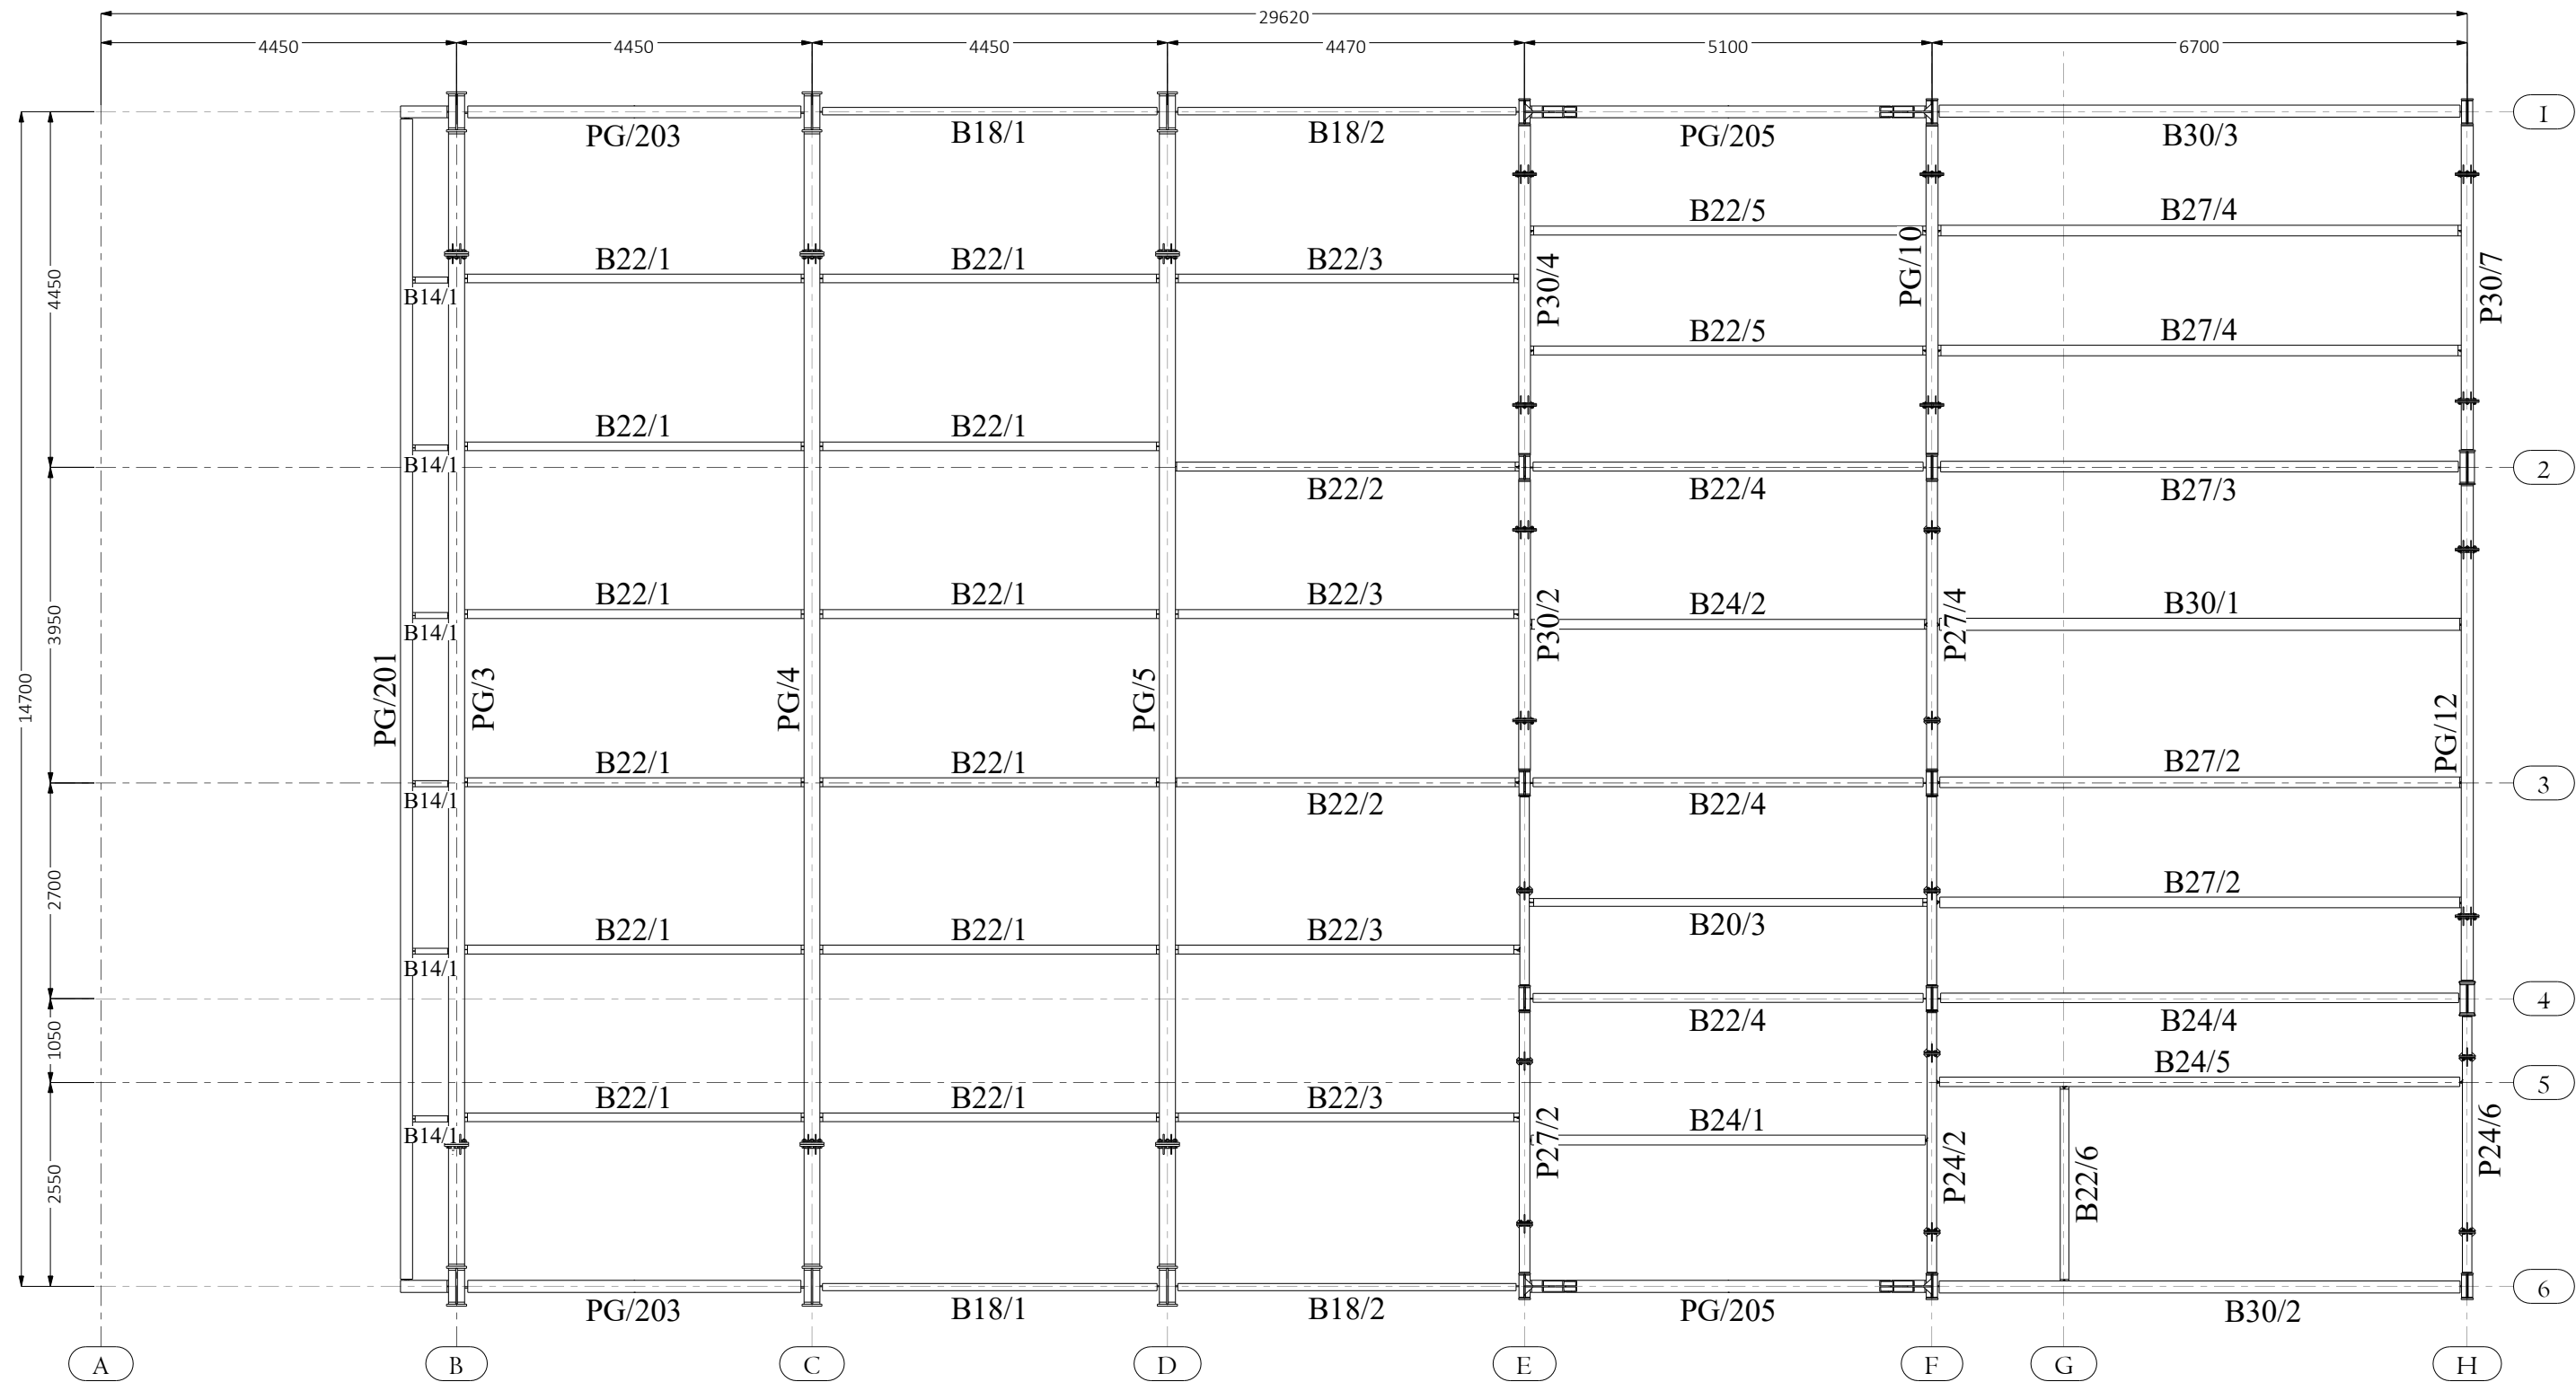


TITLE		EL +9.05			
CLIENT					
CONTRACTOR			ISSUED		
MODELLED BY		EN ALMASI		SCALE 1:85	A3
DRAWING No		[18]		REVISION No. 0	

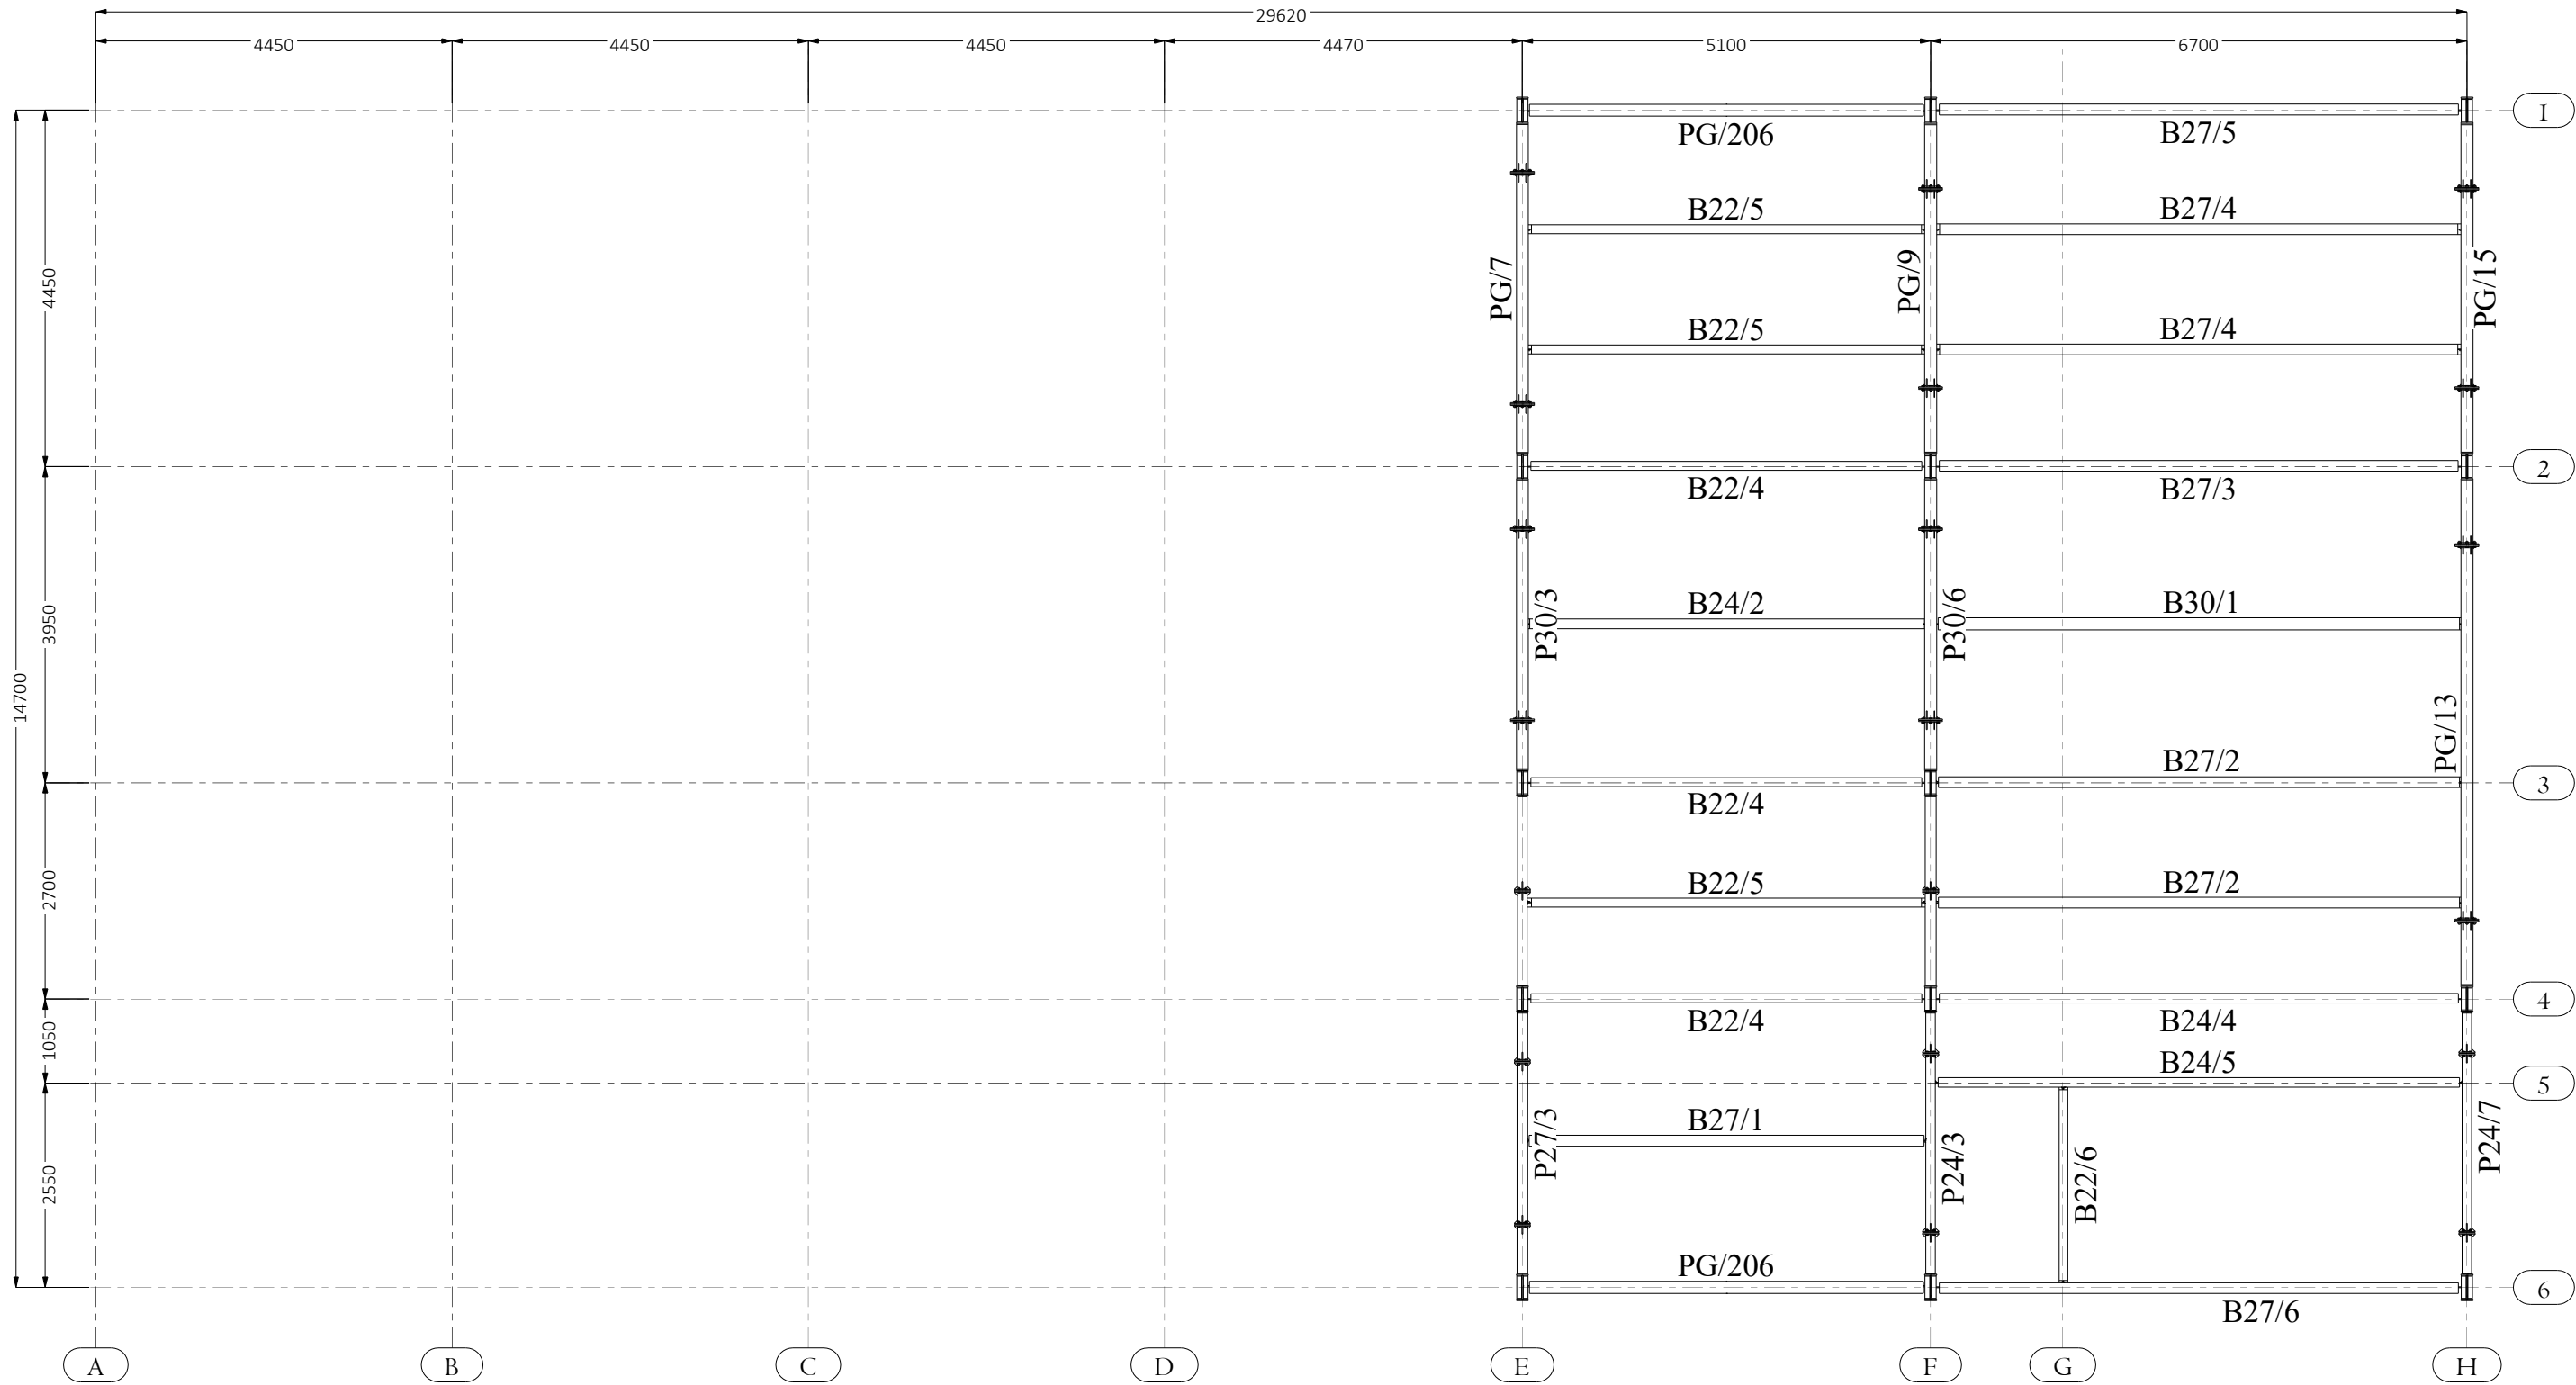


TITLE		EL +12.50		
CLIENT				
CONTRACTOR			ISSUED	
MODELLED BY		EN ALMASI	SCALE 1:85	
DRAWING No		[19]	REVISION No. 0	
A3				

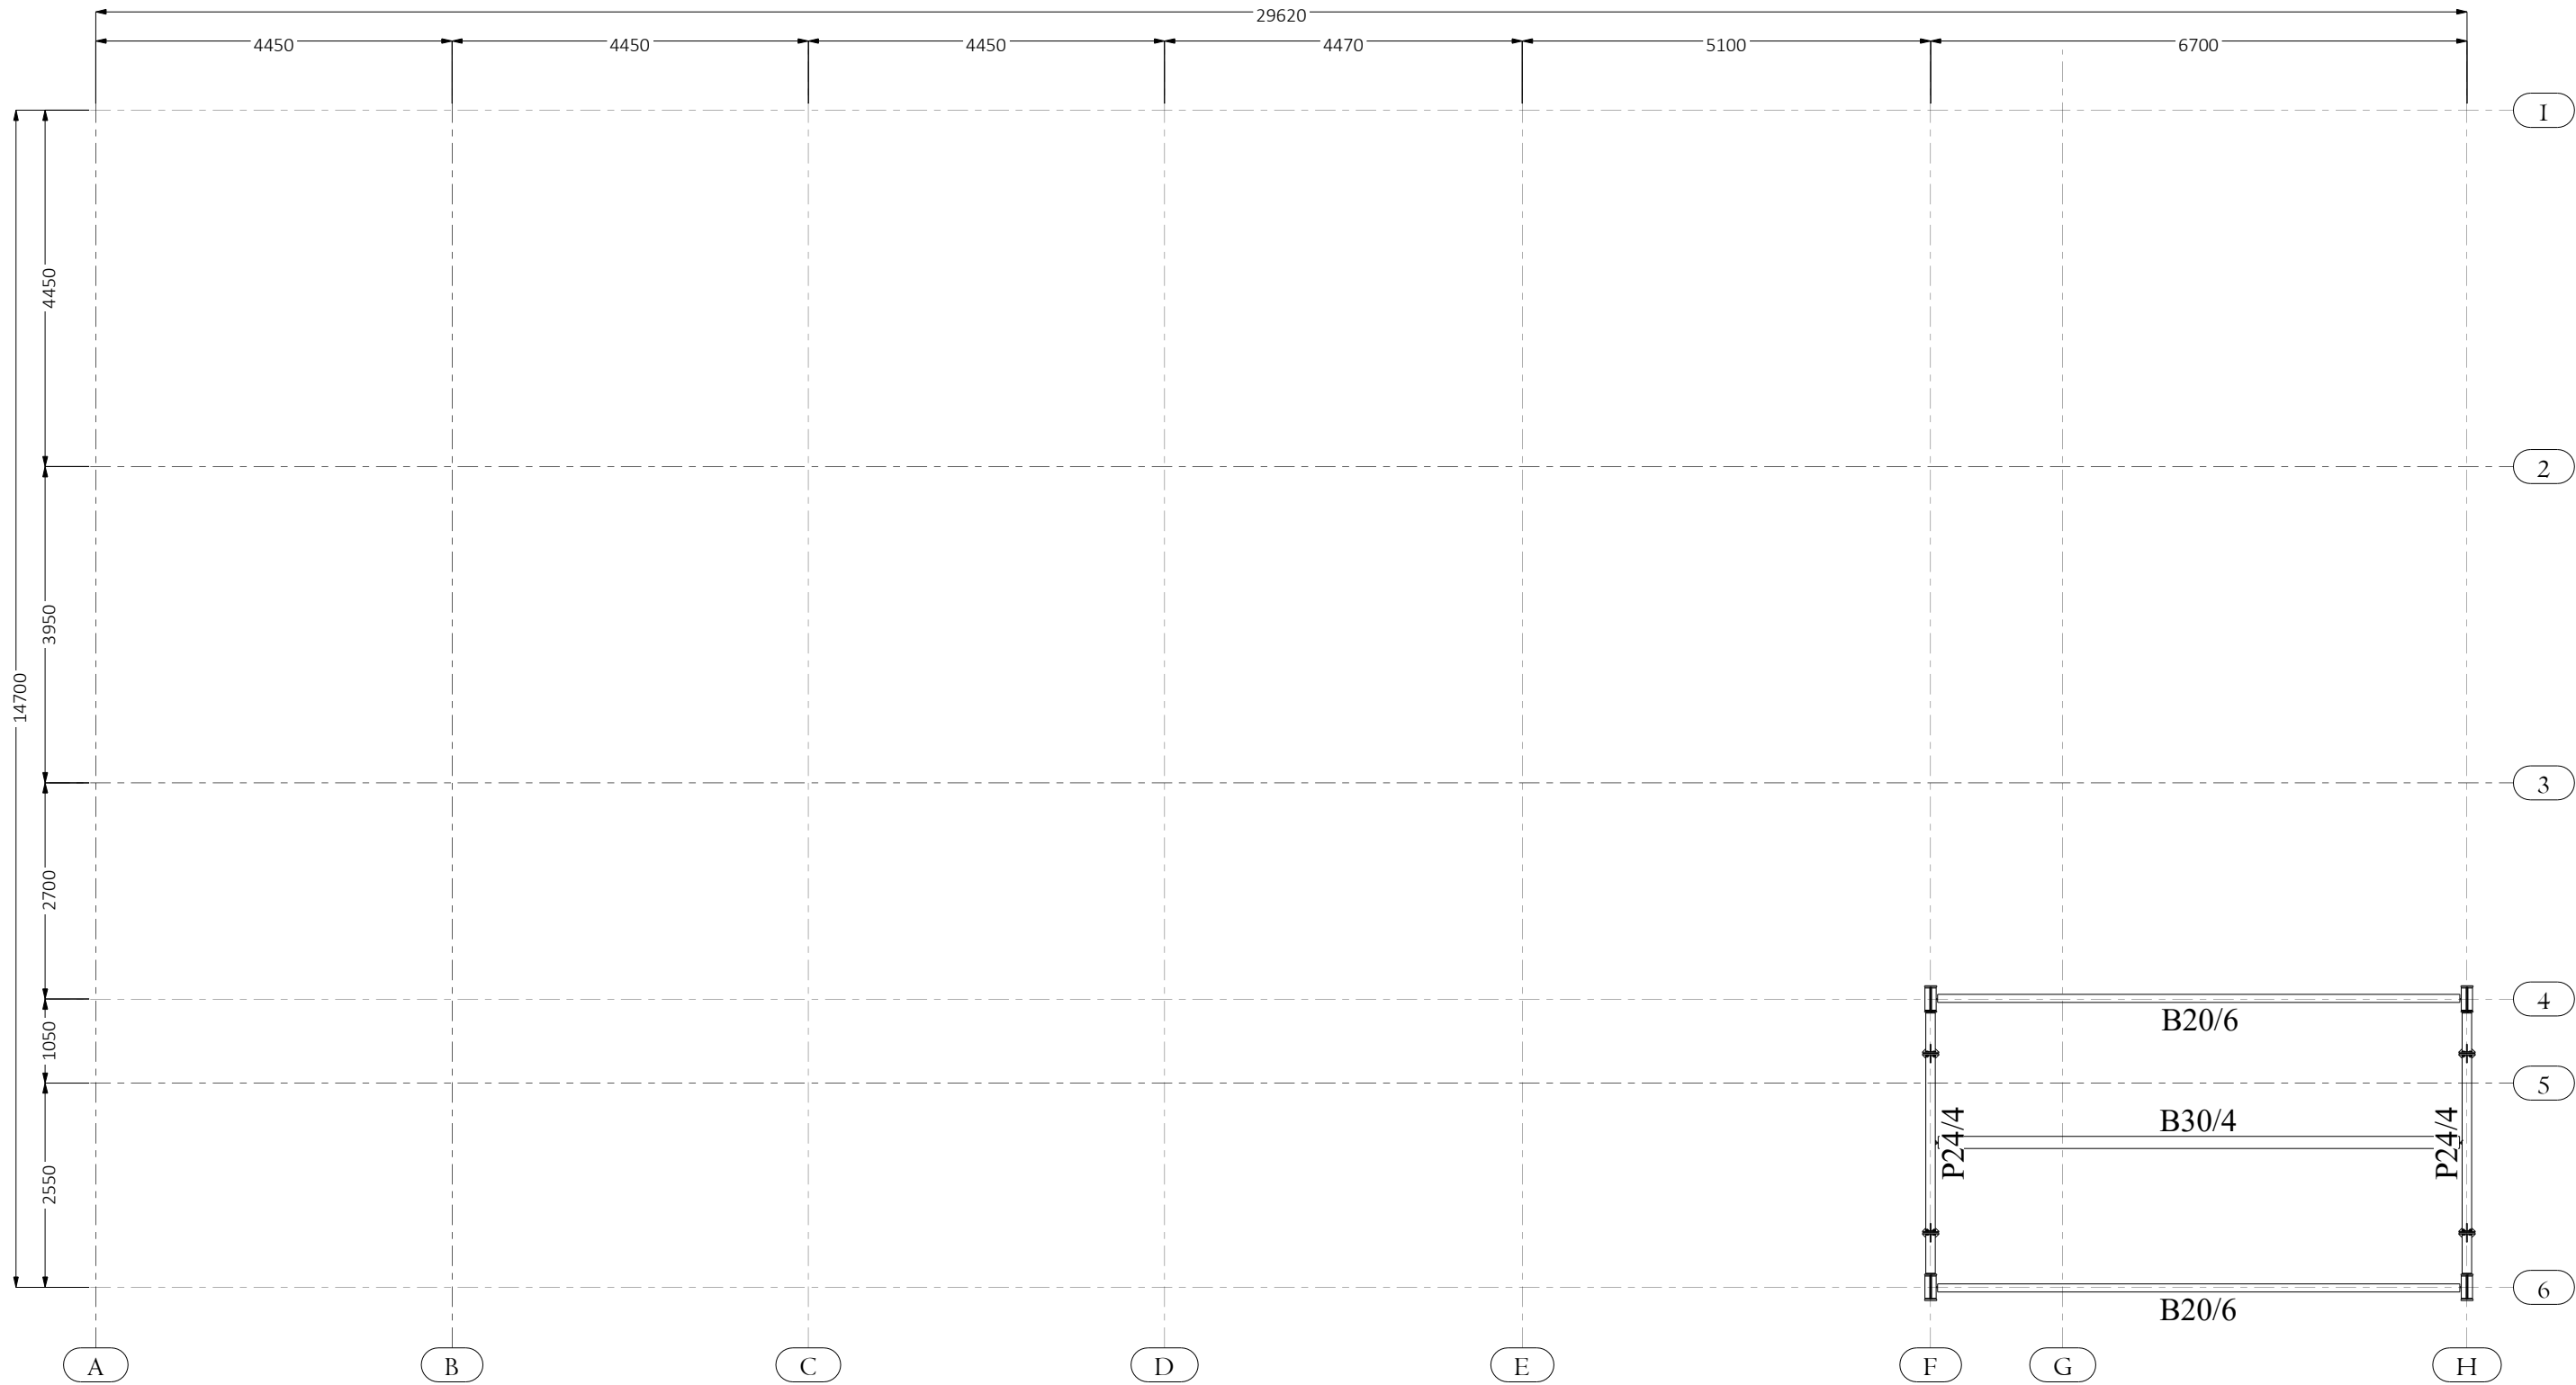


TITLE		EL +15.50		
CLIENT				
CONTRACTOR			ISSUED	
MODELLED BY		EN ALMASI		SCALE 1:85
DRAWING No		[20]		REVISION No. 0
A3				

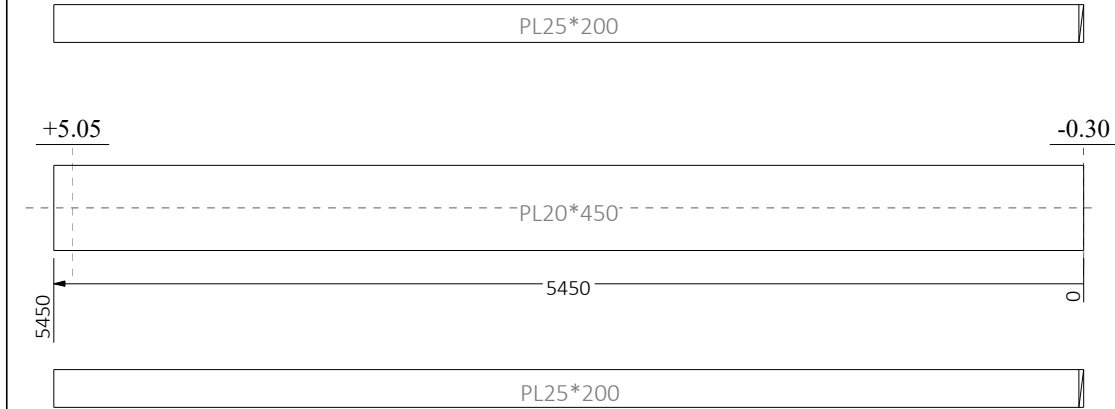


No. 2, Marked C/101

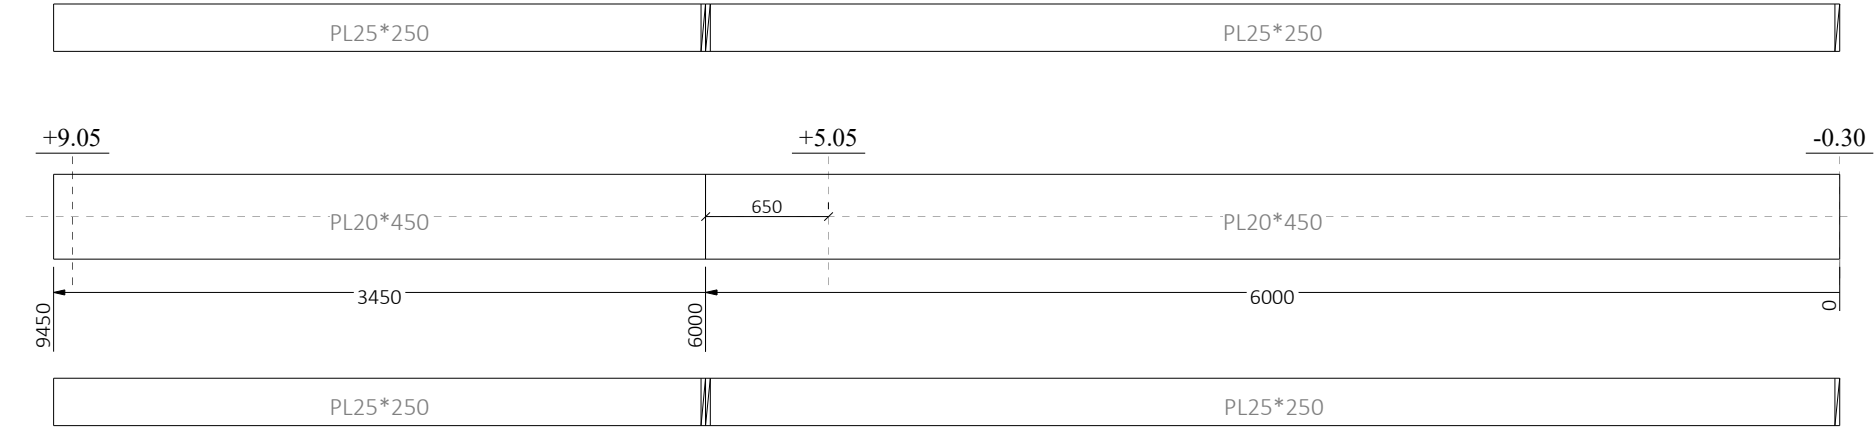

No. 6, Marked C/102

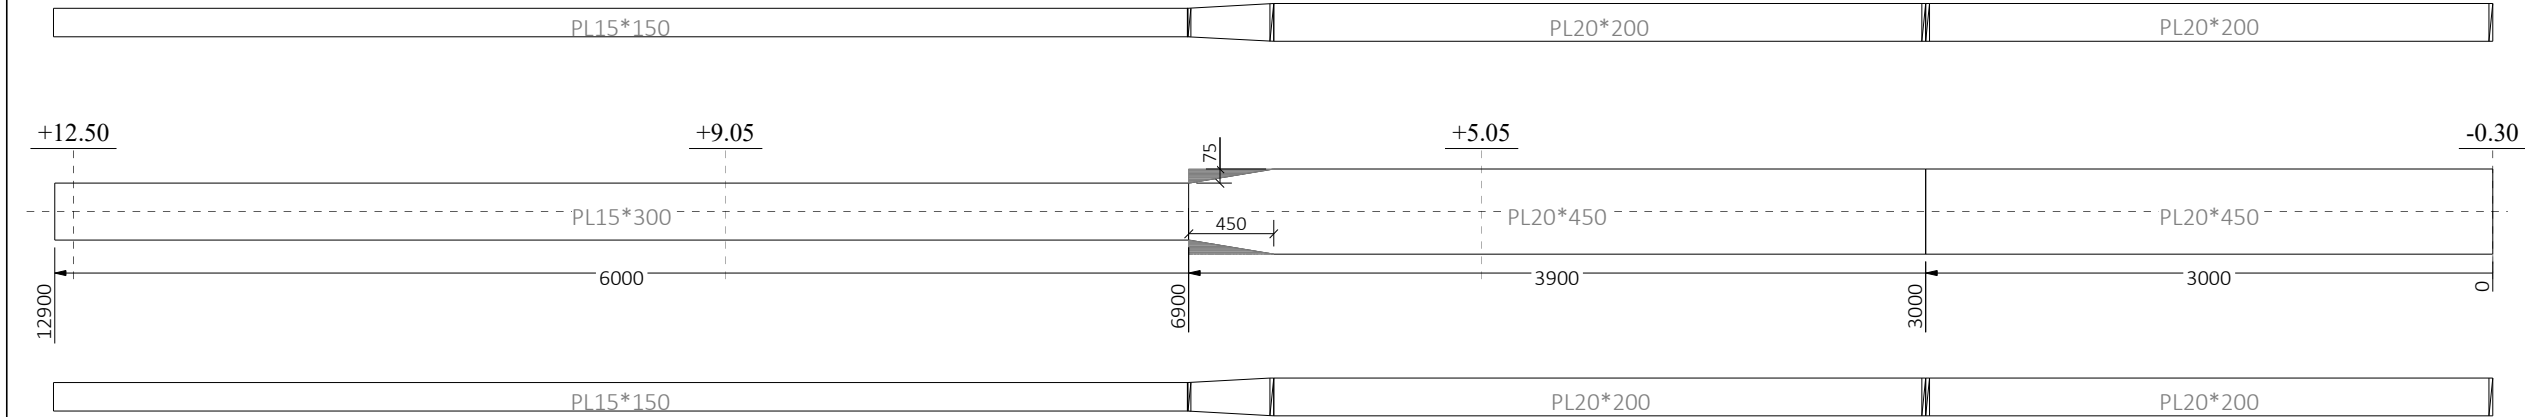

No. 1, Marked C/103



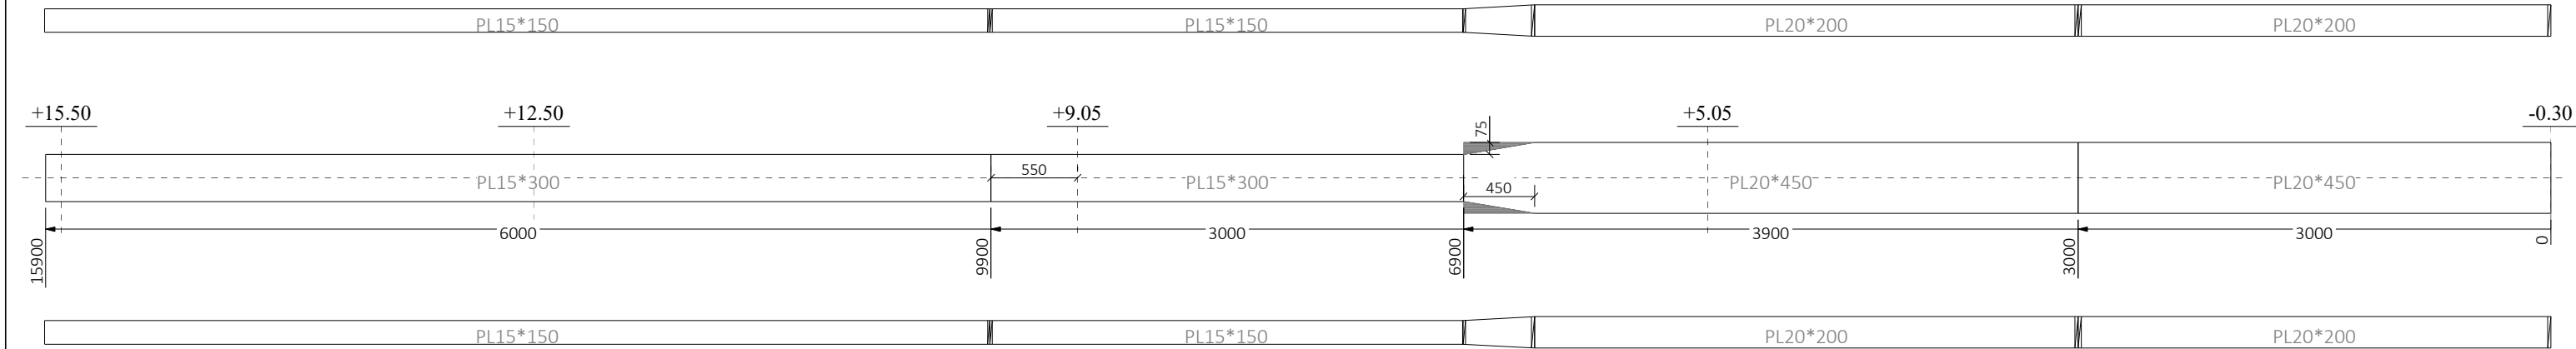


No. 2, Marked C/104

TITLE		مونتاز ستون ا		
CLIENT				
CONTRACTOR		ISSUED 04.03.04		
MODELLED BY	EN ALMASI	SCALE	1:40 1:42	A3
DRAWING No	[1]	REVISION No.	0	

Tekla Structures


MATERIAL LIST FOR C/1 N=1					
Mark	Profile	No.	Length	Area	Weight
1/2PL/1002	PL10*120	4	150	0.0	0.7
1/2PL/1003	PL10*150	4	150	0.0	0.9
1/2PL/1004	PL10*150	4	210	0.0	1.2
BaPL/2	PL20*450	1	800	0.8	56.5
FlgPL-Be/6	PL12*180	1	150	0.1	2.5
Stf/1	PL25*90	4	450	0.1	7.5
Stf/11	PL10*50	2	695	0.1	2.7
WePL/4	PL12*150	1	670	0.2	8.6
C/101	Assembly	1		10.1	811.9
PG/1001	Assembly	1		4.3	277.0
Total				16.3	1203.4

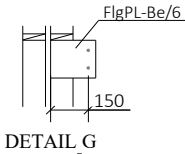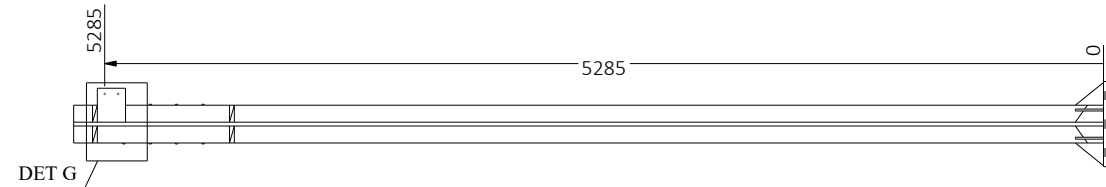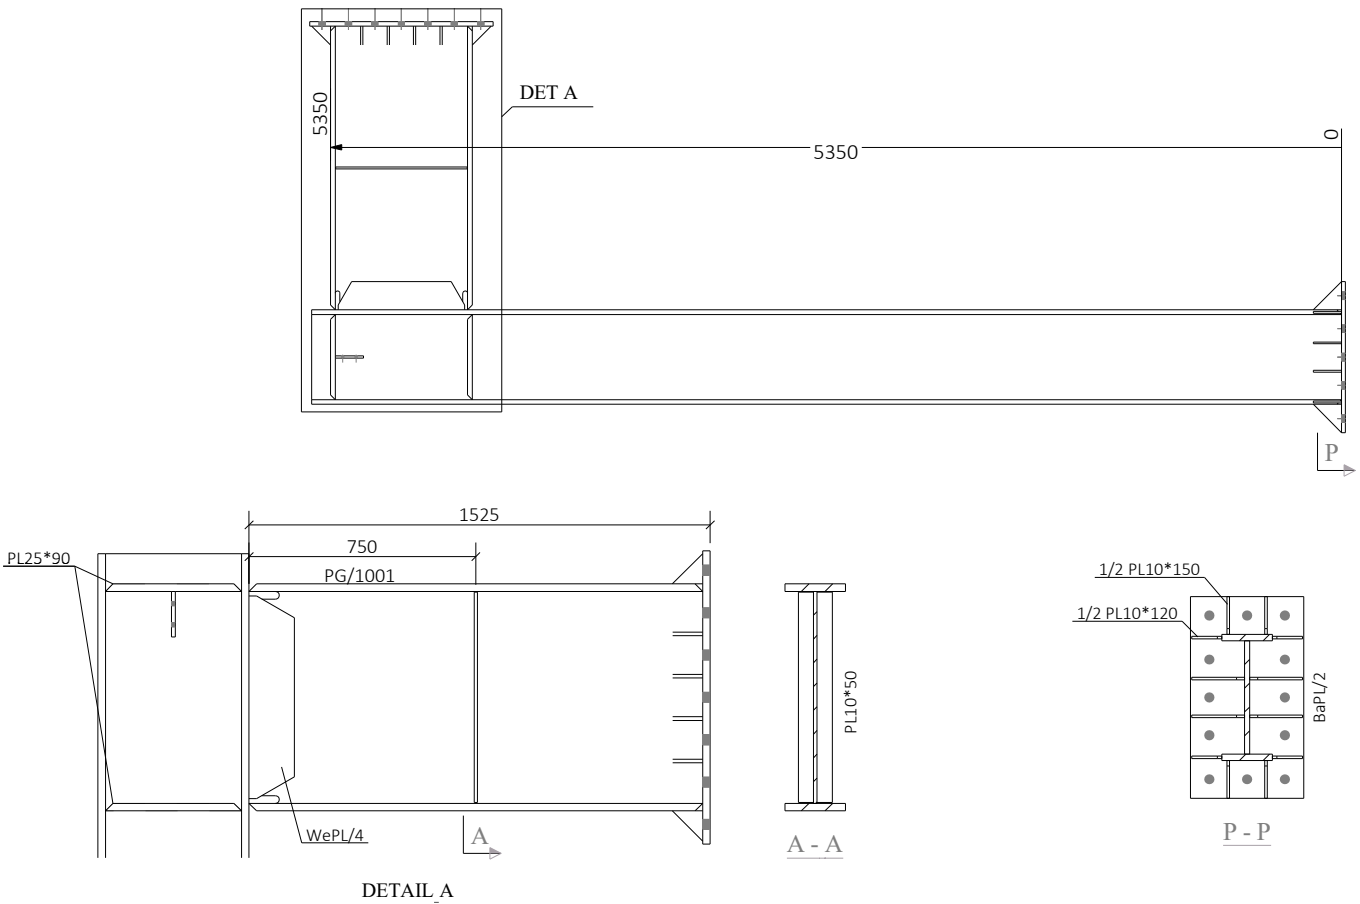

TITLE		ستون تکمیل		
CLIENT				
CONTRACTOR		ISSUED 04.03.		
MODELLED BY	EN ALMASI	SCALE	1:25 1:28	A3
DRAWING No	[C.1]	REVISION No.	0	


Tekla Structures

MATERIAL LIST FOR C/2 N=1					
Mark	Profile	No.	Length	Area	Weight
1/2PL/1002	PL10*120	4	150	0.0	0.7
1/2PL/1003	PL10*150	4	150	0.0	0.9
1/2PL/1004	PL10*150	4	210	0.0	1.2
BaPL/2	PL20*450	1	800	0.8	56.5
FlgPL-Be/6	PL12*180	1	150	0.1	2.5
Stf/1	PL25*90	4	450	0.1	7.5
Stf/11	PL10*50	2	695	0.1	2.7
WePL/4	PL12*150	1	670	0.2	8.6
C/101	Assembly	1		10.1	811.9
PG/1001	Assembly	1		4.3	277.0
Total				16.3	1203.4

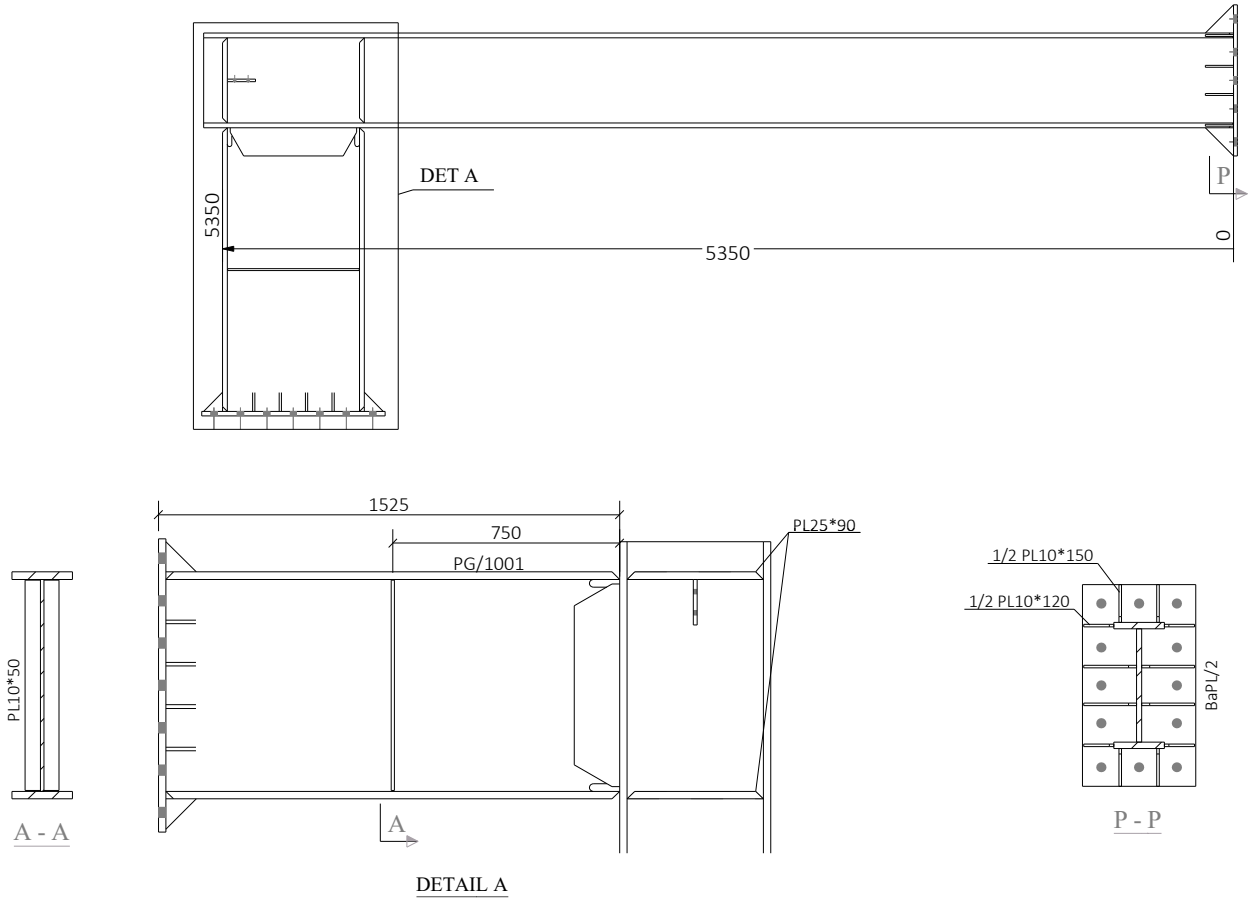


TITLE		ستون تکمیل		
CLIENT				
CONTRACTOR		ISSUED 04.03.		
MODELLED BY	EN ALMASI	SCALE 1:25	1:28	A3
DRAWING No	[C.2]	REVISION No. 0		

MATERIAL LIST FOR C/3 N=1					
Mark	Profile	No.	Length	Area	Weight
1/2PL/1002	PL10*120	4	150	0.0	0.7
1/2PL/1003	PL10*150	6	150	0.0	0.9
1/2PL/1005	PL10*150	4	230	0.0	1.4
1/2PL/1011	PL10*90	8	100	0.0	0.4
BaPL/11	PL25*500	1	800	0.9	78.5
FlgPL-Be/3	PL15*230	1	430	0.2	11.6
FlgPL-Be/5	PL15*110	1	430	0.1	5.6
FlgPL-Be/6	PL12*180	1	150	0.1	2.5
GusPL/1	PL15*350	1	630	0.4	21.2
GusPL/5	PL15*450	1	480	0.4	23.3
GusPL/8	PL15*200	2	200	0.1	4.4
Stf/1	PL25*90	6	450	0.1	7.5
Stf/2	PL25*110	2	450	0.1	9.2
Stf/11	PL10*50	2	695	0.1	2.7
Stf/12	PL10*50	2	745	0.1	2.9
WePL/4	PL12*150	1	670	0.2	8.6
WePL/5	PL12*150	1	720	0.2	9.3
Br10/1	Assembly	1		0.6	18.9
C/102	Assembly	1	19.3	1591.2	
PG/1001	Assembly	1	4.3	277.0	
PG/1002	Assembly	1	4.8	316.7	
PG/2001	Assembly	1	1.1	44.1	
PG/2002	Assembly	1	1.0	56.5	
Total				35.7	2564.9

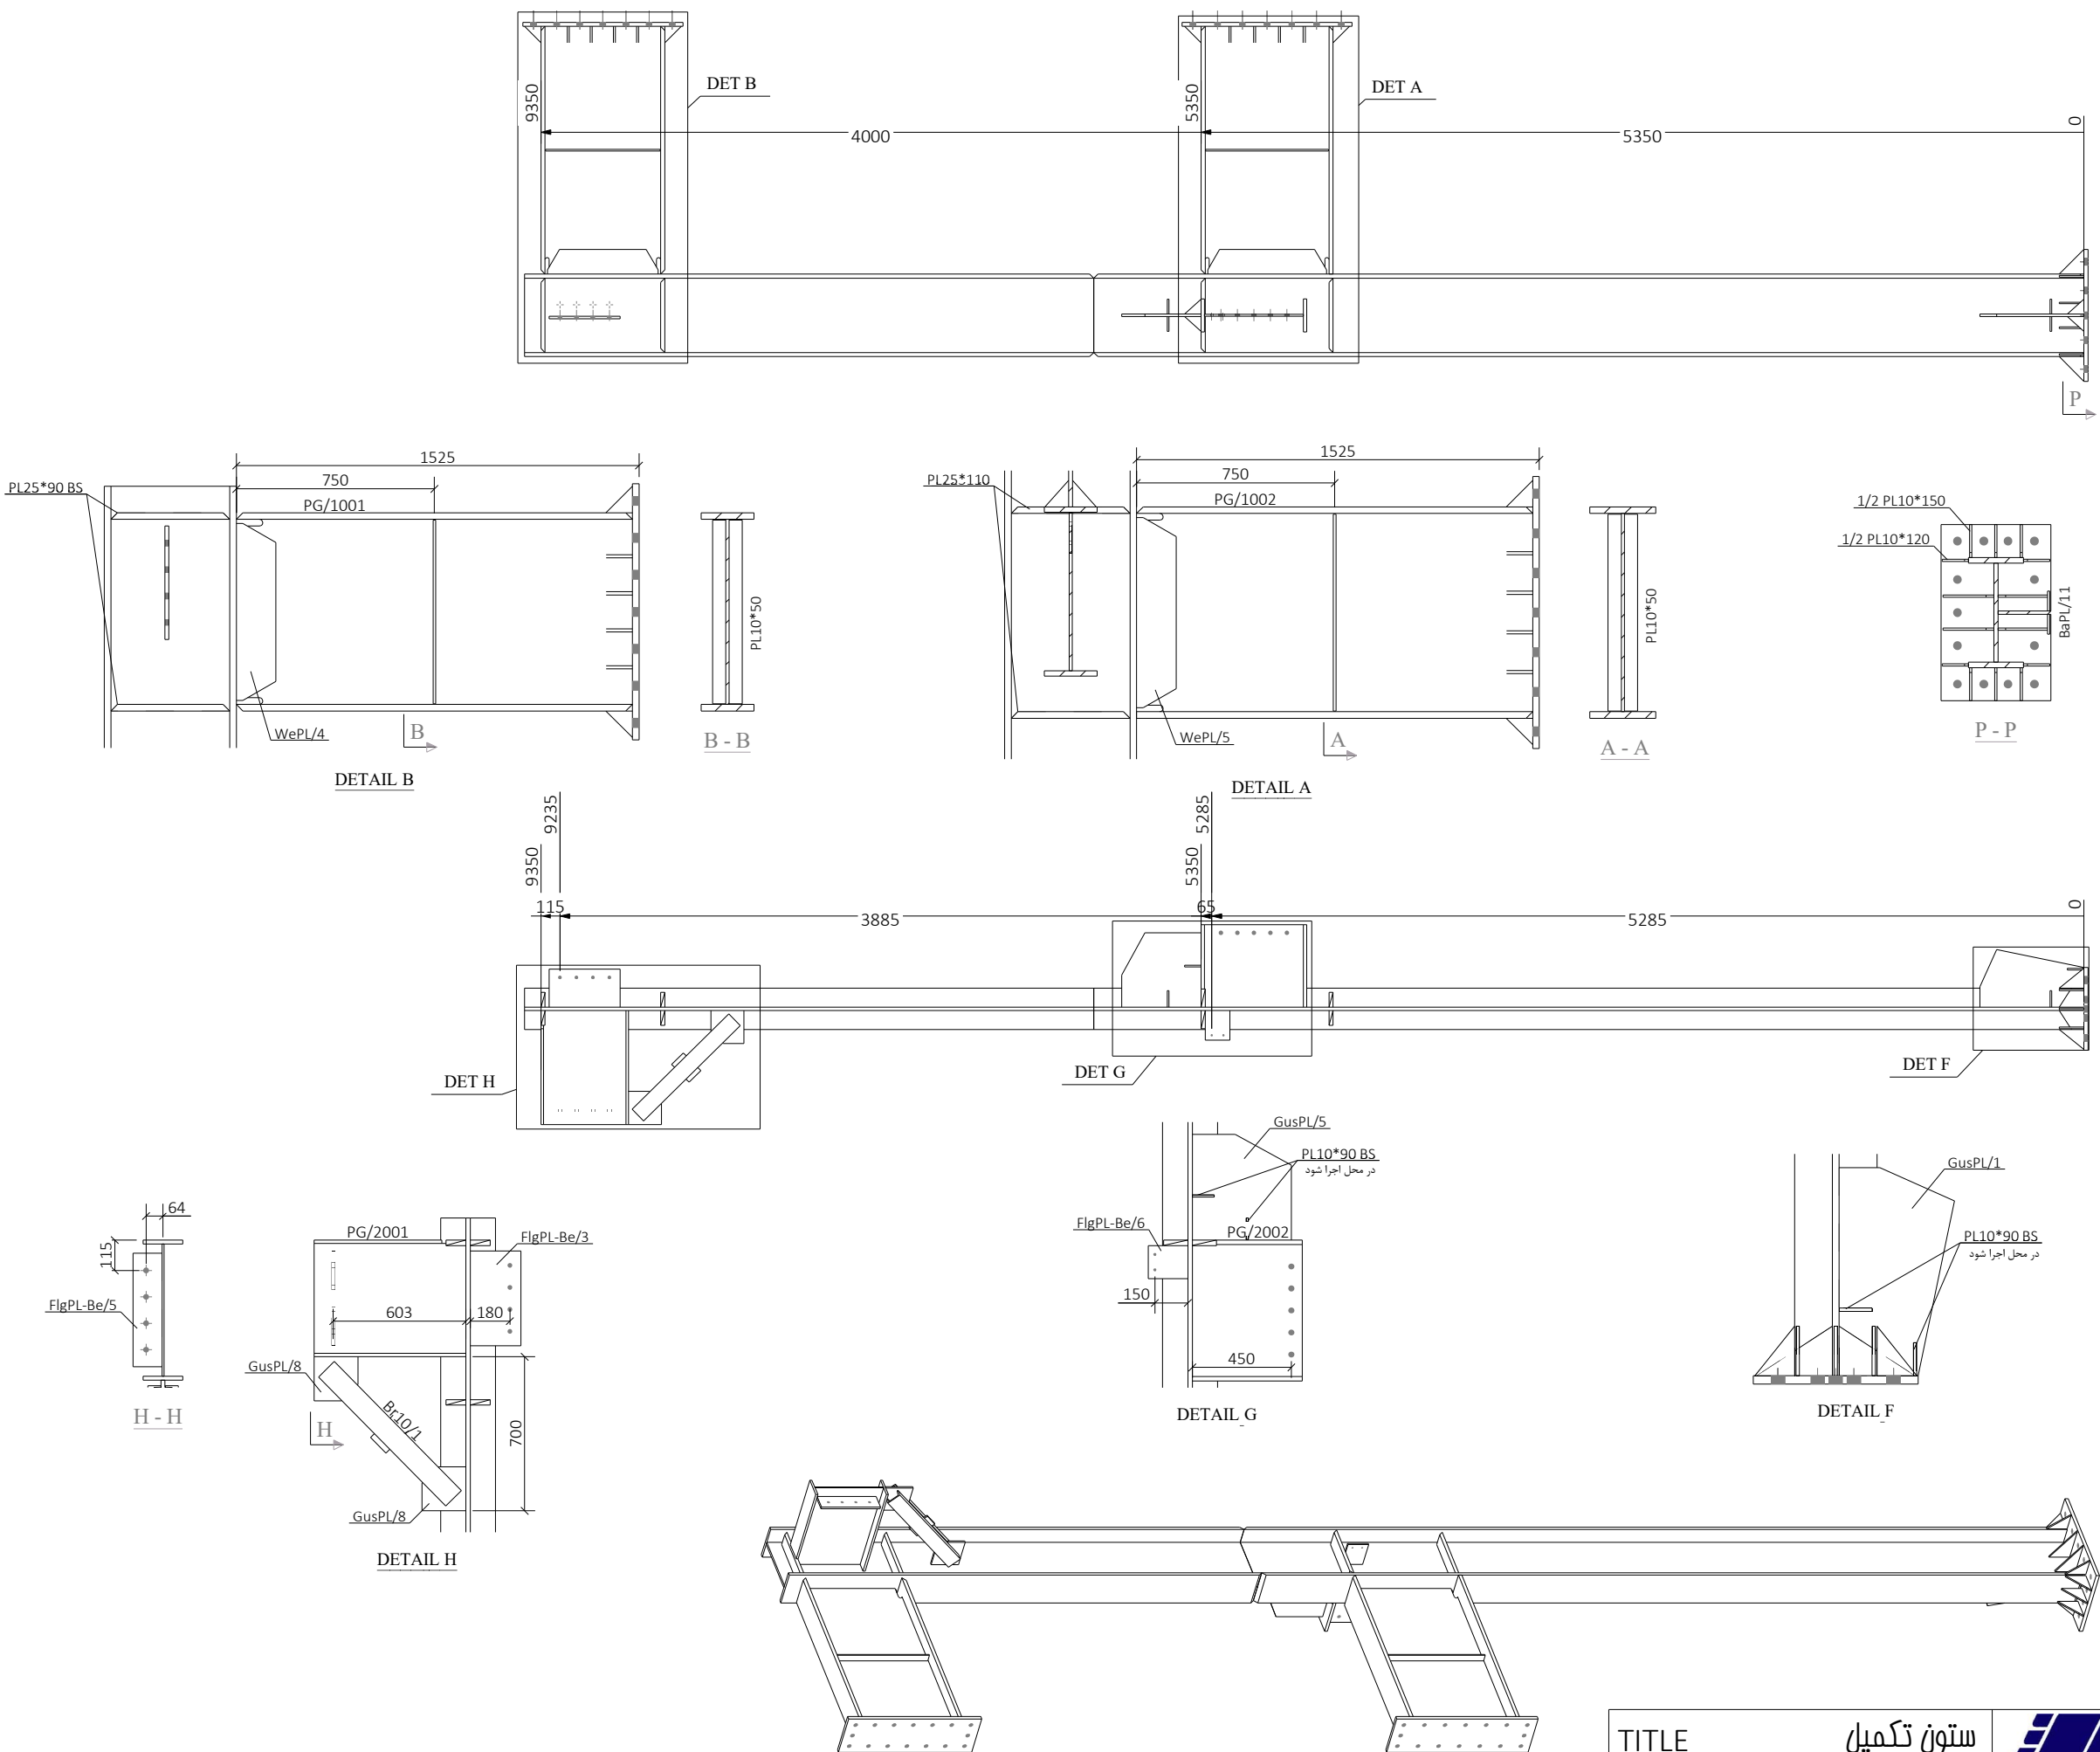

TITLE		ستون تکمیل		
CLIENT				
CONTRACTOR		ISSUED 04.03.		
MODELLED BY	EN ALMASI	SCALE	1:20 1:25	A3
DRAWING No	[C.3]	REVISION No.	0	


MATERIAL LIST FOR C/4 N=1					
Mark	Profile	No.	Length	Area	Weight
1/2PL/1002	PL10*120	4	150	0.0	0.7
1/2PL/1003	PL10*150	6	150	0.0	0.9
1/2PL/1005	PL10*150	4	230	0.0	1.4
1/2PL/1011	PL10*90	8	100	0.0	0.4
BaPL/11	PL25*500	1	800	0.9	78.5
FlgPL-Be/3	PL15*230	1	430	0.2	11.6
FlgPL-Be/5	PL15*110	1	430	0.1	5.6
FlgPL-Be/6	PL12*180	1	150	0.1	2.5
GusPL/1	PL15*350	1	630	0.4	21.2
GusPL/5	PL15*450	1	480	0.4	23.3
GusPL/8	PL15*200	2	200	0.1	4.4
Stf/1	PL25*90	6	450	0.1	7.5
Stf/2	PL25*110	2	450	0.1	9.2
Stf/11	PL10*50	2	695	0.1	2.7
Stf/12	PL10*50	2	745	0.1	2.9
WePL/4	PL12*150	1	670	0.2	8.6
WePL/5	PL12*150	1	720	0.2	9.3
Br10/1	Assembly	1		0.6	18.9
C/102	Assembly	1	19.3	1591.2	
PG/1001	Assembly	1	4.3	277.0	
PG/1002	Assembly	1	4.8	316.7	
PG/2001	Assembly	1	1.1	44.1	
PG/2002	Assembly	1	1.0	56.5	
Total			35.7	2564.9	

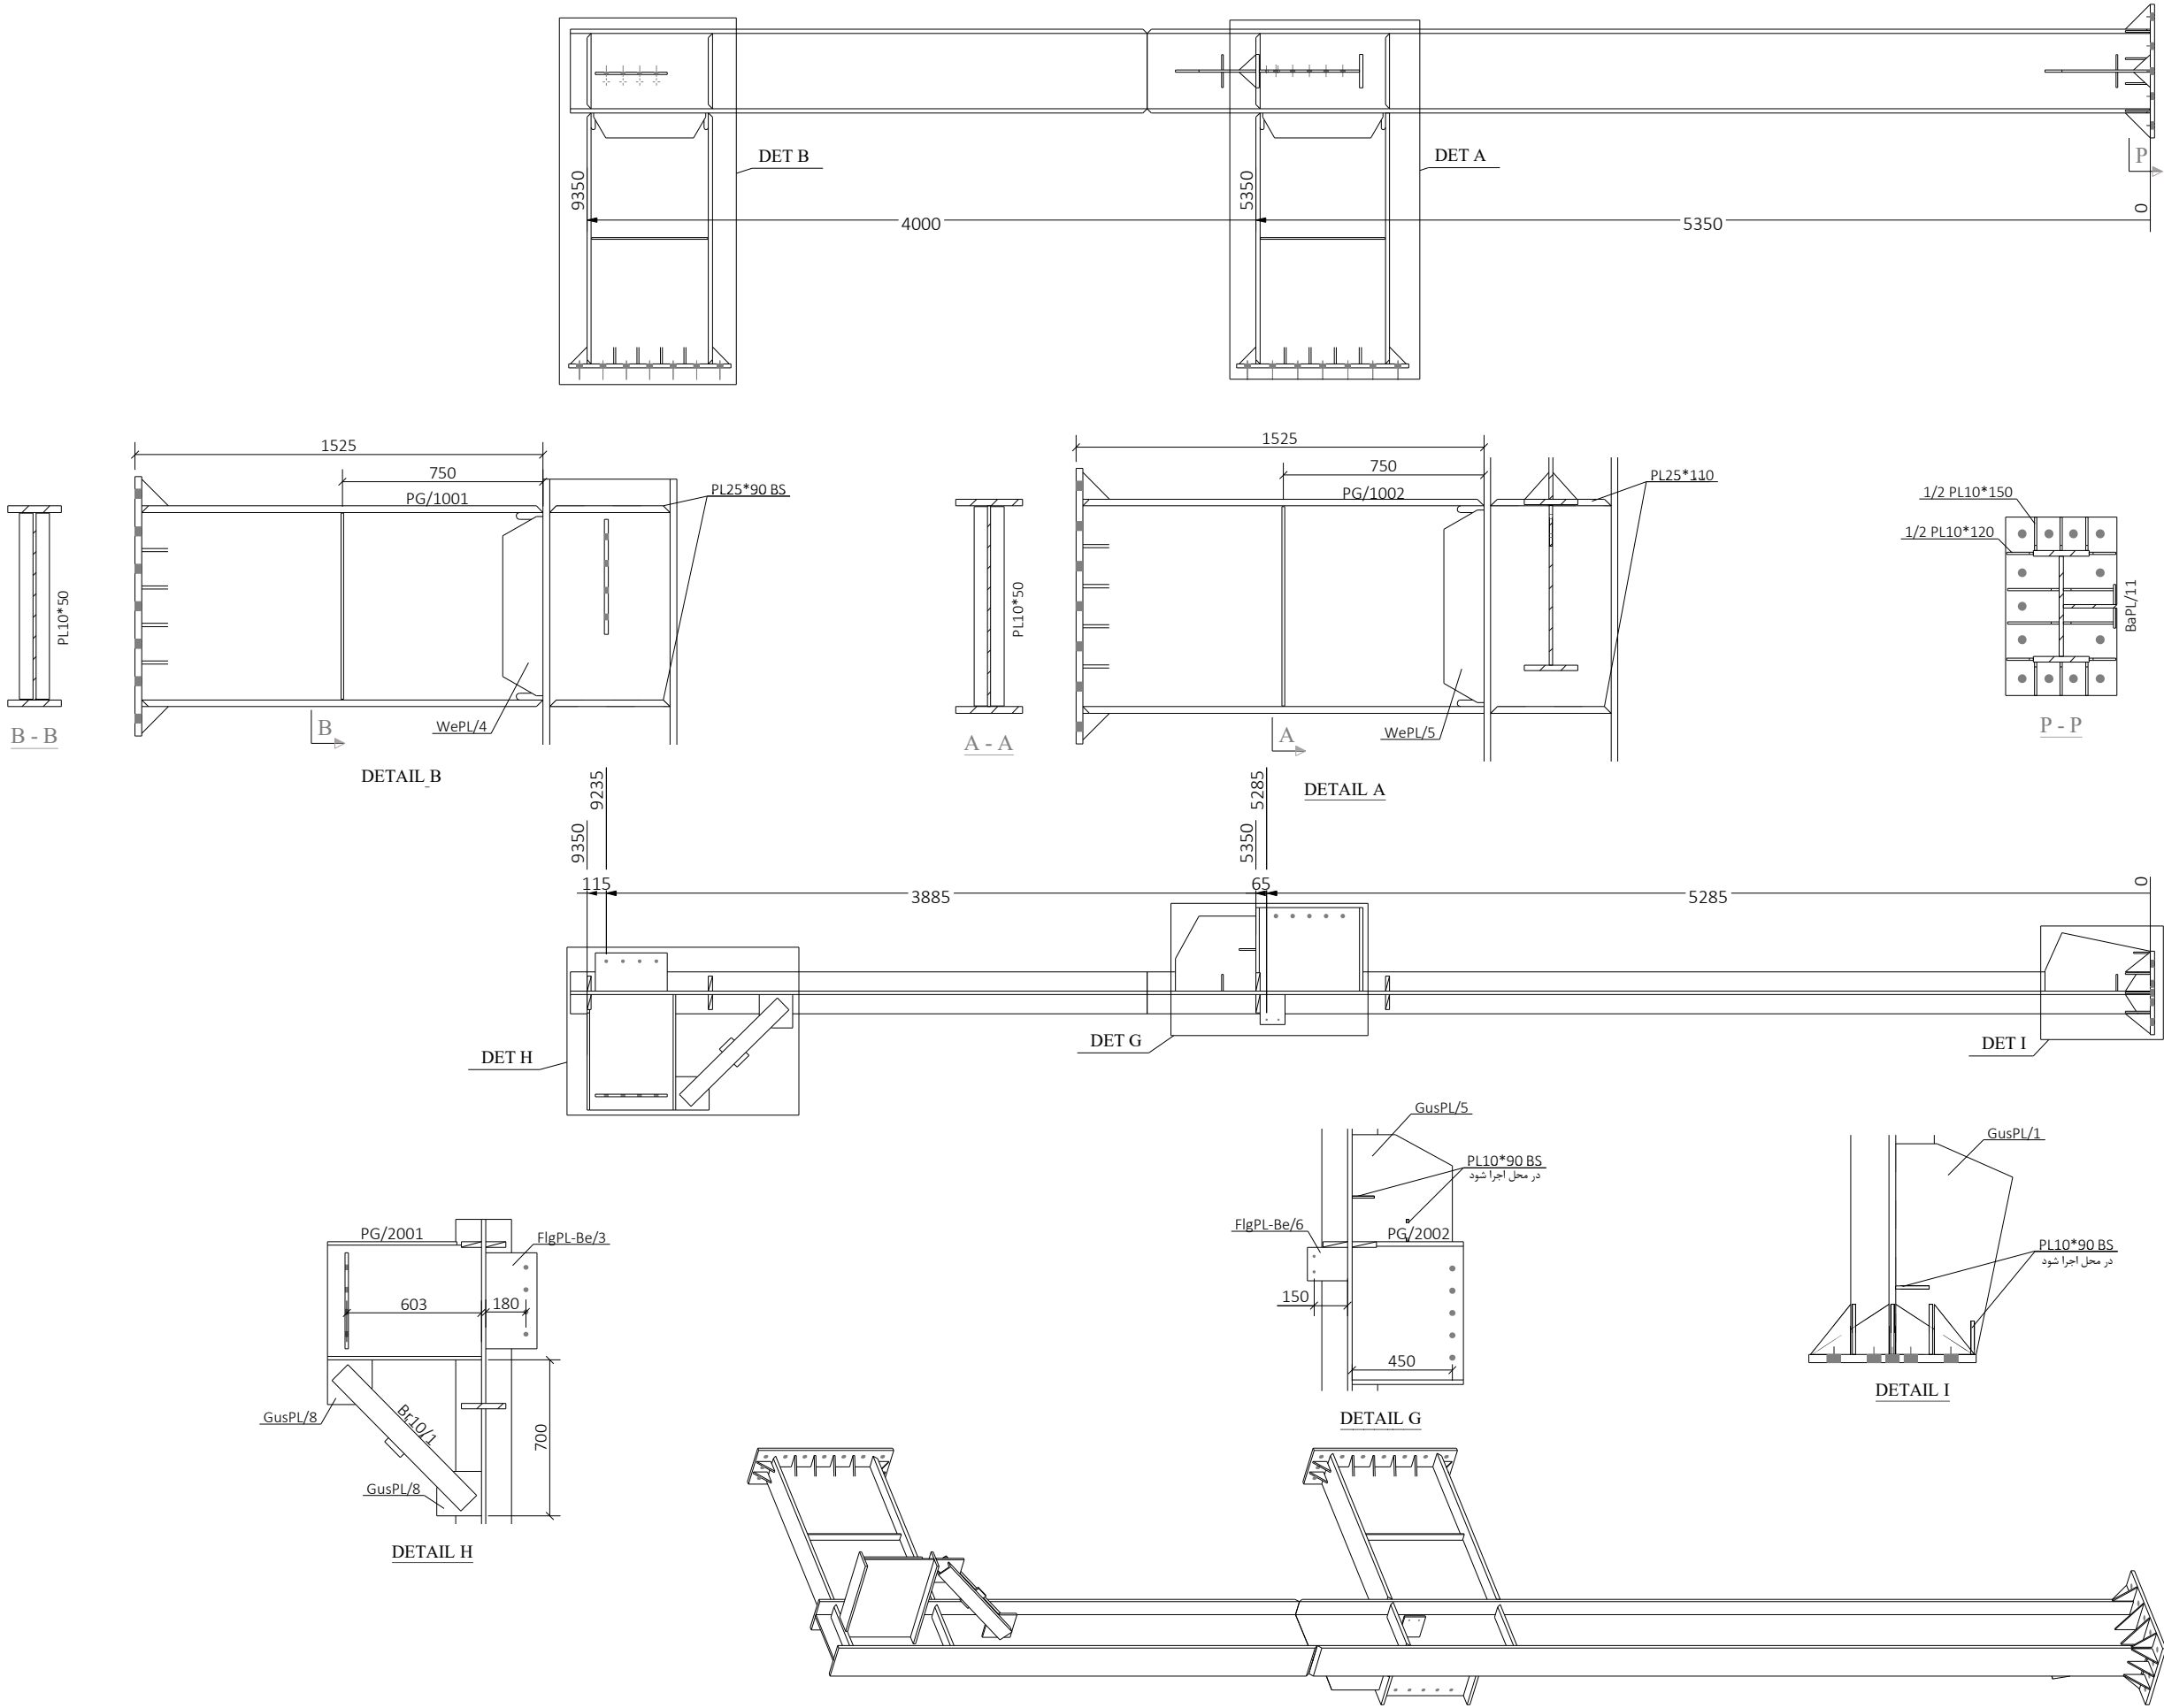

TITLE		ستون تکمیل		
CLIENT				
CONTRACTOR		ISSUED 04.03.		
MODELLED BY	EN ALMASI	SCALE 1:25	1:28	A3
DRAWING No	[C.4]	REVISION No. 0		

Tekla Structures









MATERIAL LIST FOR					C/6	N=1
Mark	Profile	No.	Length	Area	Weight	
1/2PL/1002	PL10*120	4	150	0.0	0.7	
1/2PL/1003	PL10*150	6	150	0.0	0.9	
1/2PL/1005	PL10*150	4	230	0.0	1.4	
1/2PL/1011	PL10*90	8	100	0.0	0.4	
BaPL/11	PL25*500	1	800	0.9	78.5	
FlgPL-Be/3	PL15*230	1	430	0.2	11.6	
FlgPL-Be/6	PL12*180	2	150	0.1	2.5	
GusPL/1	PL15*350	1	630	0.4	21.2	
GusPL/5	PL15*450	1	480	0.4	23.3	
Stf/1	PL25*90	8	450	0.1	7.5	
Stf/11	PL10*50	4	695	0.1	2.7	
WePL/4	PL12*150	2	670	0.2	8.6	
C/102	Assembly	1		19.3	1591.2	
PG/1001	Assembly	2		4.3	277.0	
PG/2002	Assembly	1		1.0	56.5	
Total			33.1	2446.1		

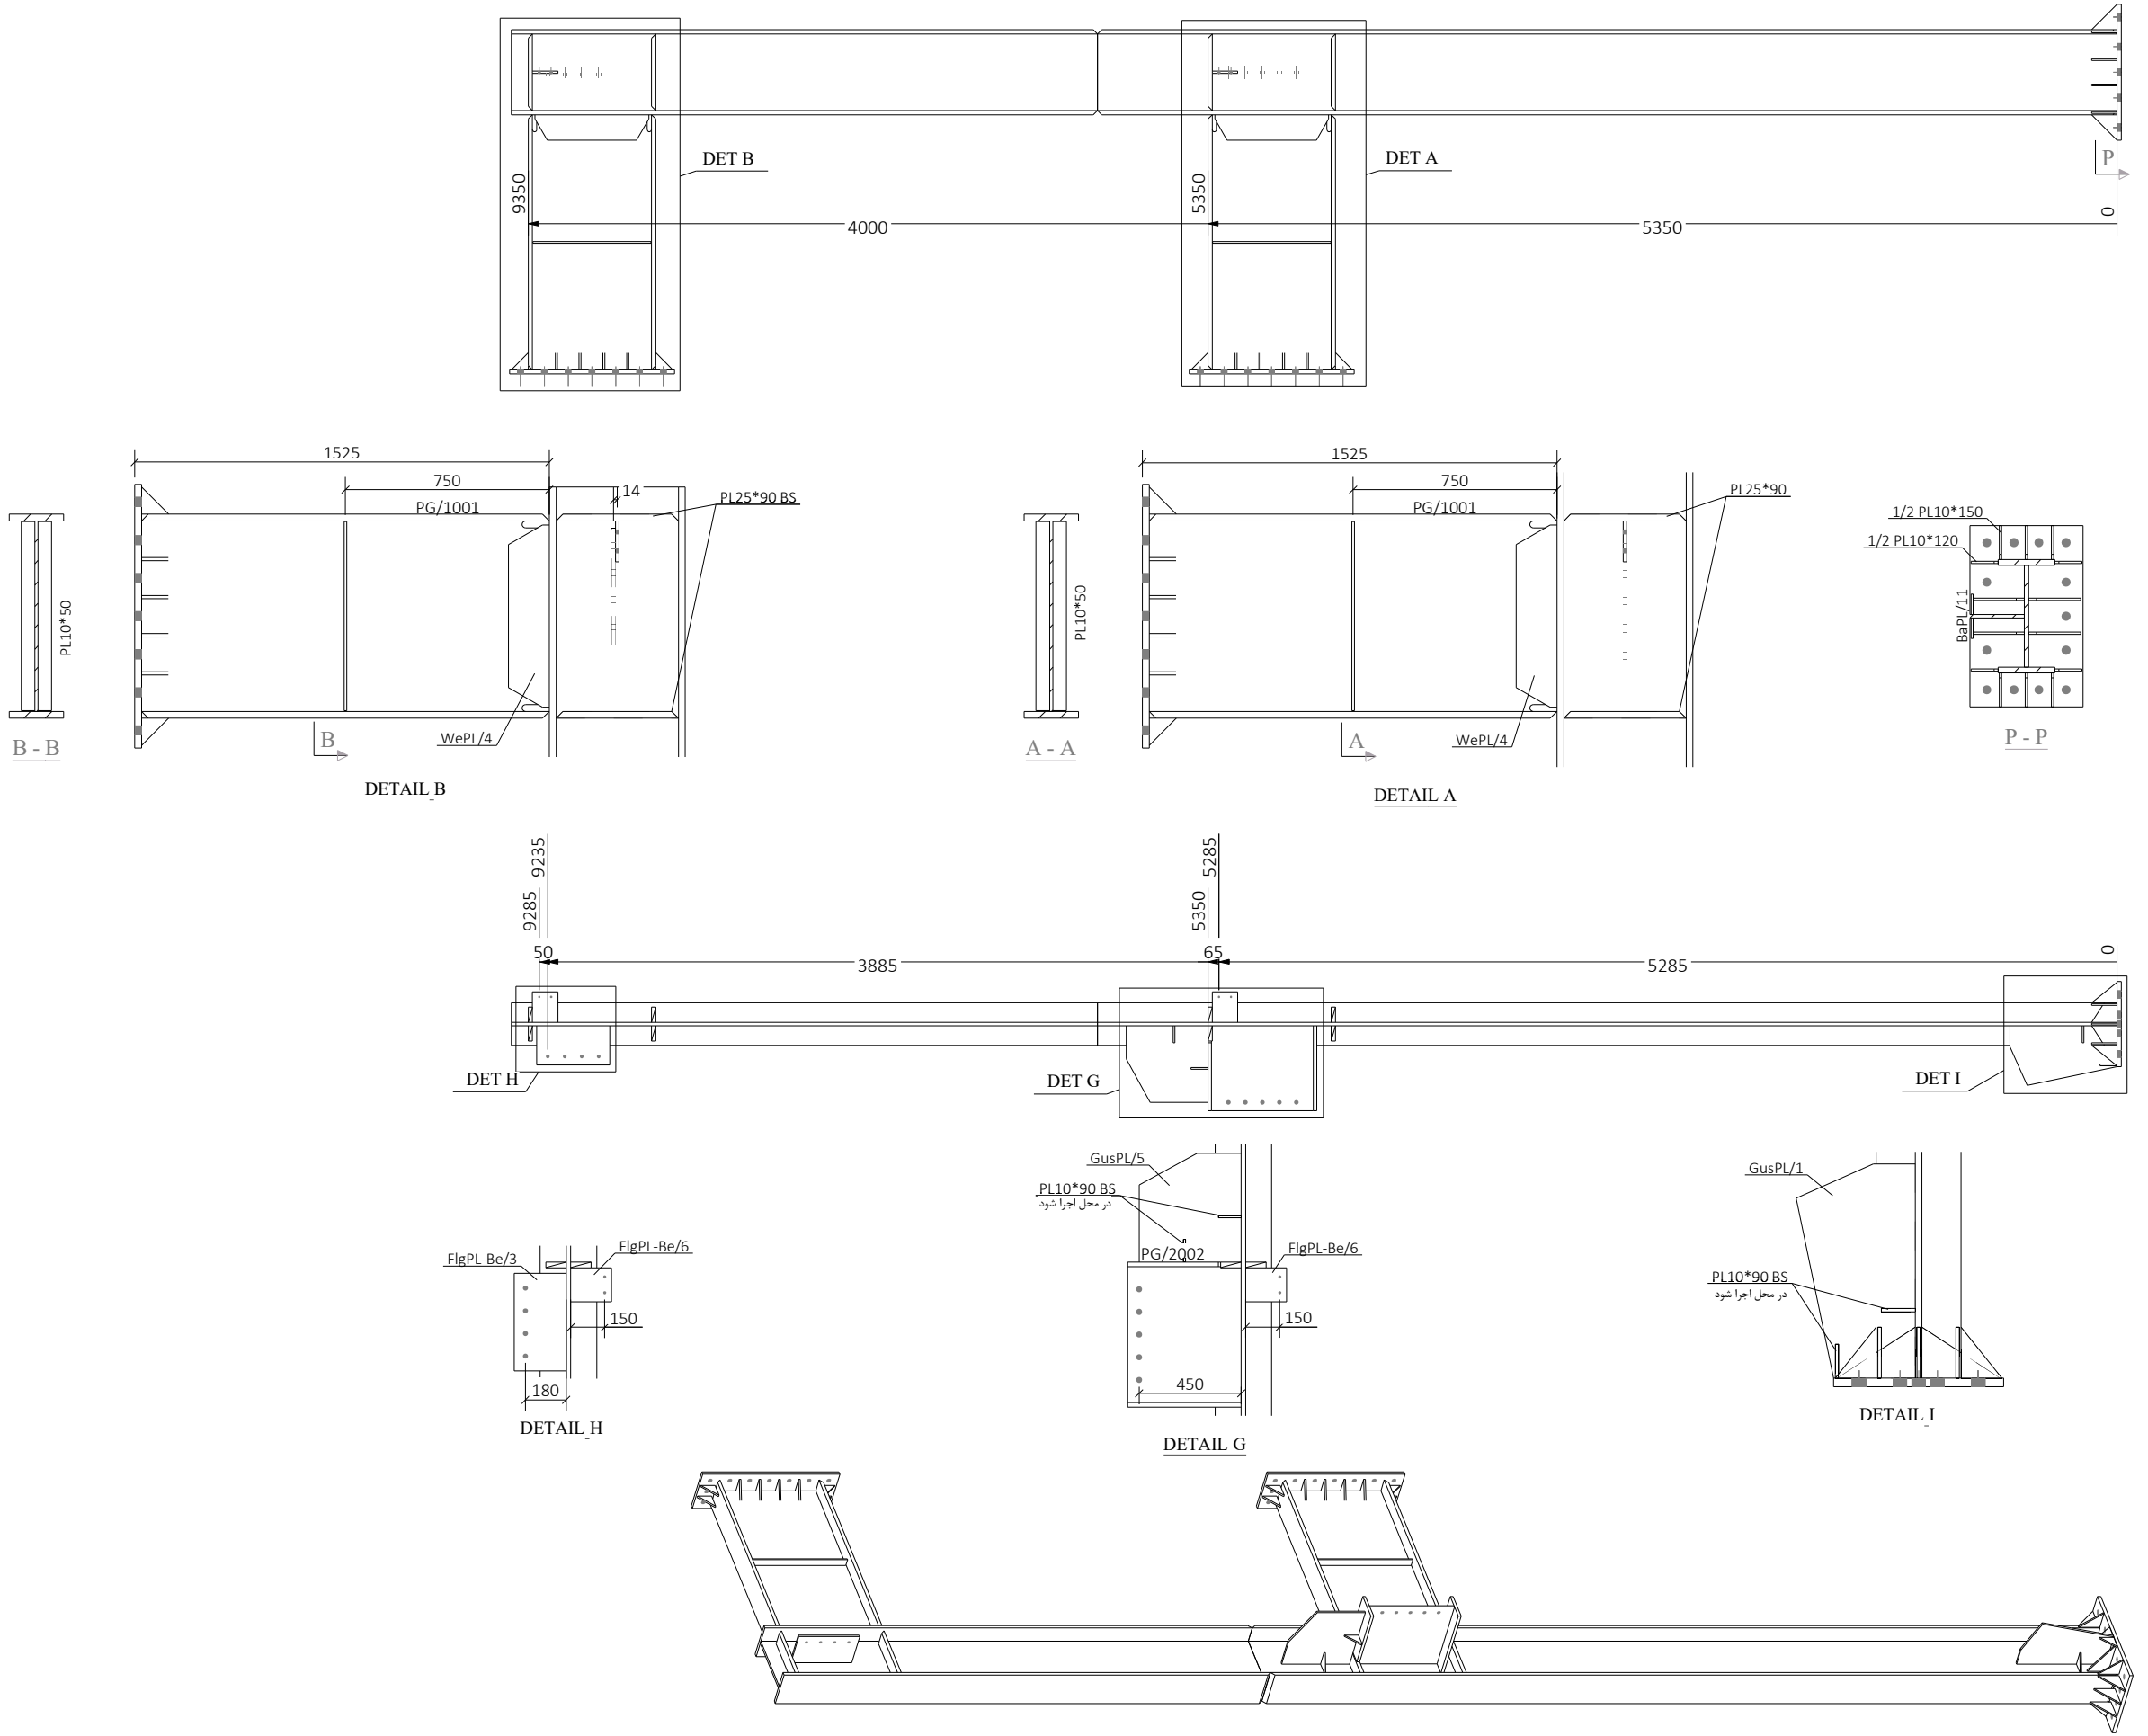

TITLE		ستون تکمیل		
CLIENT				
CONTRACTOR		ISSUED 04.03.		
MODELLED BY	EN ALMASI	SCALE	1:25 1:28	A3
DRAWING No	[C.6]	REVISION No.	0	


Tekla Structures

MATERIAL LIST FOR C/7 N=1					
Mark	Profile	No.	Length	Area	Weight
1/2PL/1002	PL10*120	4	150	0.0	0.7
1/2PL/1003	PL10*150	6	150	0.0	0.9
1/2PL/1005	PL10*150	4	230	0.0	1.4
BaPL/1	PL25*500	1	800	0.9	78.5
FlgPL-Be/6	PL12*180	4	150	0.1	2.5
Stf/1	PL25*90	8	450	0.1	7.5
Stf/11	PL10*50	4	695	0.1	2.7
WePL/4	PL12*150	2	670	0.2	8.6
C/102	Assembly	1		19.3	1591.2
PG/1001	Assembly	2		4.3	277.0
Total				31.1	2335.7

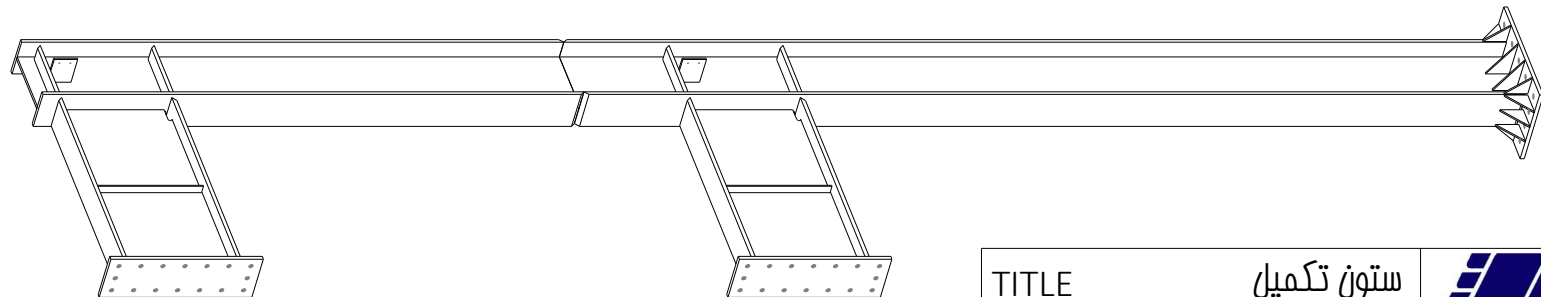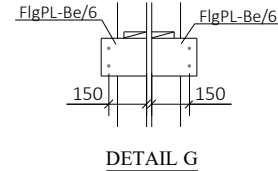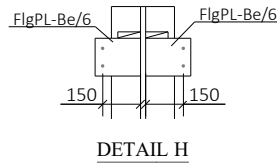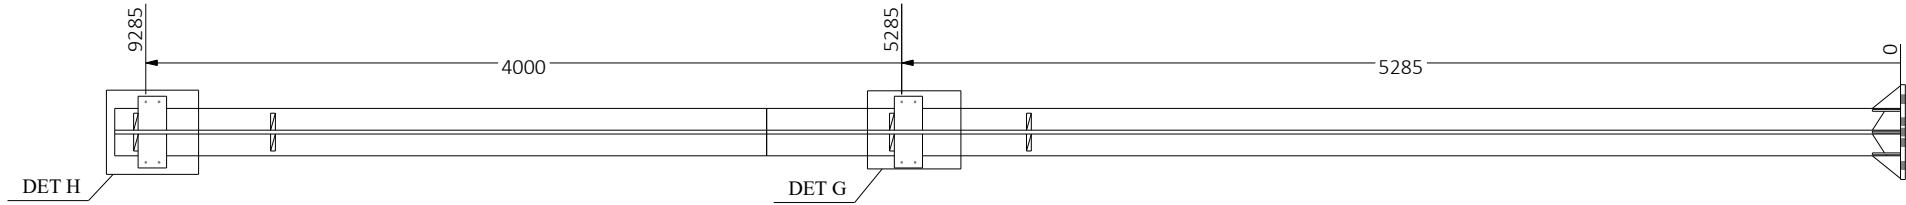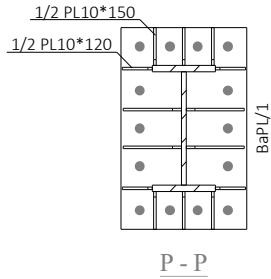
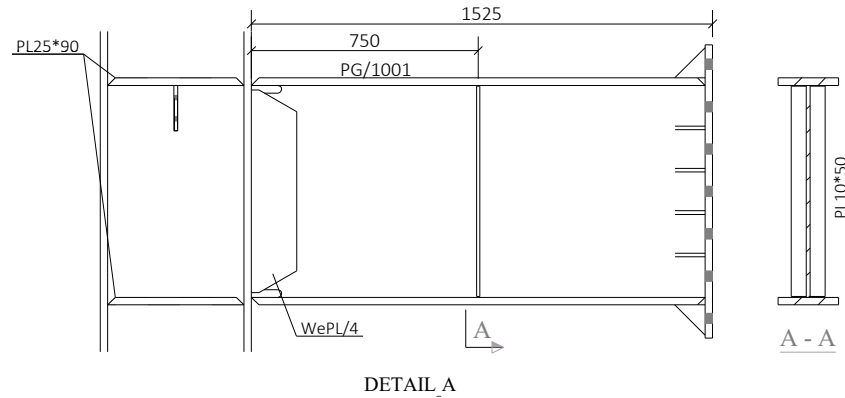
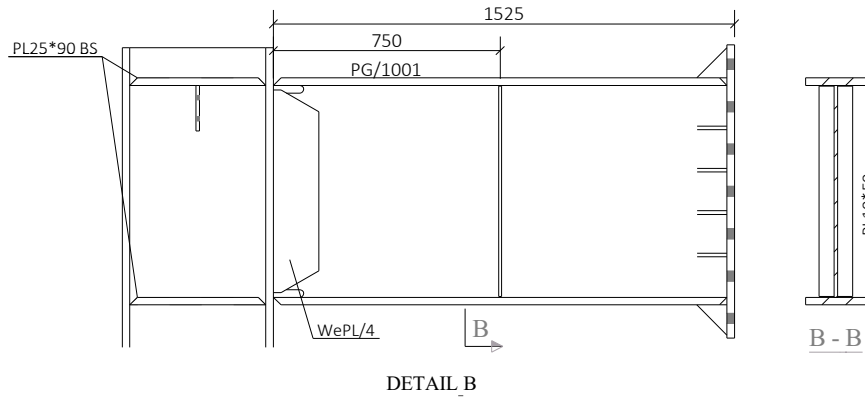
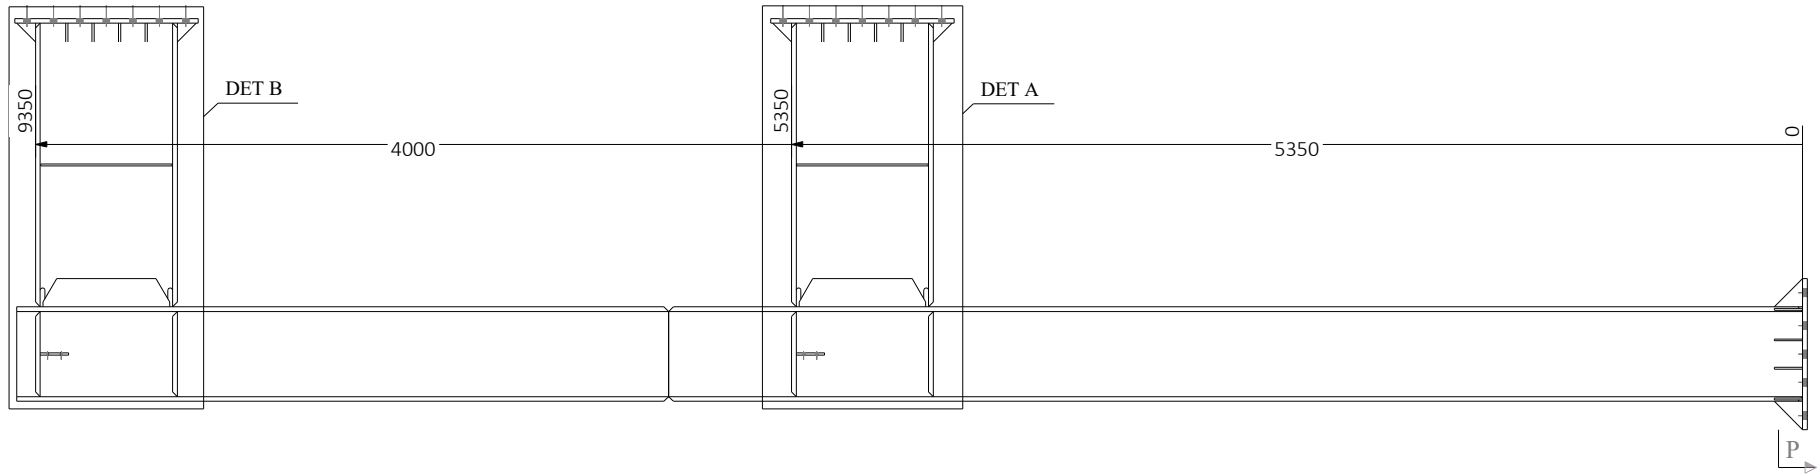


TITLE		ستون تکمیل		
CLIENT				
CONTRACTOR		ISSUED 04.03.		
MODELLED BY	EN ALMASI	SCALE 1:25	1:28	A3
DRAWING No	[C.7]	REVISION No. 0		


MATERIAL LIST FOR C/9 N=1					
Mark	Profile	No.	Length	Area	Weight
1/2PL/1002	PL10*120	4	150	0.0	0.7
1/2PL/1003	PL10*150	4	150	0.0	0.9
1/2PL/1004	PL10*150	4	210	0.0	1.2
1/2PL/1011	PL10*90	10	100	0.0	0.4
1/2PL/1012	PL10*60	2	100	0.0	0.2
BaPL/21	PL20*450	1	800	0.8	56.5
FlgPL-Be/4	PL15*180	1	430	0.2	9.1
FlgPL-Be/7	PL12*160	2	150	0.1	2.3
GusPL/3	PL15*400	1	600	0.4	21.1
GusPL/6	PL15*420	2	500	0.4	23.2
Stf/8	PL12*80	4	450	0.1	3.3
Stf/9	PL12*60	8	300	0.0	1.6
Stf/16	PL10*50	6	245	0.0	1.0
WePL/2	PL8*150	3	218	0.1	1.5
C/103	Assembly	1		20.3	1339.3
P27/1001	Assembly	3		0.9	35.0
PG/2002	Assembly	1		1.0	56.5
PG/2003	Assembly	1		0.8	31.9
Total				28.6	1722.2

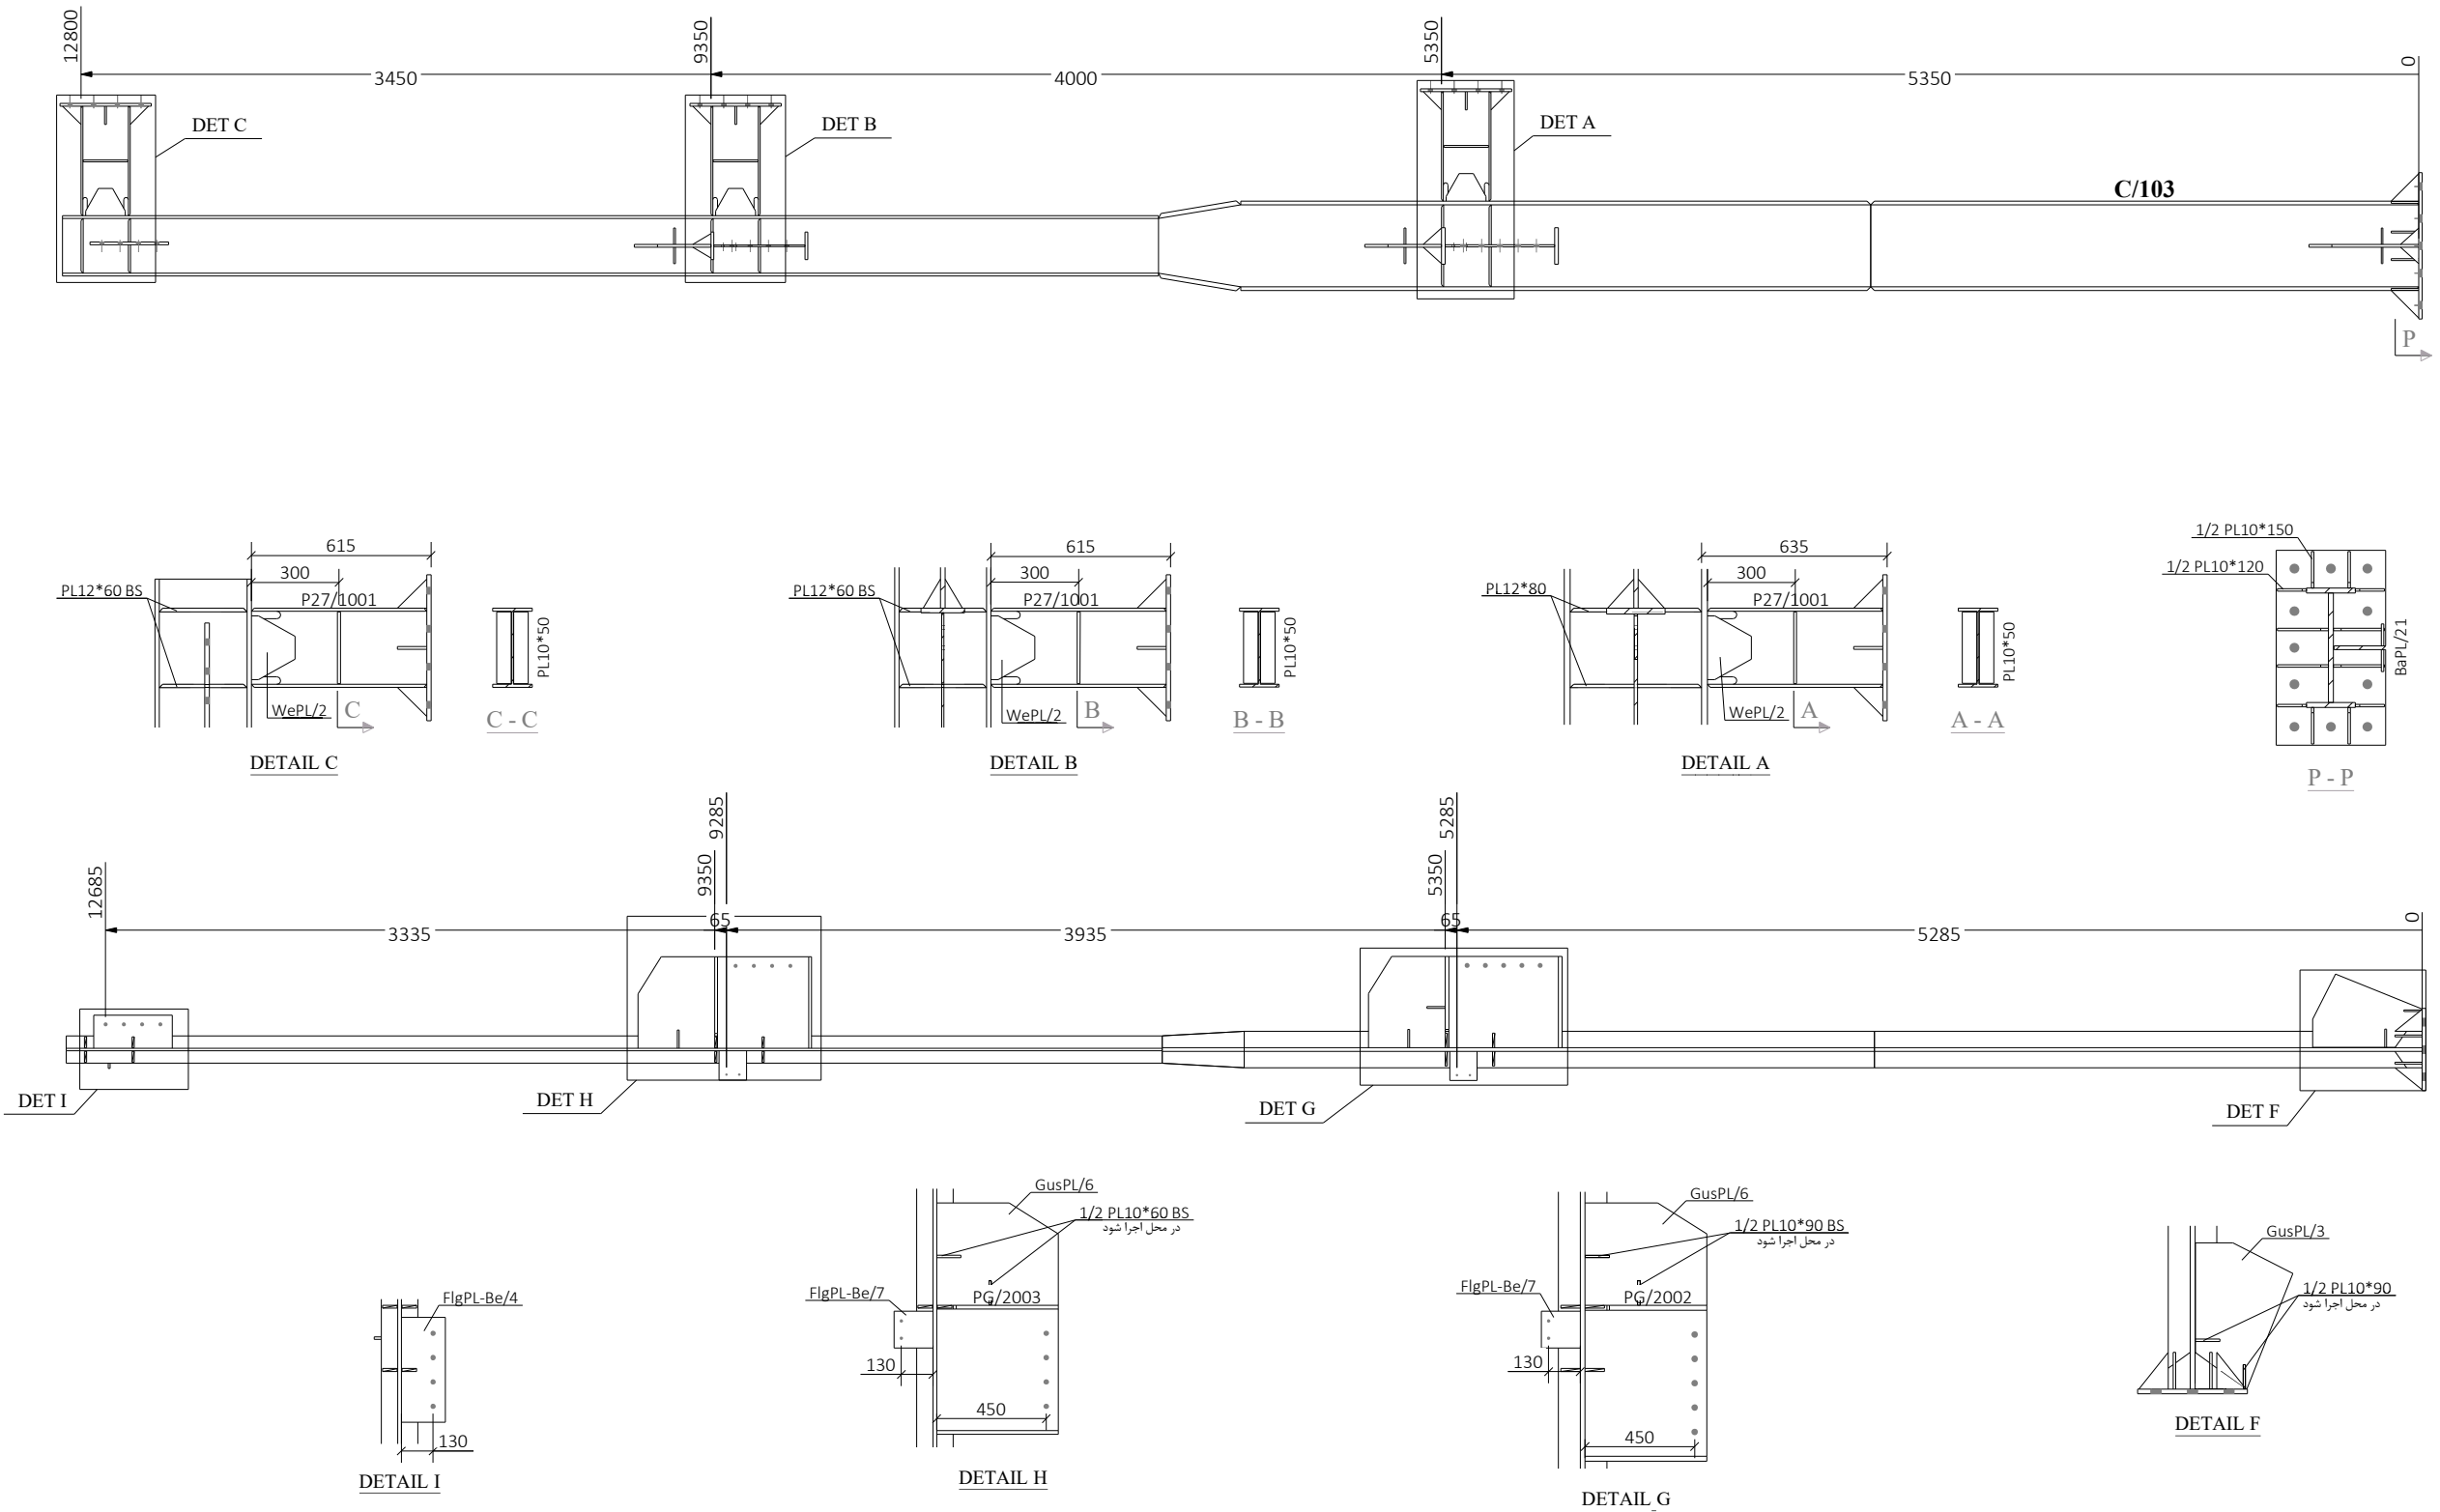

TITLE		ستون تکمیل		
CLIENT				
CONTRACTOR		ISSUED 04.03.		
MODELLED BY	EN ALMASI	SCALE	1:25 1:28	A3
DRAWING No	[C.9]	REVISION No.	0	

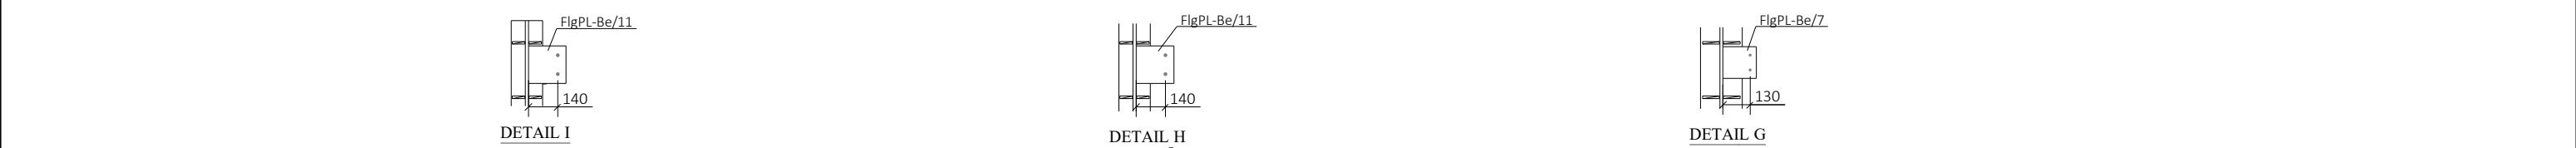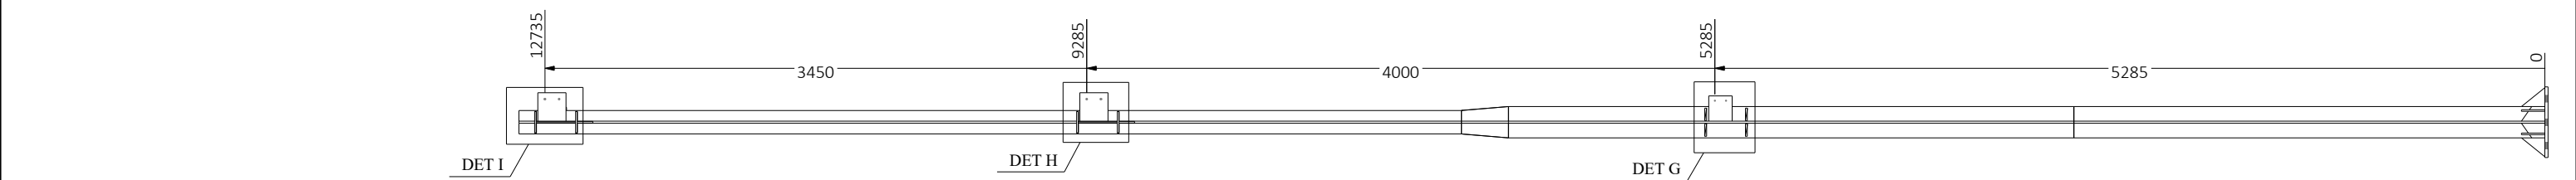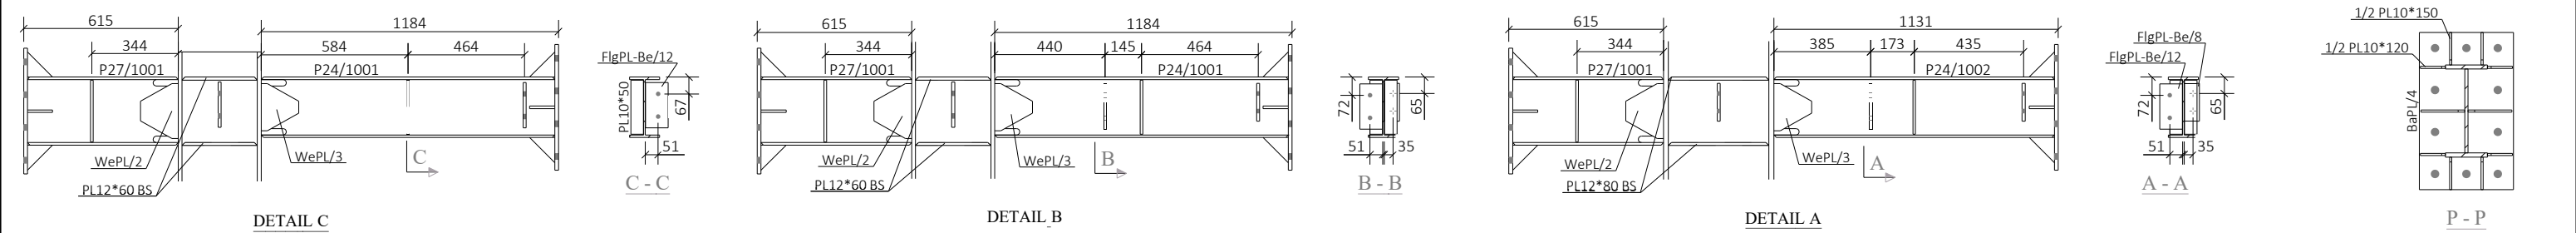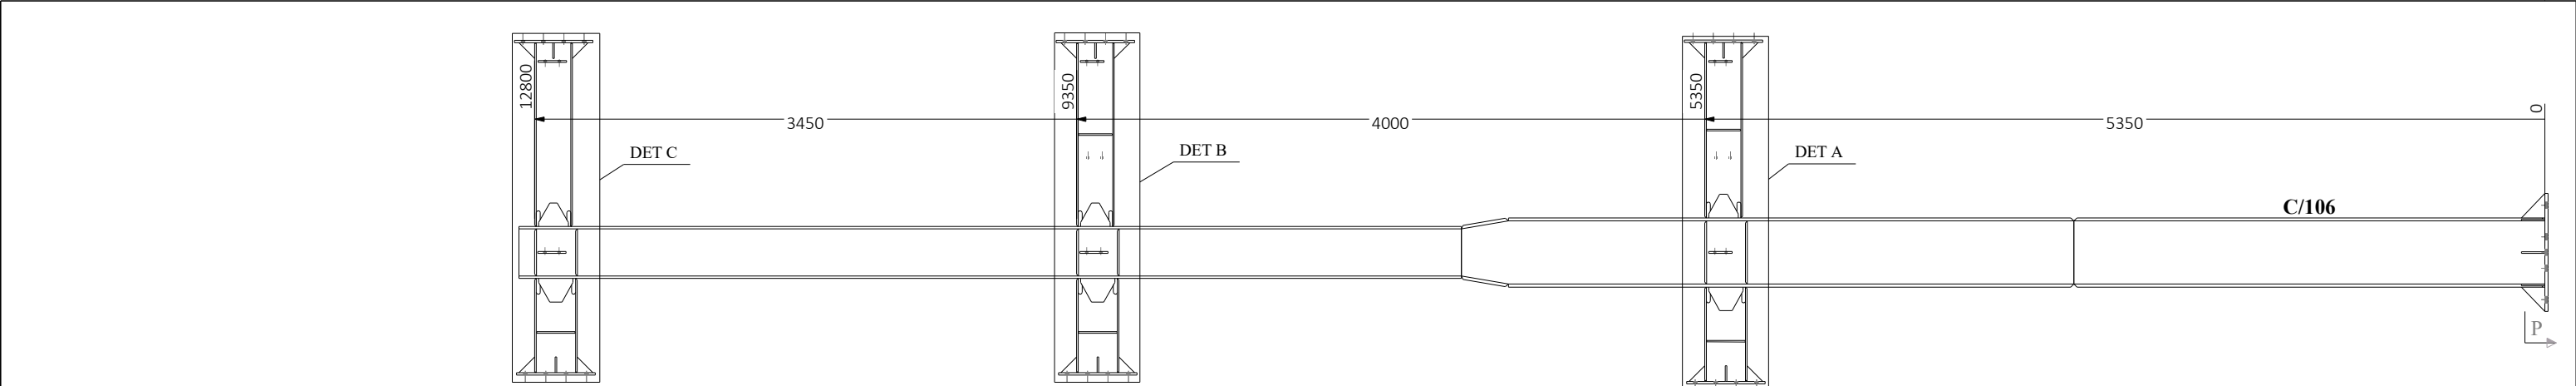


MATERIAL LIST FOR C/10 N=1					
Mark	Profile	No.	Length	Area	Weight
1/2PL/1002	PL10*120	4	150	0.0	0.7
1/2PL/1004	PL10*150	2	210	0.0	1.2
1/2PL/1008	PL10*150	4	155	0.0	0.9
BaPL/4	PL20*450	1	750	0.7	53.0
FlgPL-Be/7	PL12*160	1	150	0.1	2.3
FlgPL-Be/8	PL12*60	2	150	0.0	0.8
FlgPL-Be/11	PL12*180	2	180	0.1	3.1
FlgPL-Be/12	PL12*90	3	180	0.0	1.5
Stf/7	PL12*80	4	400	0.1	2.9
Stf/9	PL12*60	8	300	0.0	1.6
Stf/15	PL10*50	5	215	0.0	0.8
Stf/16	PL10*50	6	245	0.0	1.0
WePL/2	PL8*150	3	218	0.1	1.5
WePL/3	PL8*150	3	188	0.0	1.2
C/106	Assembly	1		19.5	1175.6
P24/1001	Assembly	2		1.4	49.2
P24/1002	Assembly	1		1.3	47.6
P27/1001	Assembly	3		0.9	35.0
Total				28.9	1545.9

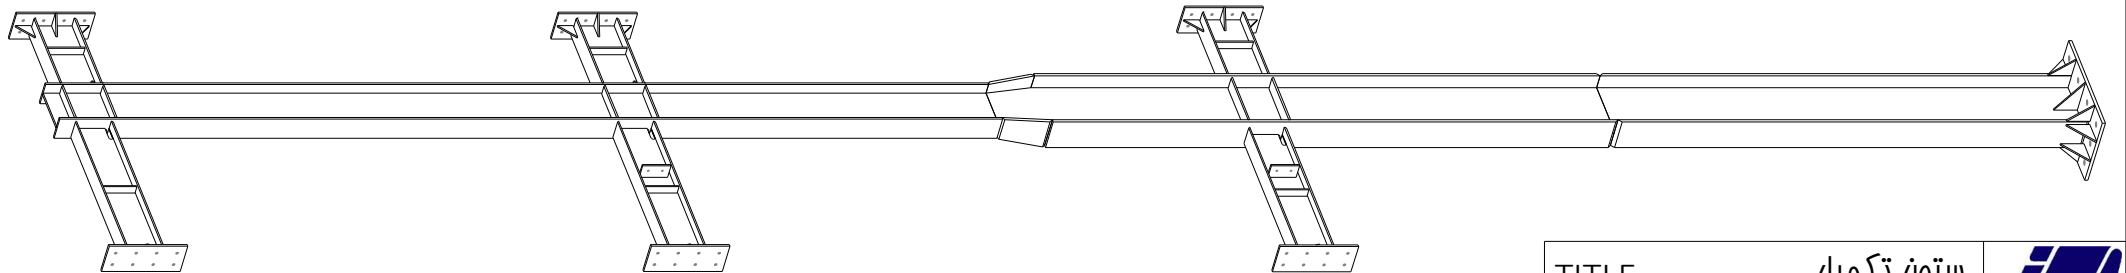



TITLE		ستون تکمیل		
CLIENT				
CONTRACTOR		ISSUED 04.03.		
MODELLED BY	EN ALMASI	SCALE	1:25 1:28	A3
DRAWING No	[C.10]	REVISION No.	0	

Tekla Structures

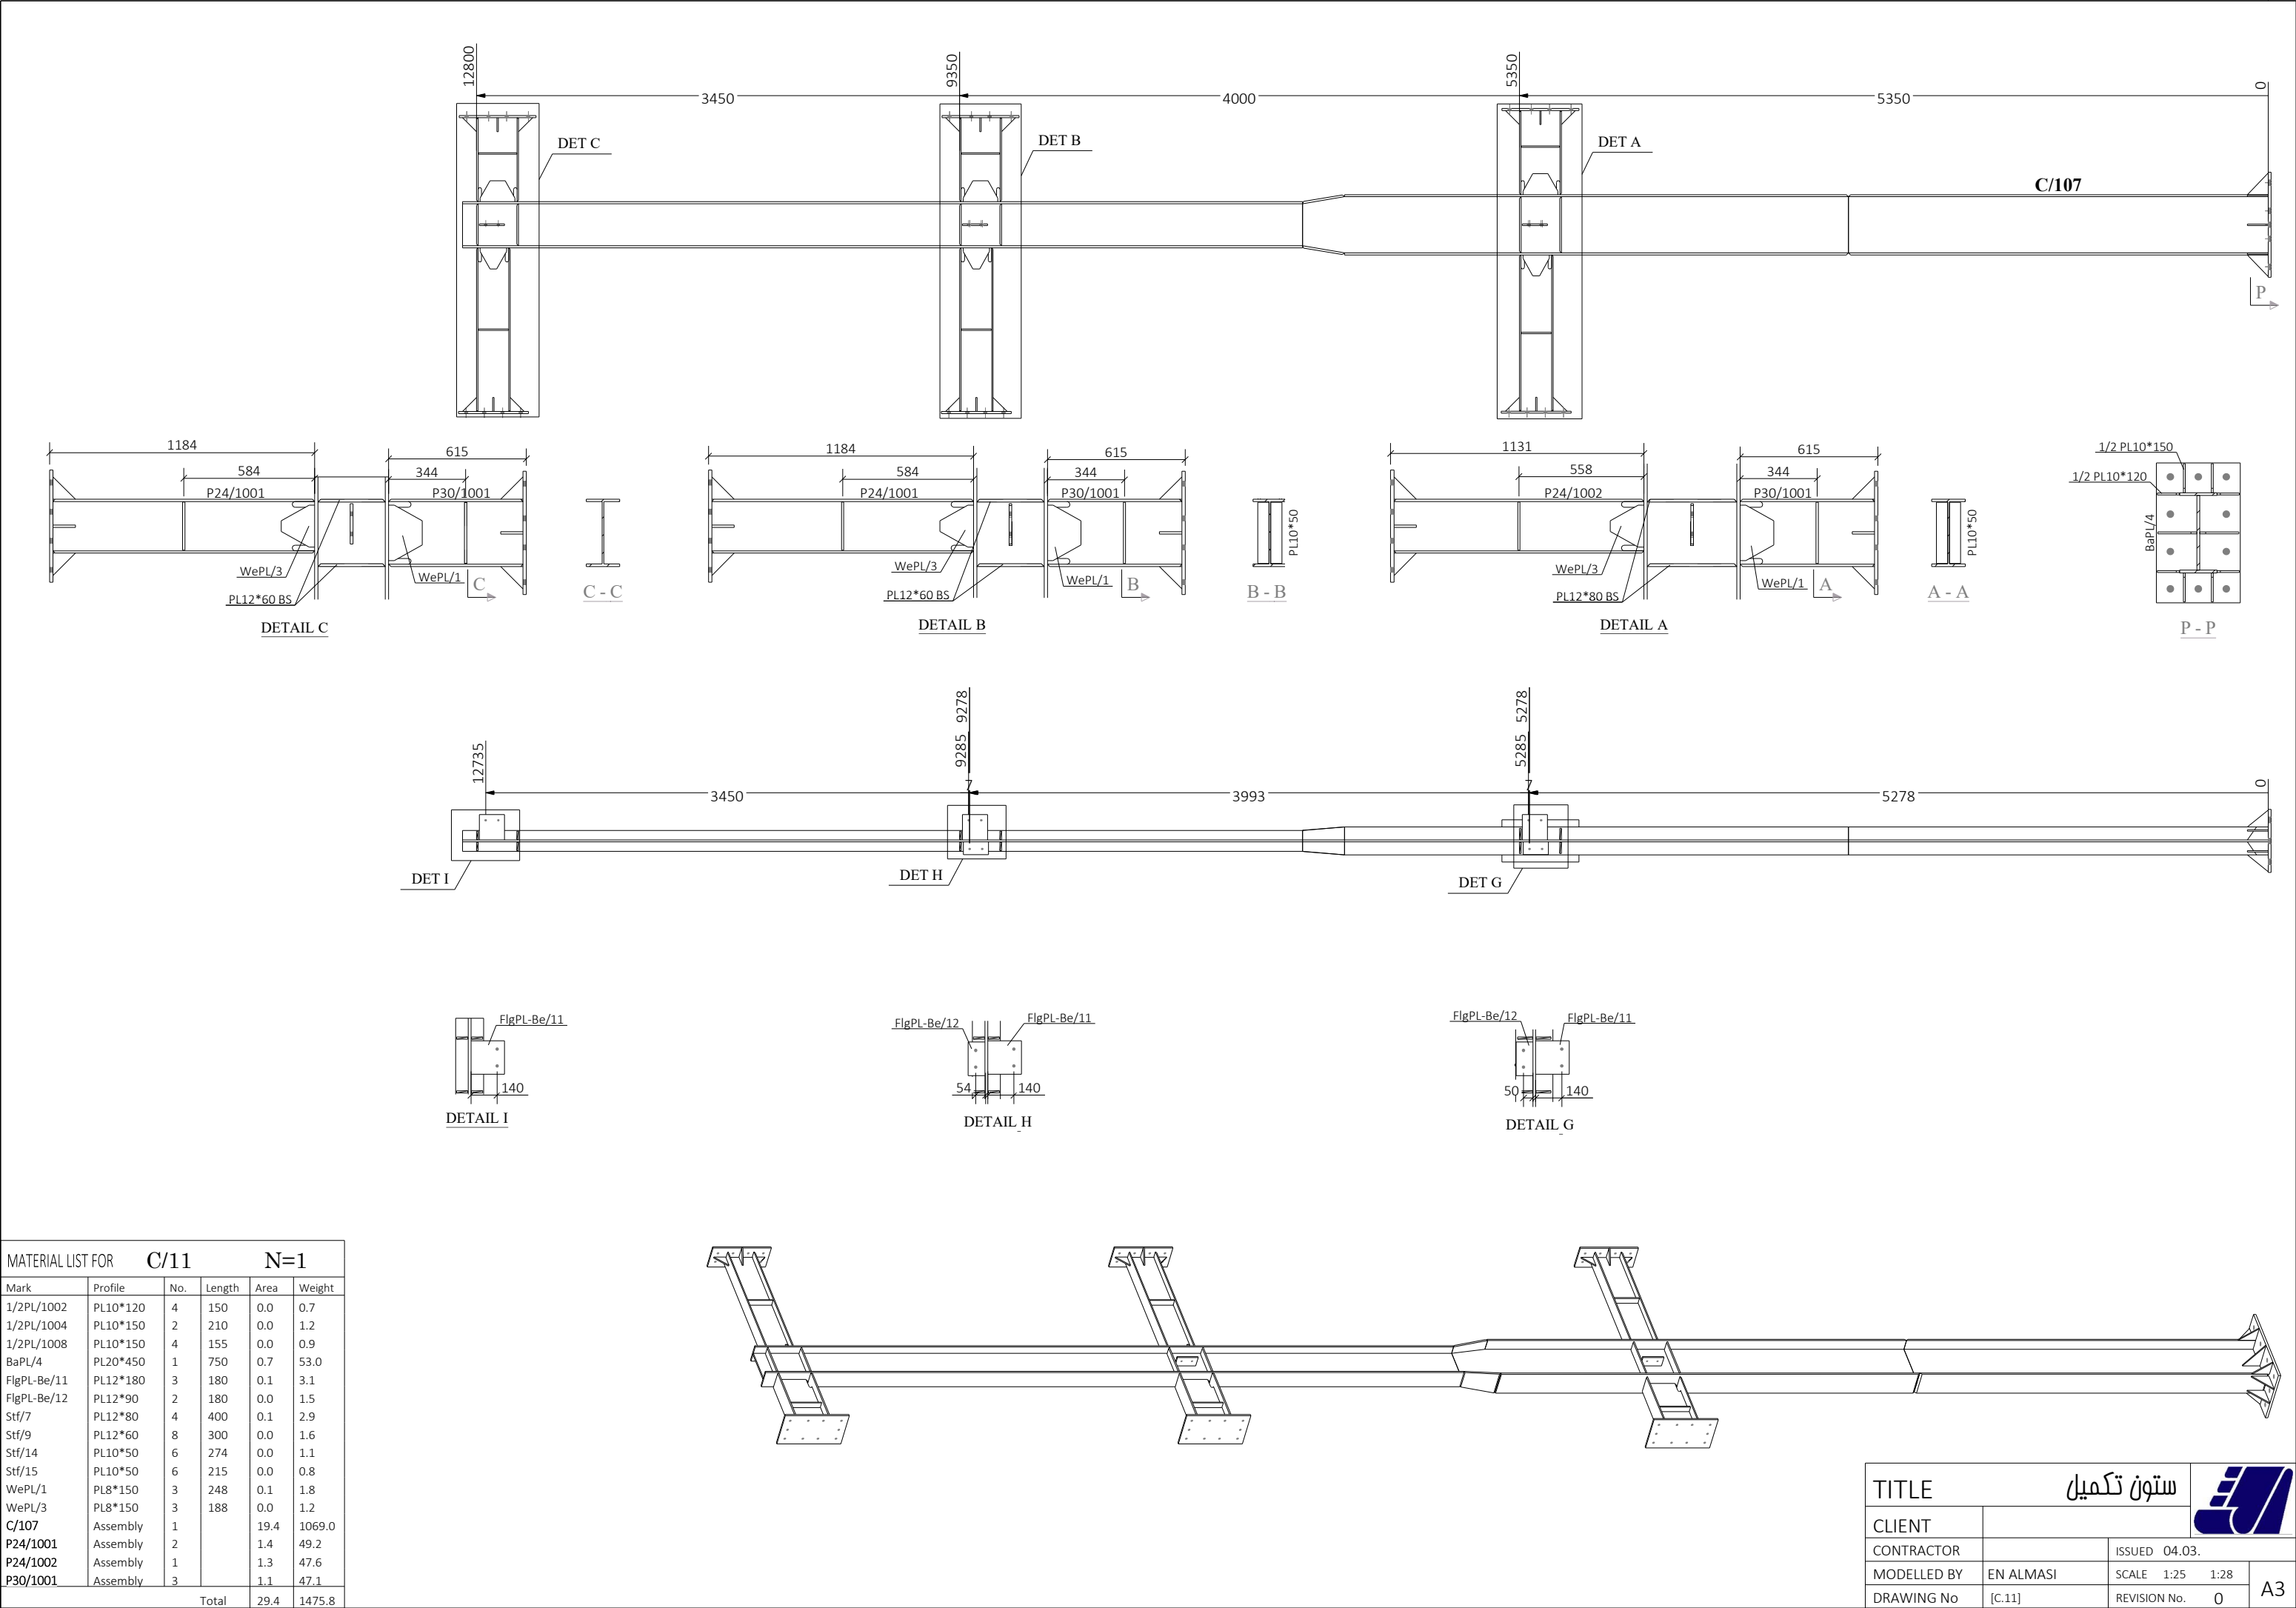



TITLE		ستون تکمیل		
CLIENT				
CONTRACTOR		ISSUED 04.03.		
MODELLED BY	EN ALMASI	SCALE 1:25	1:28	A3
DRAWING No	[C.11]	REVISION No. 0		

MATERIAL LIST FOR C/12					N=1
Mark	Profile	No.	Length	Area	Weight
1/2PL/1002	PL10*120	4	150	0.0	0.7
1/2PL/1004	PL10*150	2	210	0.0	1.2
1/2PL/1008	PL10*150	4	155	0.0	0.9
BaPL/4	PL20*450	1	750	0.7	53.0
FlgPL-Be/11	PL12*180	3	180	0.1	3.1
FlgPL-Be/12	PL12*90	2	180	0.0	1.5
Stf/7	PL12*80	4	400	0.1	2.9
Stf/9	PL12*60	8	300	0.0	1.6
Stf/13	PL10*50	4	295	0.0	1.2
Stf/14	PL10*50	8	274	0.0	1.1
WePL/1	PL8*150	4	248	0.1	1.8
WePL/6	PL10*150	2	270	0.1	2.5
C/107	Assembly	1		19.4	1069.0
P30/1001	Assembly	4		1.1	47.1
PG/1003	Assembly	2		1.2	49.4
Total				29.1	1480.5

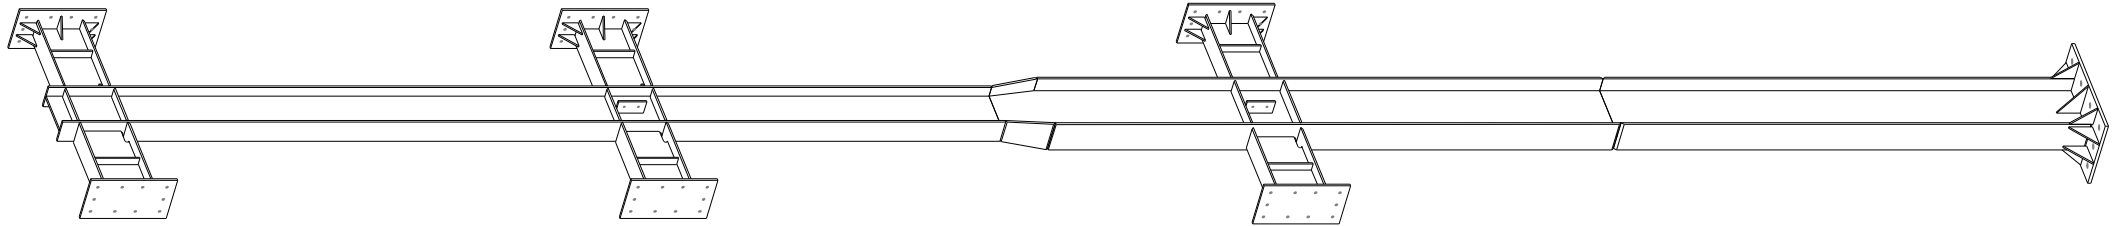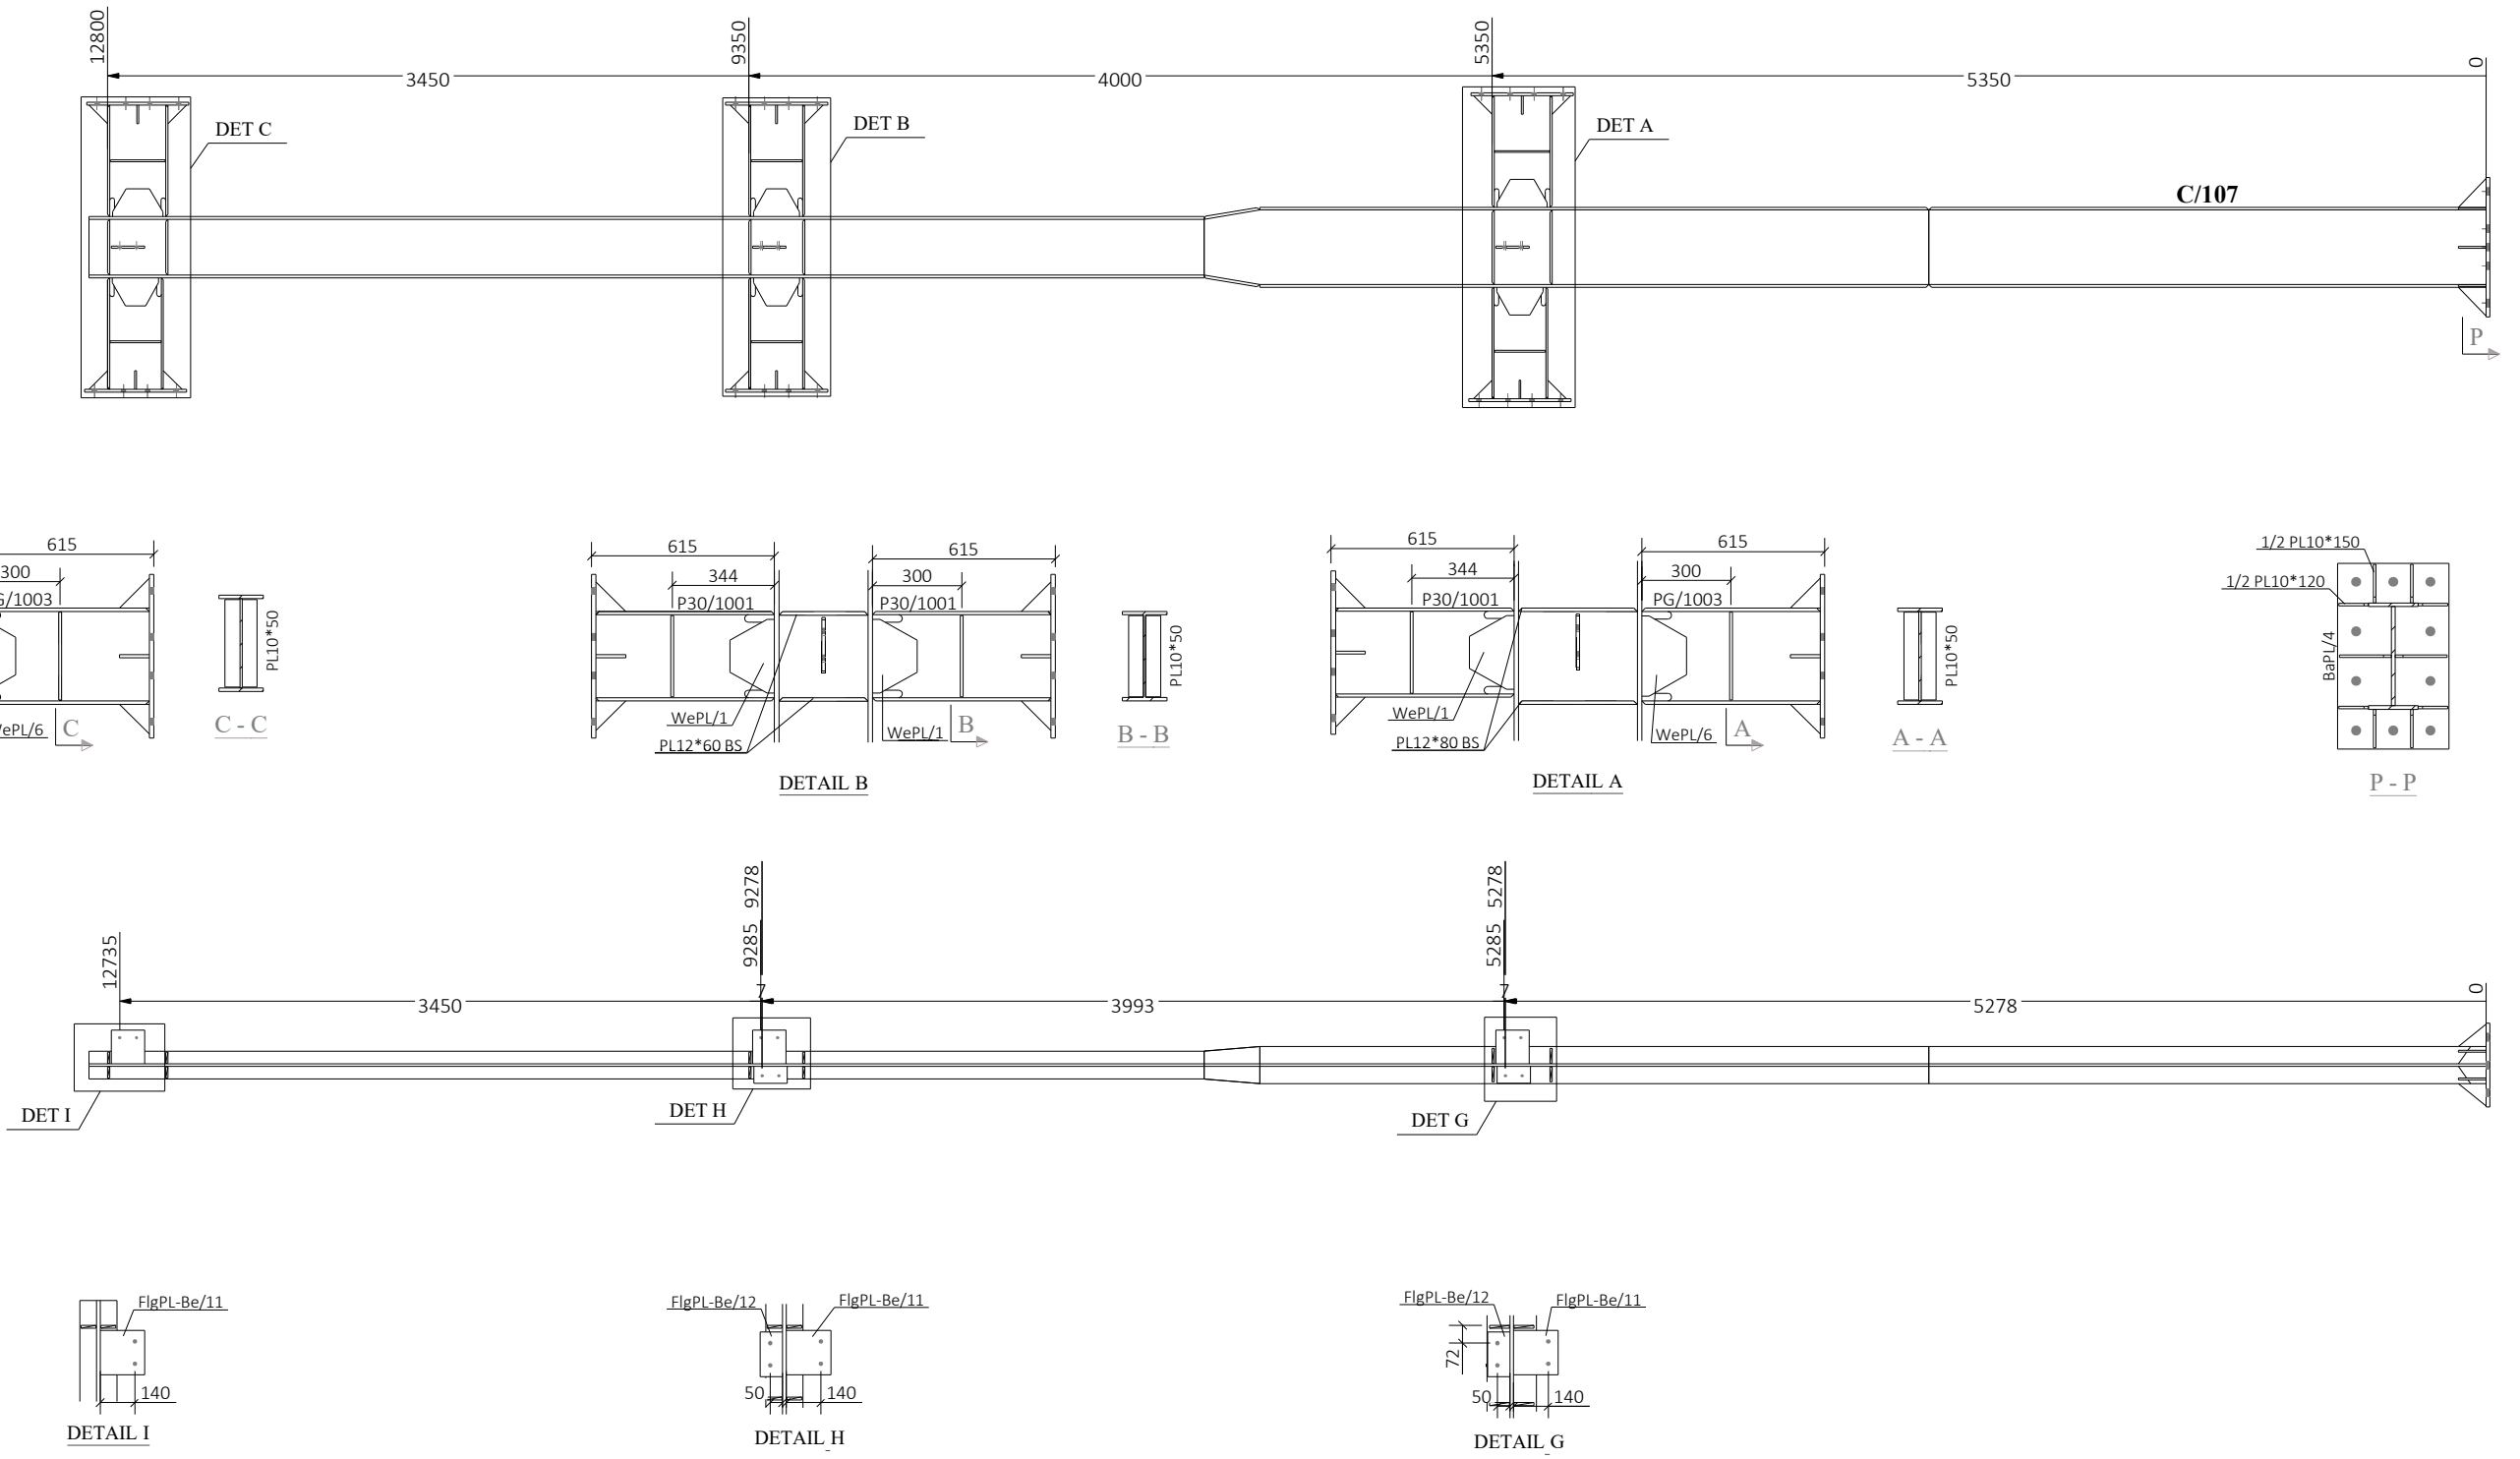


TITLE		ستون تکمیل		
CLIENT				
CONTRACTOR		ISSUED 04.03.		
MODELLED BY	EN ALMASI	SCALE	1:25	1:28
DRAWING No	[C.12]	REVISION No.	0	A3


MATERIAL LIST FOR C/13 N=1					
Mark	Profile	No.	Length	Area	Weight
1/2PL/1002	PL10*120	4	150	0.0	0.7
1/2PL/1003	PL10*150	4	150	0.0	0.9
1/2PL/1004	PL10*150	4	210	0.0	1.2
1/2PL/1011	PL10*90	10	100	0.0	0.4
1/2PL/1012	PL10*60	2	100	0.0	0.2
BaPL/21	PL20*450	1	800	0.8	56.5
FlgPL-Be/4	PL15*180	1	430	0.2	9.1
FlgPL-Be/7	PL12*160	2	150	0.1	2.3
GusPL/3	PL15*400	1	600	0.4	21.1
GusPL/6	PL15*420	2	500	0.4	23.2
Stf/8	PL12*80	4	450	0.1	3.3
Stf/9	PL12*60	8	300	0.0	1.6
Stf/13	PL10*50	4	295	0.0	1.2
Stf/14	PL10*50	2	274	0.0	1.1
WePL/1	PL8*150	1	248	0.1	1.8
WePL/6	PL10*150	2	270	0.1	2.5
C/111	Assembly	1	20.4	1439.5	
P30/1001	Assembly	1		1.1	47.1
PG/1003	Assembly	2		1.2	49.4
PG/2002	Assembly	1		1.0	56.5
PG/2003	Assembly	1		0.8	31.9
Total				29.7	1866.6

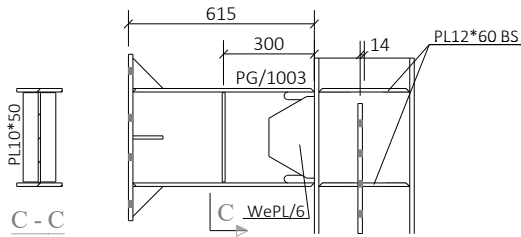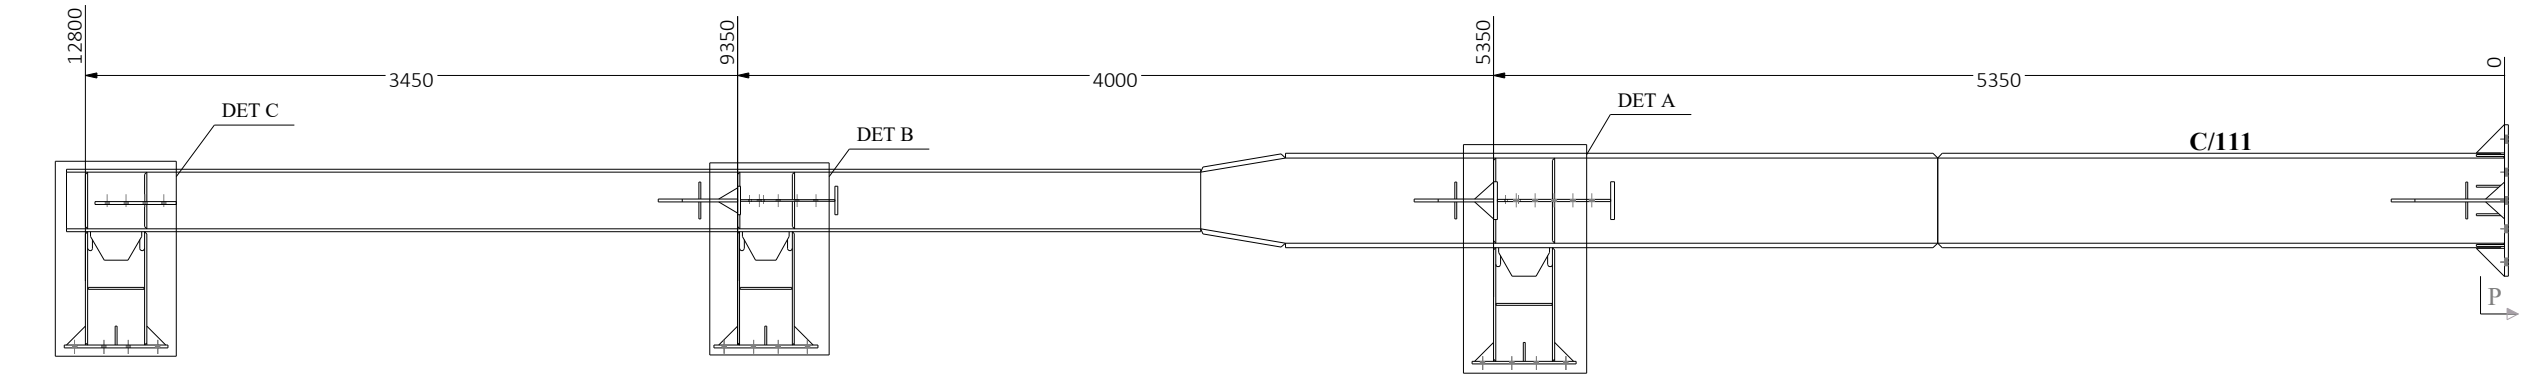


DETAIL C

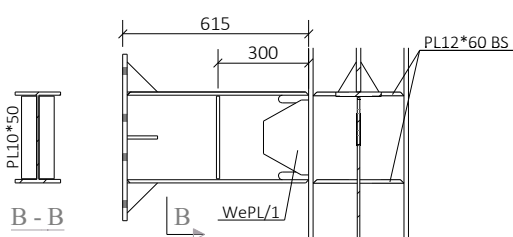



DETAIL B

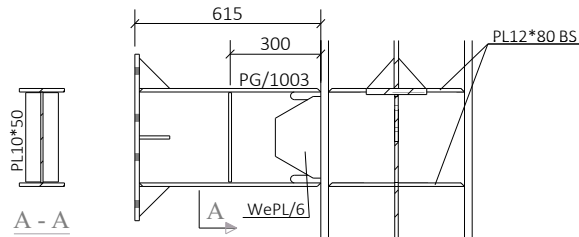


DETAIL A

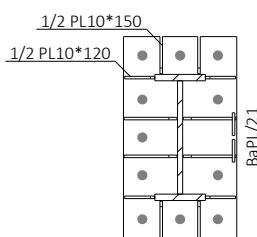


P - P

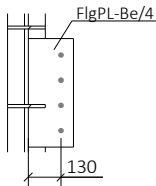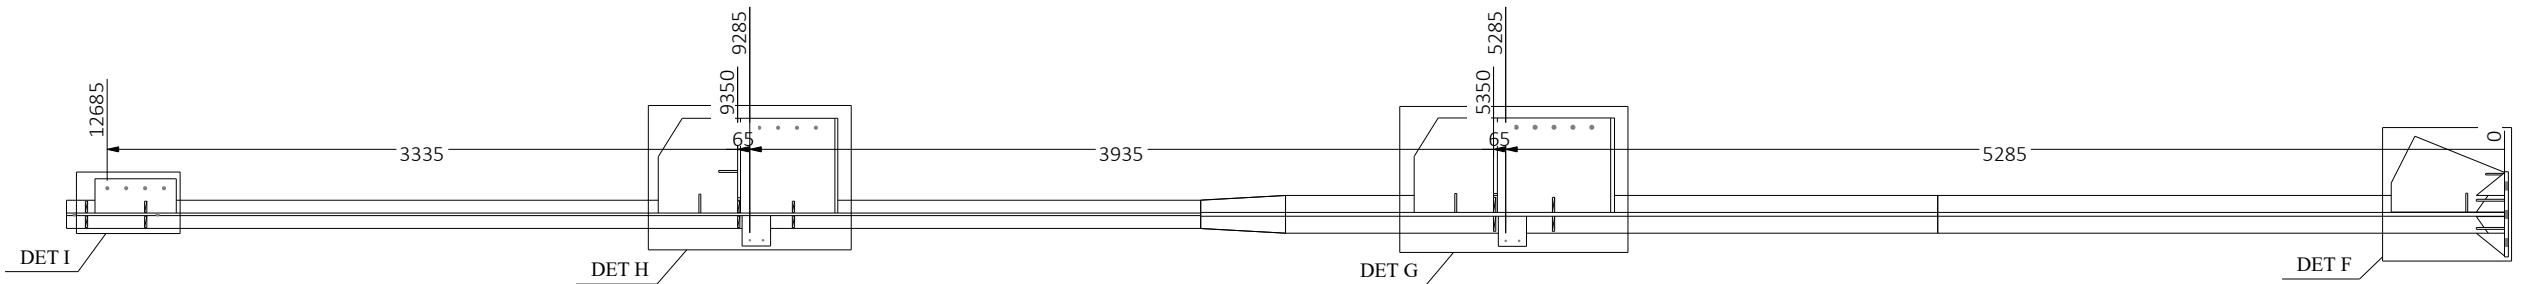


DETAIL I

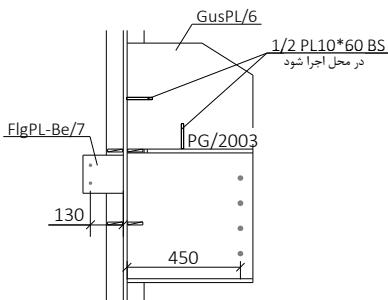


DETAIL H

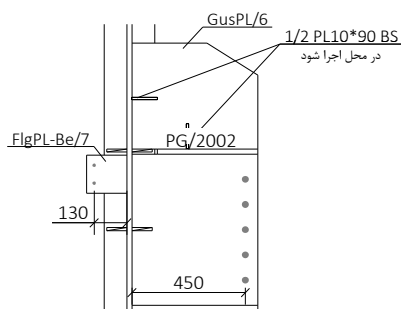





DETAIL G

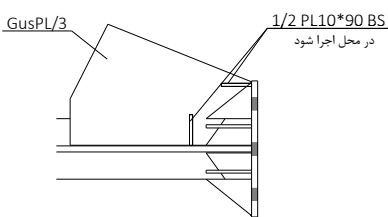


DETAIL F

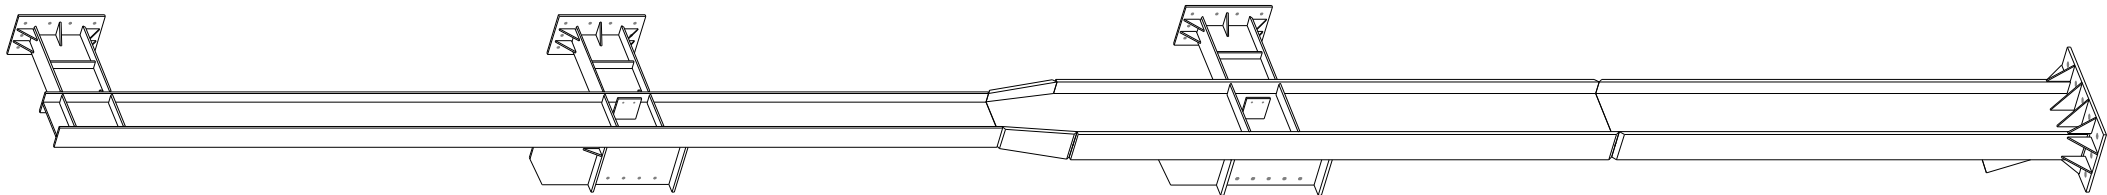





TITLE		ستون تکمیل		
CLIENT				
CONTRACTOR		ISSUED 04.03.		
MODELLED BY	EN ALMASI	SCALE	1:25 1:28	A3
DRAWING No	[C.13]	REVISION No.	0	

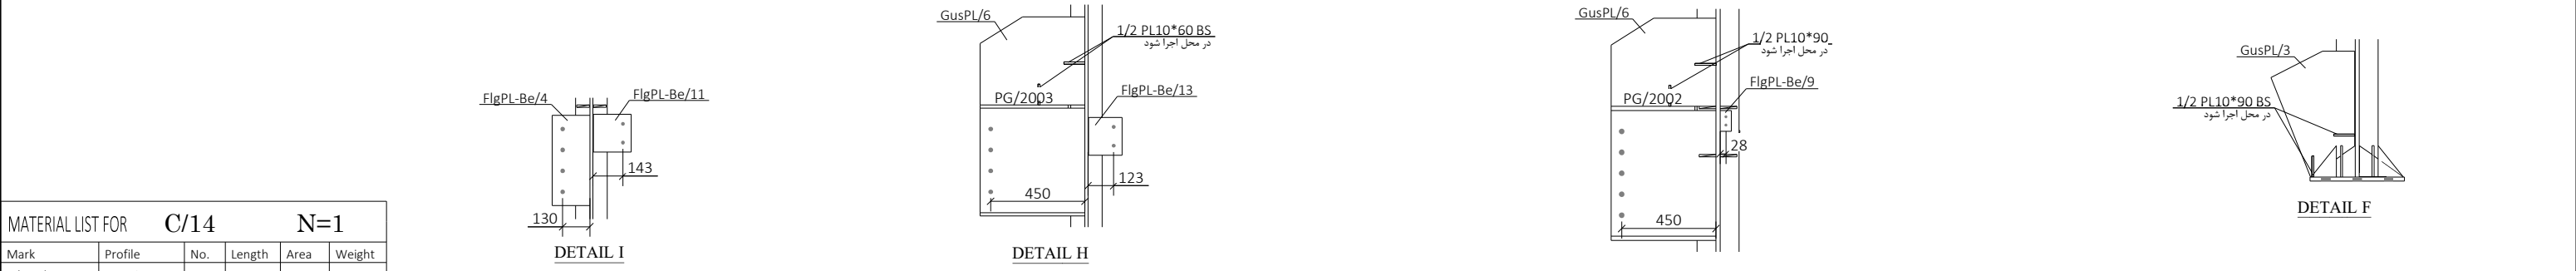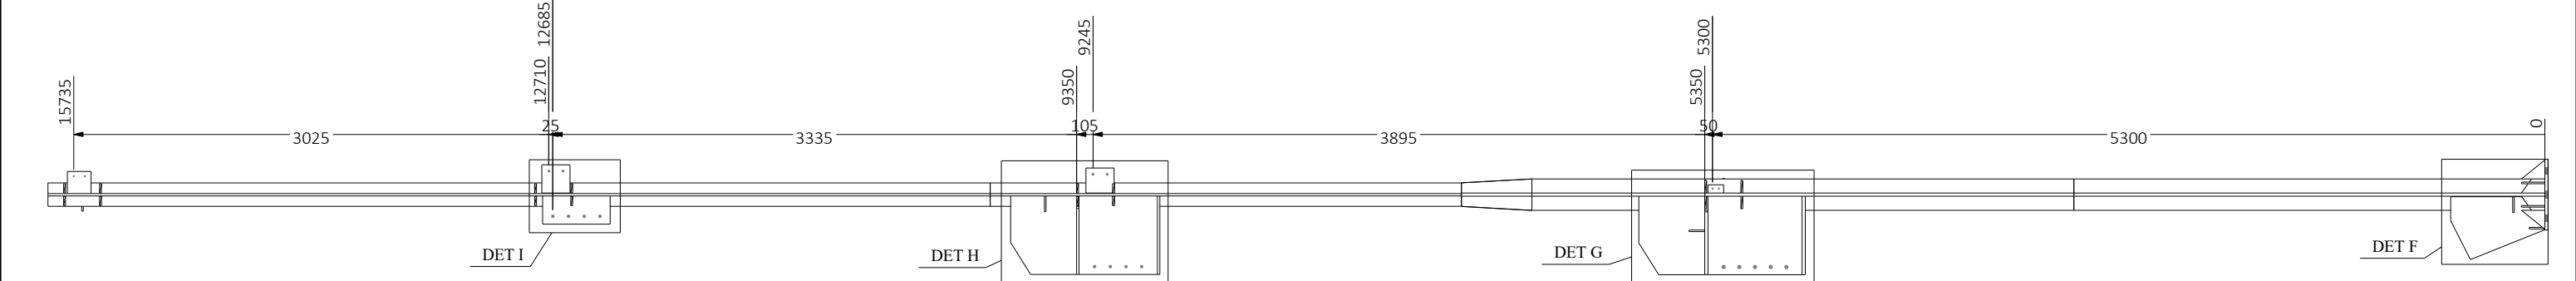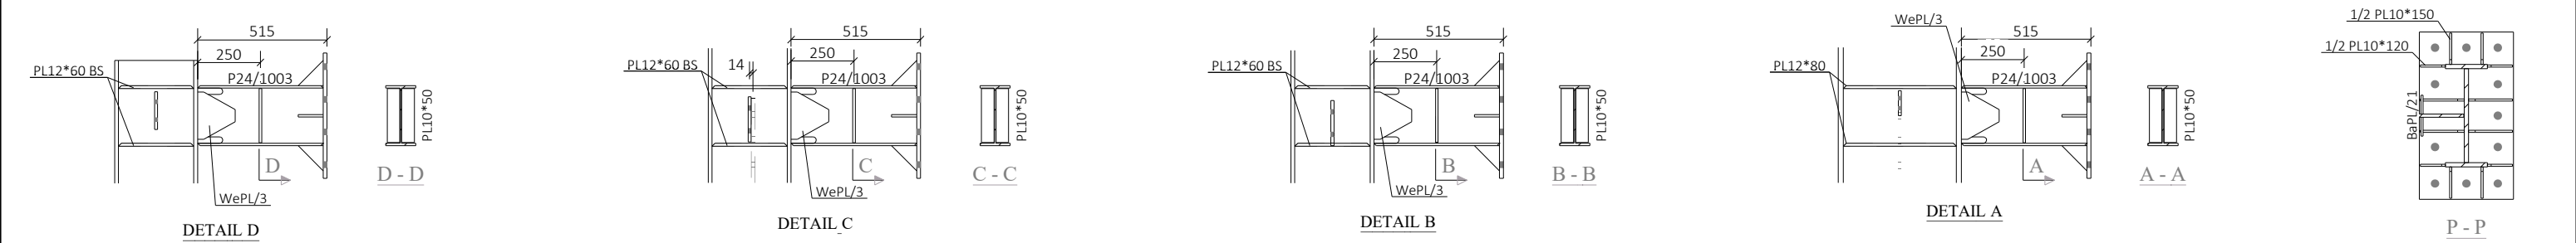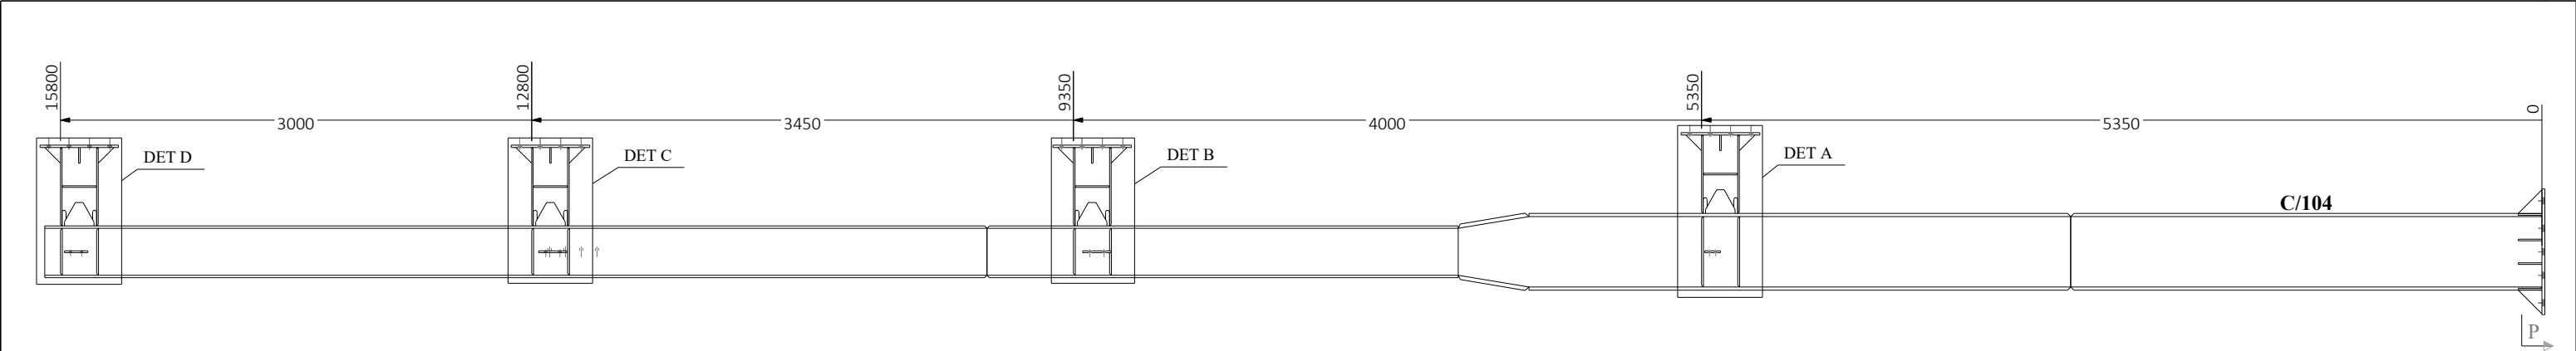


MATERIAL LIST FOR C/14 N=1					
Mark	Profile	No.	Length	Area	Weight
1/2PL/1002	PL10*120	4	150	0.0	0.7
1/2PL/1003	PL10*150	4	150	0.0	0.9
1/2PL/1004	PL10*150	4	210	0.0	1.2
1/2PL/1011	PL10*90	10	100	0.0	0.4
1/2PL/1012	PL10*60	2	100	0.0	0.2
BaPL/21	PL20*450	1	800	0.8	56.5
FlgPL-Be/4	PL15*180	1	430	0.2	9.1
FlgPL-Be/9	PL12*60	1	100	0.0	0.6
FlgPL-Be/10	PL12*140	1	150	0.0	2.0
FlgPL-Be/11	PL12*180	1	180	0.1	3.1
FlgPL-Be/13	PL12*160	1	180	0.1	2.7
GusPL/3	PL15*400	1	600	0.4	21.1
GusPL/6	PL15*420	2	500	0.4	23.2
Stf/8	PL12*80	4	450	0.1	3.3
Stf/9	PL12*60	12	300	0.0	1.6
Stf/15	PL10*50	8	215	0.0	0.8
WePL/3	PL8*150	4	188	0.0	1.2
C/104	Assembly	1		24.2	1550.7
P24/1003	Assembly	4		0.7	28.7
PG/2002	Assembly	1		1.0	56.5
PG/2003	Assembly	1		0.8	31.9
Total				33.1	1955.1

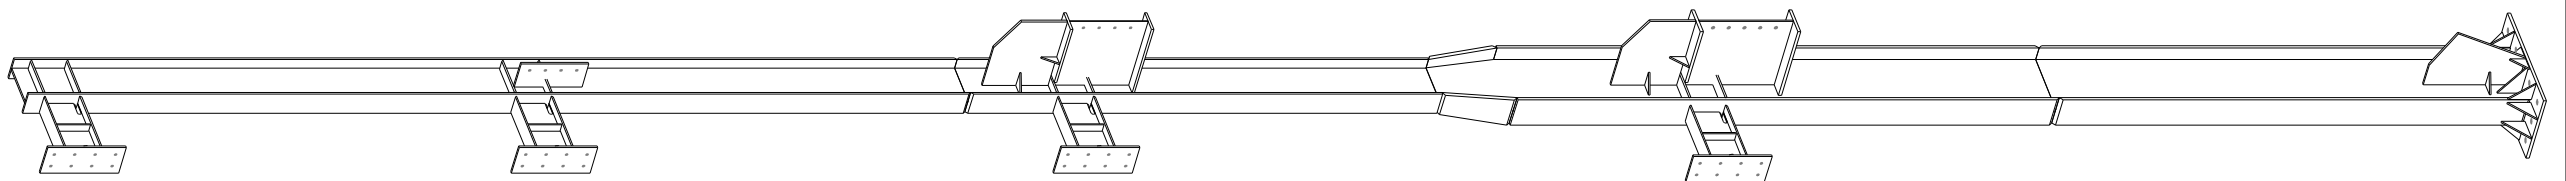

TITLE		ستون تکمیل		
CLIENT				
CONTRACTOR		ISSUED 04.03.		
MODELLED BY	EN ALMASI	SCALE	1:25 1:28	A3
DRAWING No	[C.14]	REVISION No.	0	

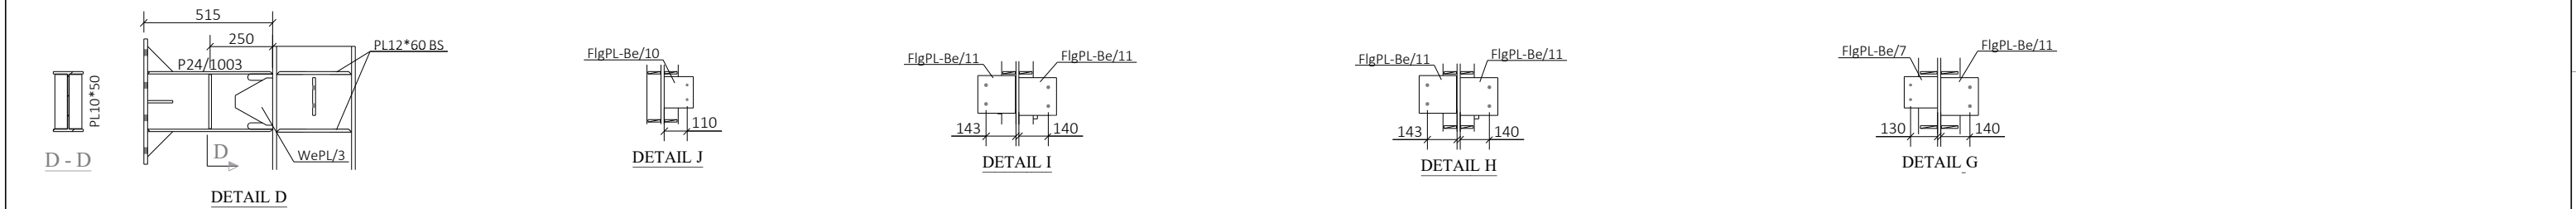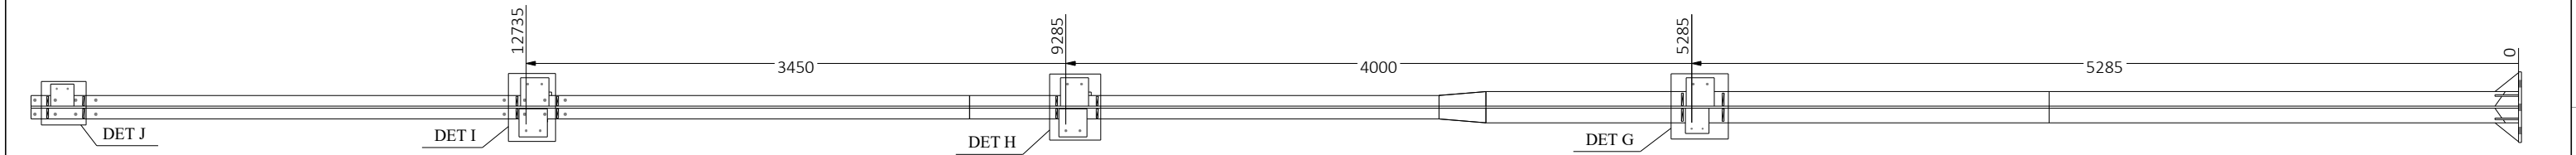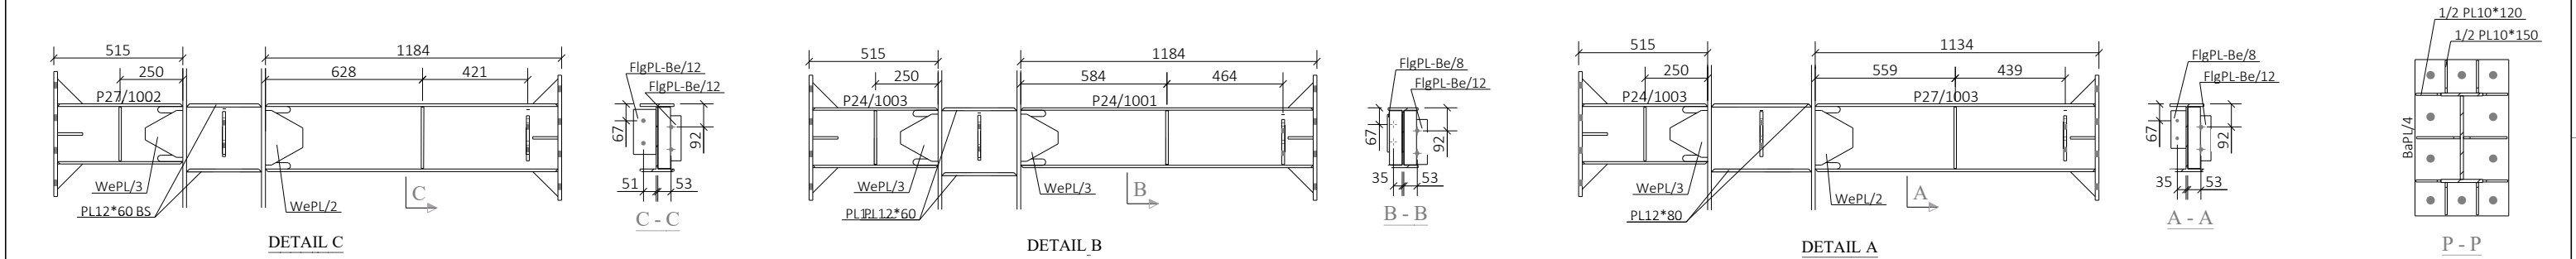
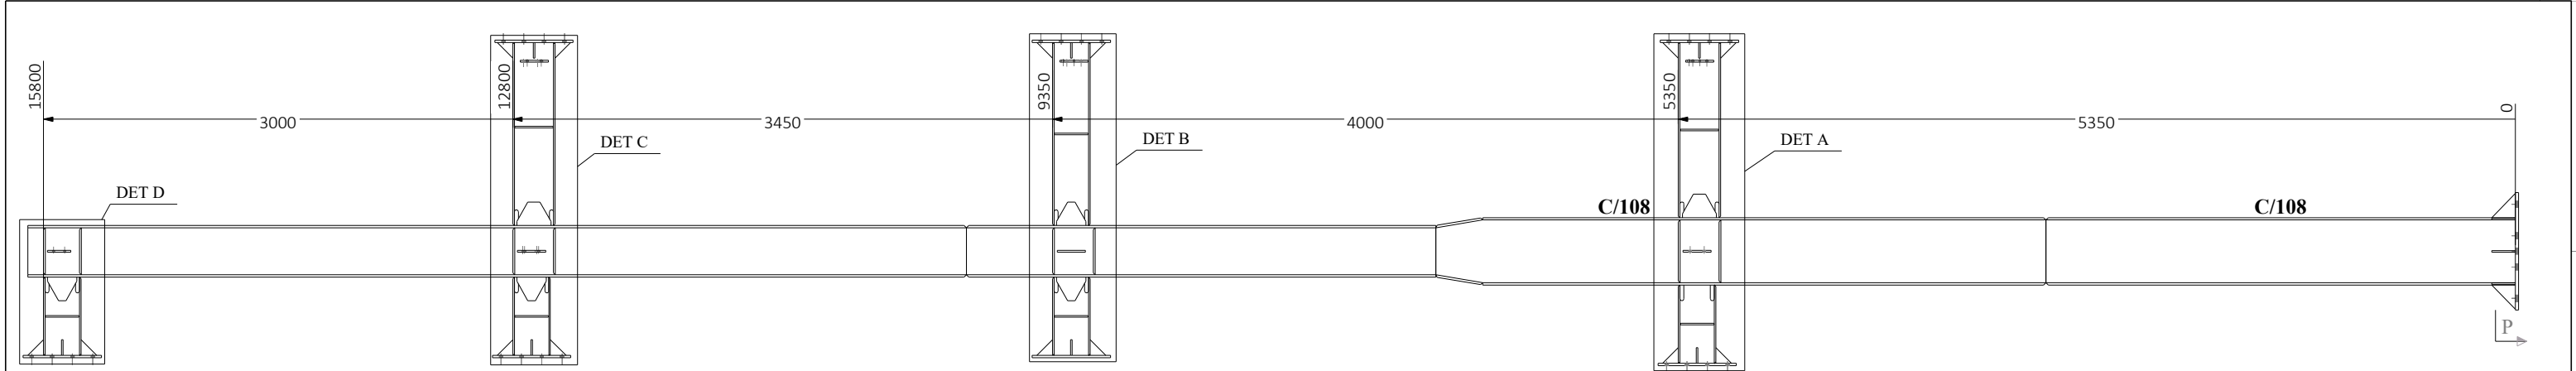


MATERIAL LIST FOR C/15 N=1					
Mark	Profile	No.	Length	Area	Weight
1/2PL/1002	PL10*120	4	150	0.0	0.7
1/2PL/1004	PL10*150	2	210	0.0	1.2
1/2PL/1008	PL10*150	4	155	0.0	0.9
BaPL/4	PL20*450	1	750	0.7	53.0
FlgPL-Be/7	PL12*160	1	150	0.1	2.3
FlgPL-Be/8	PL12*60	2	150	0.0	0.8
FlgPL-Be/10	PL12*140	1	150	0.0	2.0
FlgPL-Be/11	PL12*180	5	180	0.1	3.1
FlgPL-Be/12	PL12*90	4	180	0.0	1.5
Stf/7	PL12*80	4	400	0.1	2.9
Stf/9	PL12*60	12	300	0.0	1.6
Stf/15	PL10*50	10	215	0.0	0.8
Stf/16	PL10*50	2	245	0.0	1.0
WePL/2	PL8*150	2	218	0.1	1.5
WePL/3	PL8*150	5	188	0.0	1.2
C/108	Assembly	1	23.3	1280.4	
P24/1001	Assembly	1		1.4	49.2
P24/1003	Assembly	4		0.7	28.7
P27/1002	Assembly	1		1.5	55.4
P27/1003	Assembly	1		1.4	53.6
Total				33.7	1693.4

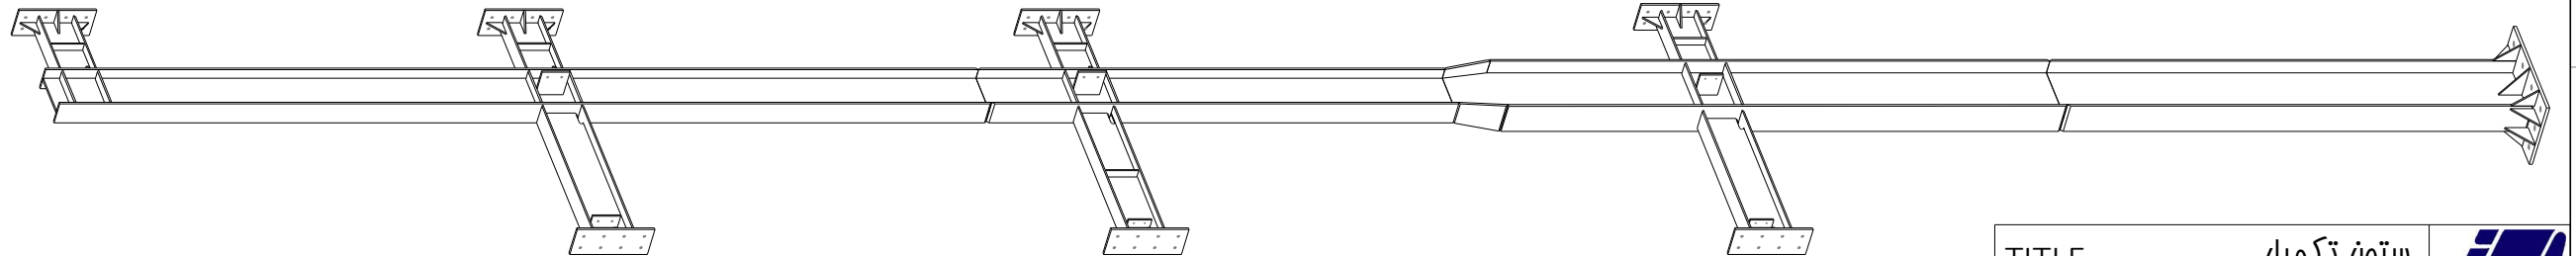


TITLE		ستون تکمیل		
CLIENT				
CONTRACTOR		ISSUED 04.03.		
MODELLED BY	EN ALMASI	SCALE 1:25	1:28	A3
DRAWING No	[C.15]	REVISION No.	0	



Tekla Structures

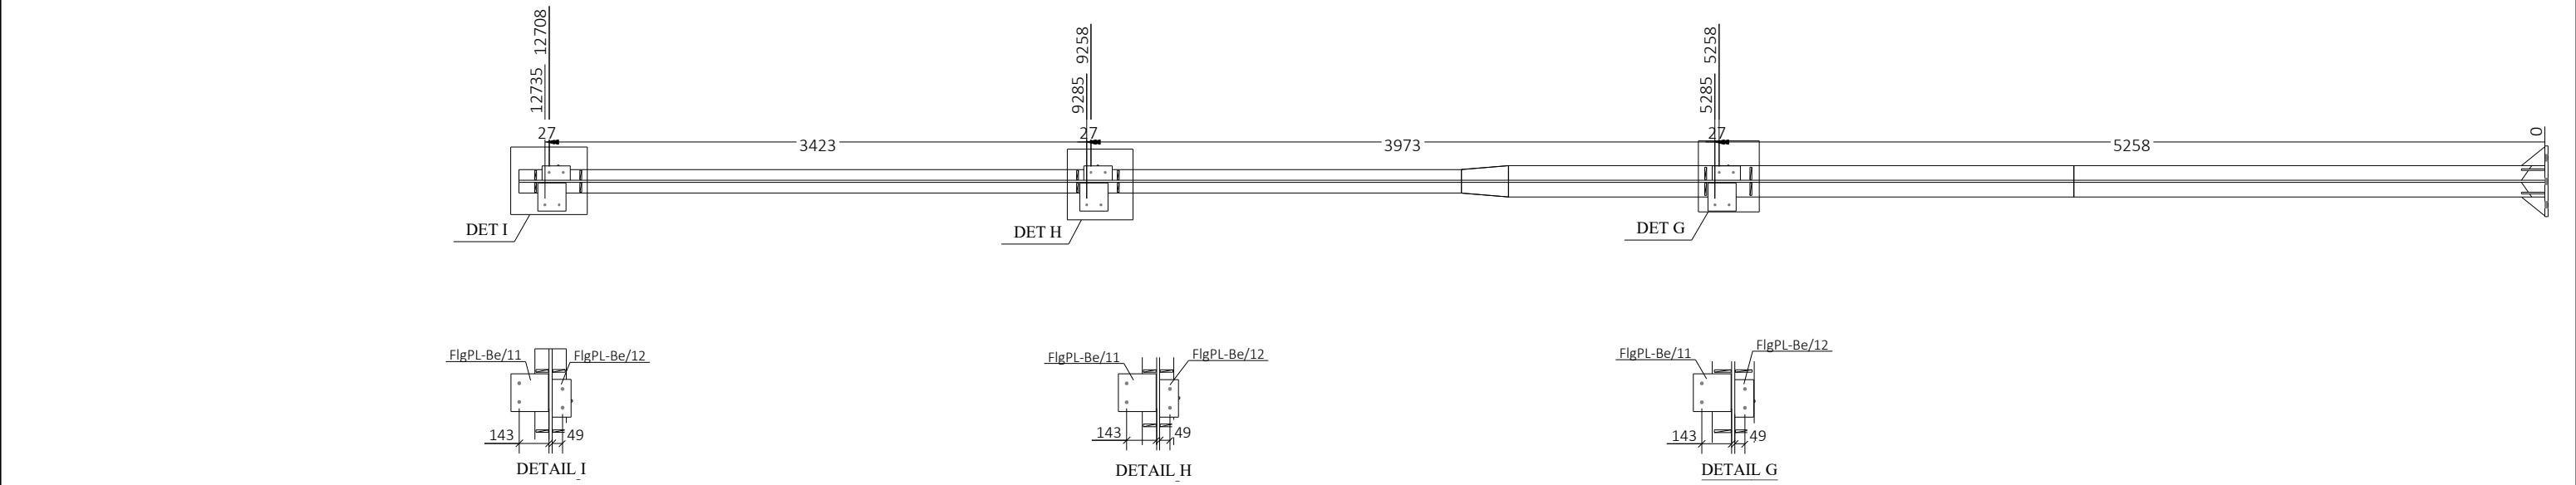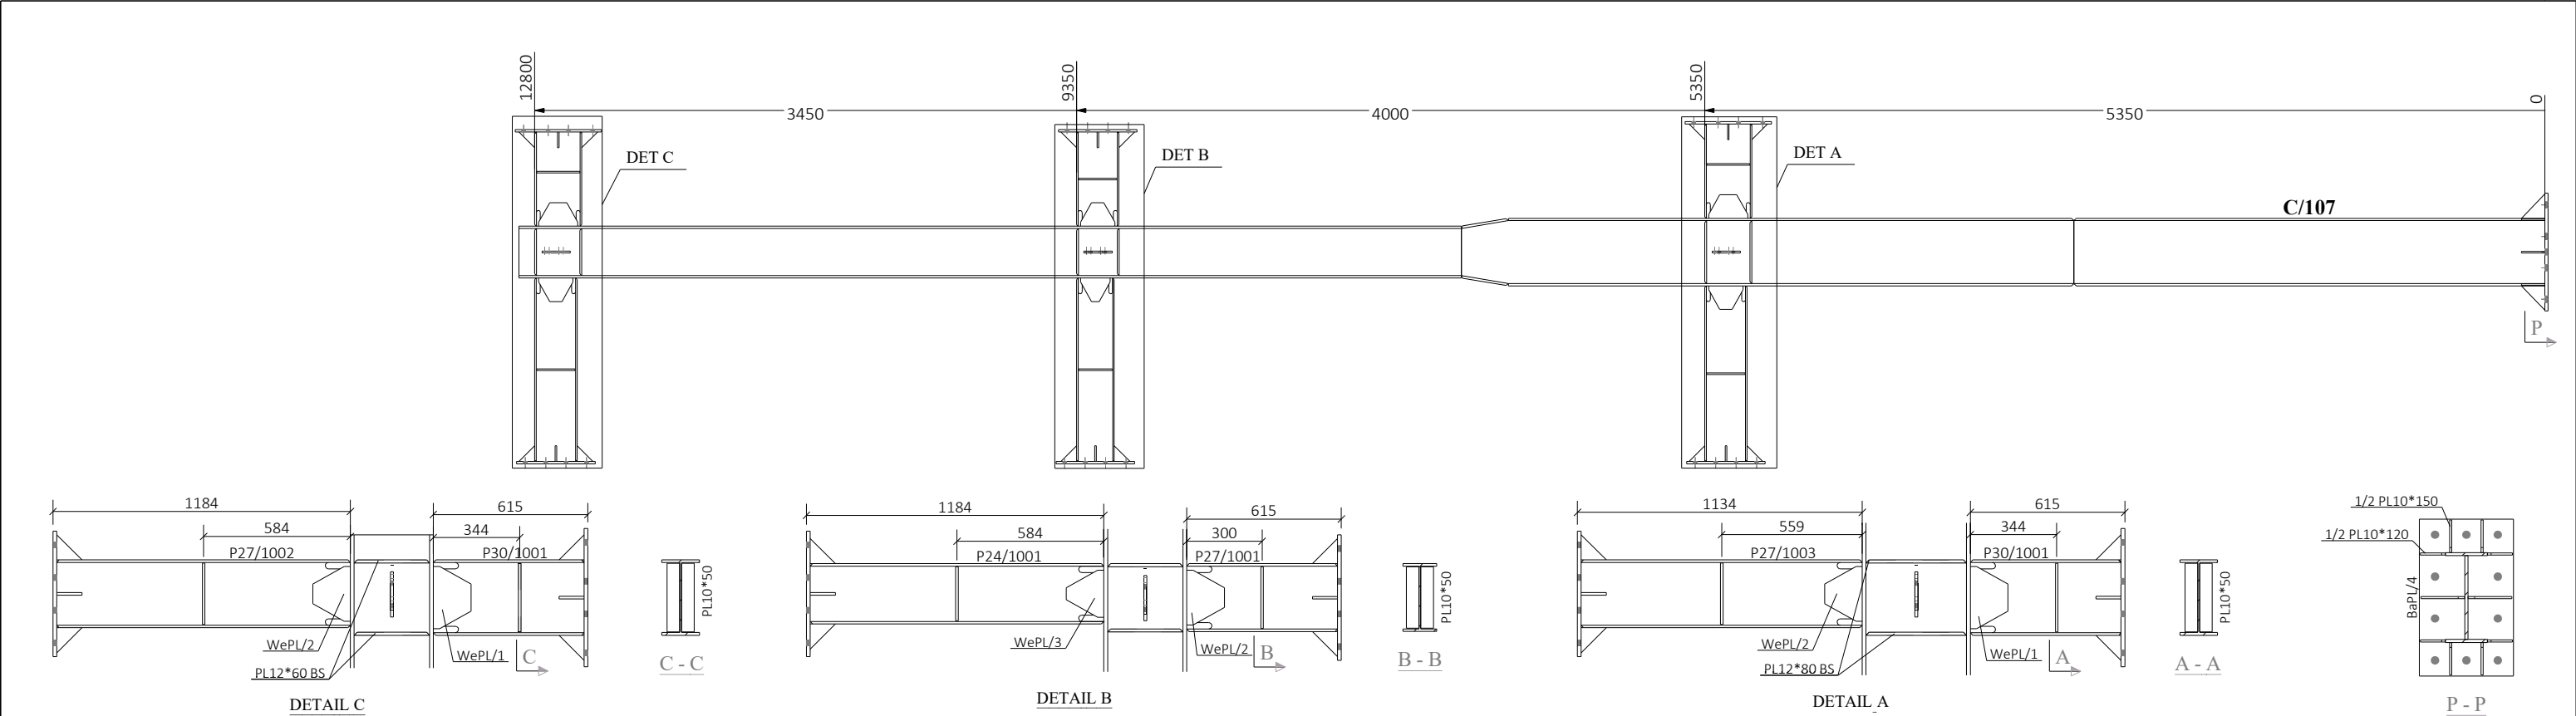


MATERIAL LIST FOR C/16 N=1					
Mark	Profile	No.	Length	Area	Weight
1/2PL/1002	PL10*120	4	150	0.0	0.7
1/2PL/1004	PL10*150	2	210	0.0	1.2
1/2PL/1008	PL10*150	4	155	0.0	0.9
BaPL/4	PL20*450	1	750	0.7	53.0
FlgPL-Be/11	PL12*180	3	180	0.1	3.1
FlgPL-Be/12	PL12*90	3	180	0.0	1.5
Stf/7	PL12*80	4	400	0.1	2.9
Stf/9	PL12*60	8	300	0.0	1.6
Stf/14	PL10*50	4	274	0.0	1.1
Stf/15	PL10*50	2	215	0.0	0.8
Stf/16	PL10*50	6	245	0.0	1.0
WePL/1	PL8*150	2	248	0.1	1.8
WePL/2	PL8*150	3	218	0.1	1.5
WePL/3	PL8*150	1	188	0.0	1.2
C/107	Assembly	1		19.4	1069.0
P24/1001	Assembly	1		1.4	49.2
P27/1001	Assembly	1		0.9	35.0
P27/1002	Assembly	1		1.5	55.4
P27/1003	Assembly	1		1.4	53.6
P30/1001	Assembly	2		1.1	47.1
Total				29.5	1477.9

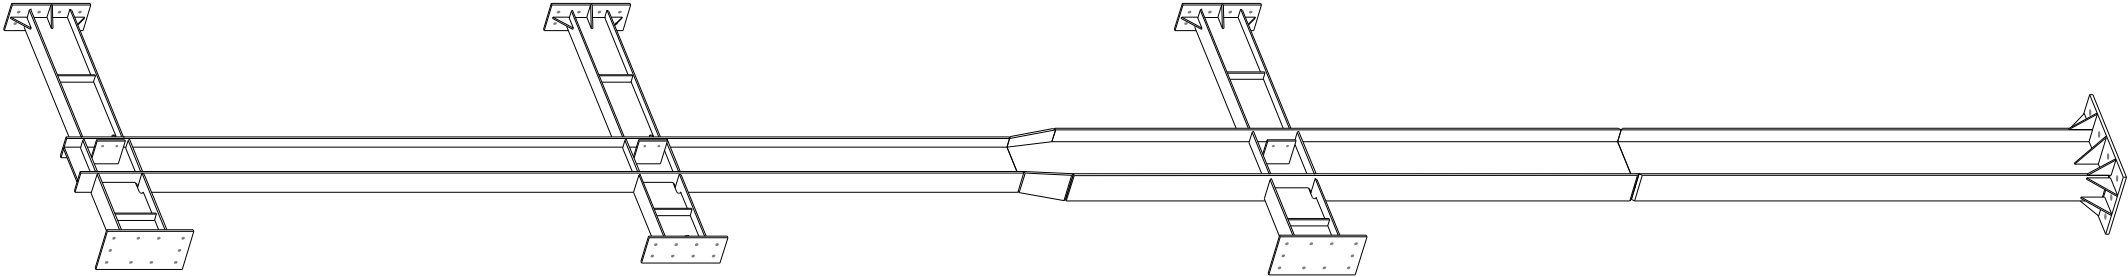


TITLE		ستون تکمیل		
CLIENT				
CONTRACTOR			ISSUED 04.03.	
MODELLED BY		EN ALMASI	SCALE 1:25 1:28	A3
DRAWING No		[C.16]	REVISION No. 0	

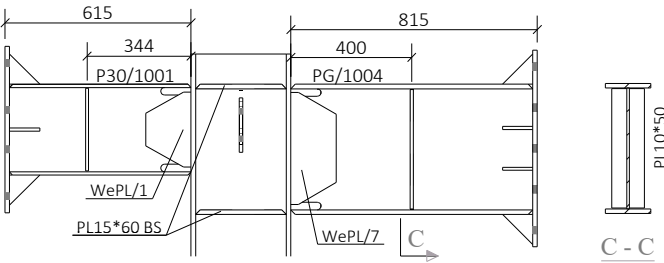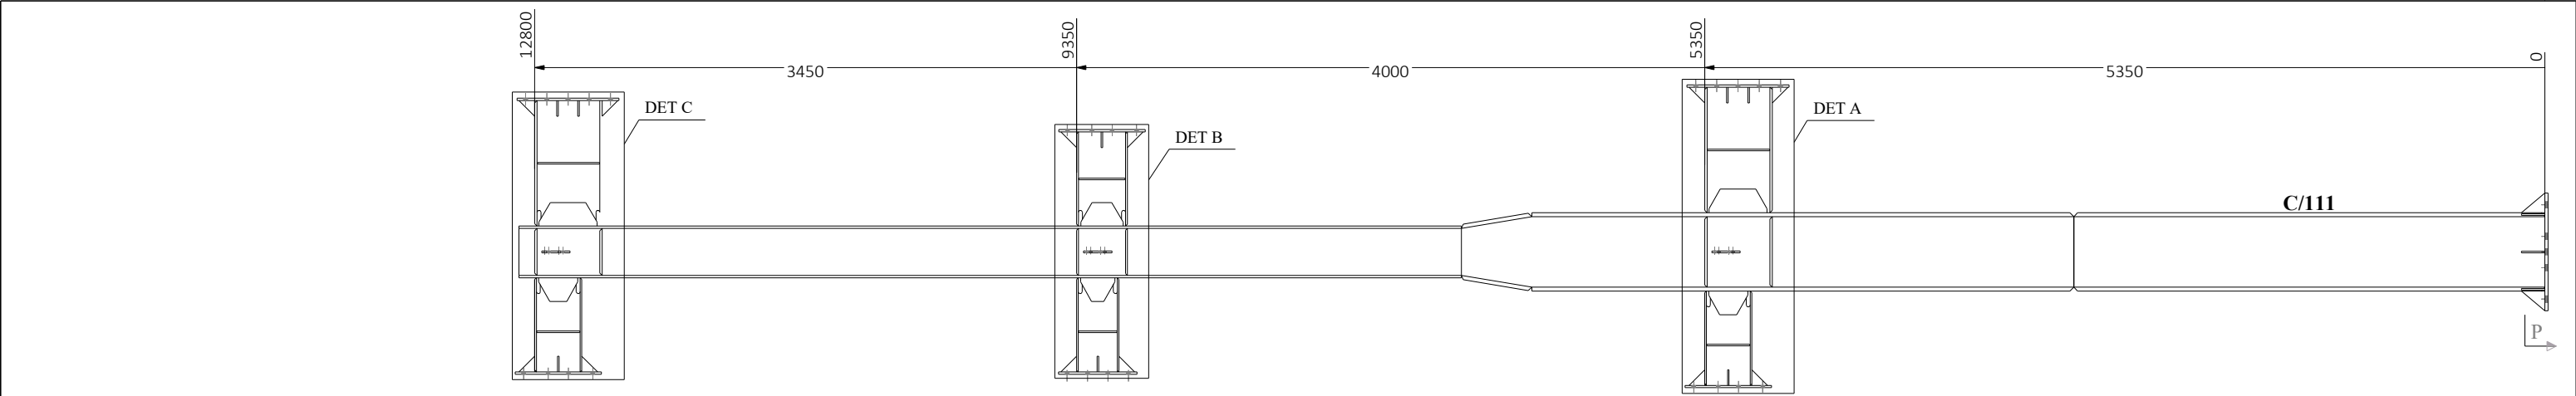


DETAIL C

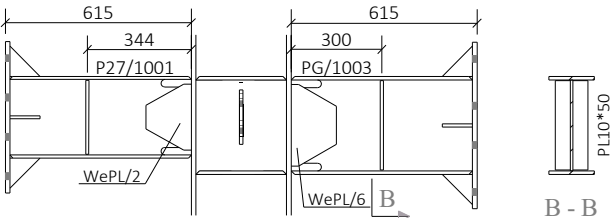



DETAIL B

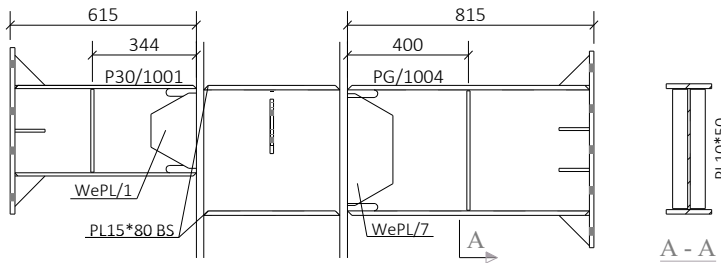


DETAIL A

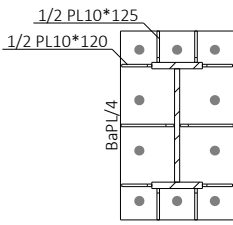


P - P

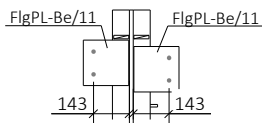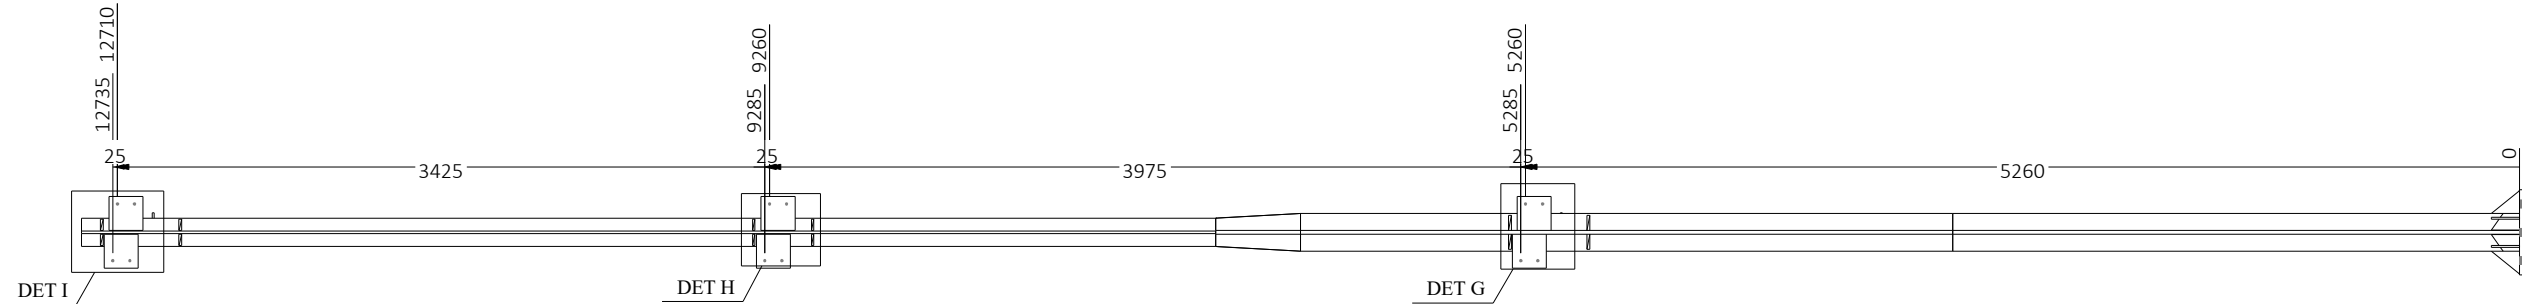

DETAIL I

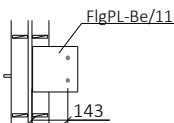


DETAIL H

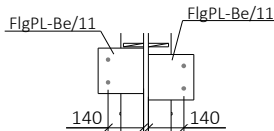


DETAIL G

MATERIAL LIST FOR C/17 N=1					
Mark	Profile	No.	Length	Area	Weight
1/2PL/1002	PL10*120	4	150	0.0	0.7
1/2PL/1004	PL10*150	2	210	0.0	1.2
1/2PL/1007	PL10*125	4	150	0.0	0.7
BaPL/4	PL20*450	1	750	0.7	53.0
FlgPL-Be/11	PL12*180	6	180	0.1	3.1
Stf/3	PL15*80	4	450	0.1	4.1
Stf/5	PL15*60	4	300	0.0	2.0
Stf/9	PL12*60	4	300	0.0	1.6
Stf/13	PL10*50	2	295	0.0	1.2
Stf/14	PL10*50	4	274	0.0	1.1
Stf/16	PL10*50	2	245	0.0	1.0
Stf/17	PL10*50	4	395	0.0	1.6
WePL/1	PL8*150	2	248	0.1	1.8
WePL/2	PL8*150	1	218	0.1	1.5
WePL/6	PL10*150	1	270	0.1	2.5
WePL/7	PL10*150	2	370	0.1	3.6
C/111	Assembly	1	20.4		1439.5
P27/1001	Assembly	1		0.9	35.0
P30/1001	Assembly	2		1.1	47.1
PG/1003	Assembly	1		1.2	49.4
PG/1004	Assembly	2		1.7	73.6
Total				31.2	1905.4

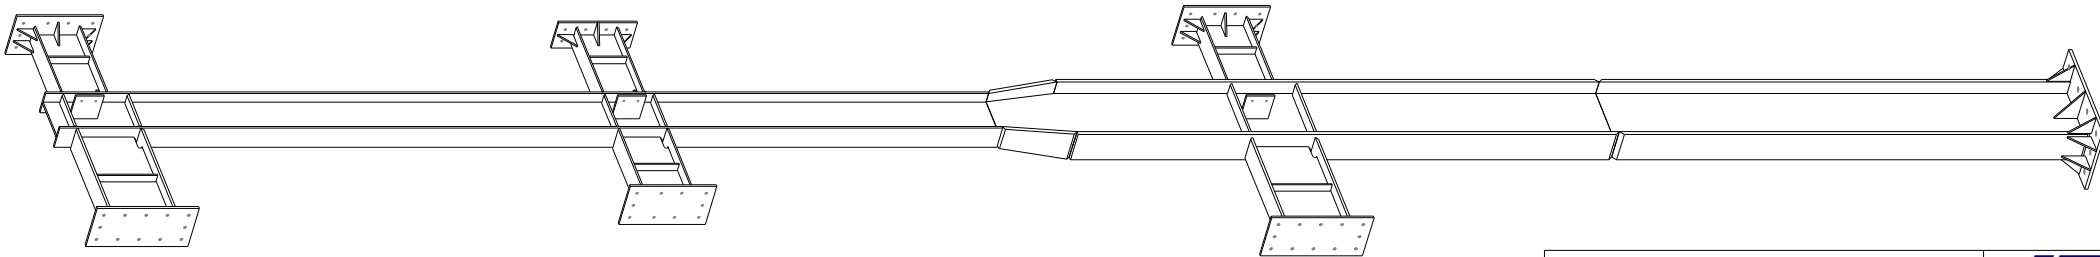




TITLE		ستون تکمیل		
CLIENT				
CONTRACTOR		ISSUED	04.03.	
MODELLED BY	EN ALMASI	SCALE	1:25	1:28
DRAWING No	[C.17]	REVISION No.	0	A3

MATERIAL LIST FOR C/18 N=1					
Mark	Profile	No.	Length	Area	Weight
1/2PL/1002	PL10*120	4	150	0.0	0.7
1/2PL/1003	PL10*150	4	150	0.0	0.9
1/2PL/1004	PL10*150	4	210	0.0	1.2
1/2PL/1011	PL10*90	10	100	0.0	0.4
1/2PL/1012	PL10*60	2	100	0.0	0.2
BaPL/21	PL20*450	1	800	0.8	56.5
FlgPL-Be/4	PL15*180	1	430	0.2	9.1
FlgPL-Be/11	PL12*180	2	180	0.1	3.1
FlgPL-Be/13	PL12*160	1	180	0.1	2.7
GusPL/3	PL15*400	1	600	0.4	21.1
GusPL/6	PL15*420	2	500	0.4	23.2
Stf/3	PL15*80	4	450	0.1	4.1
Stf/5	PL15*60	4	300	0.0	2.0
Stf/9	PL12*60	4	300	0.0	1.6
Stf/13	PL10*50	2	295	0.0	1.2
Stf/17	PL10*50	4	395	0.0	1.6
WePL/6	PL10*150	1	270	0.1	2.5
WePL/7	PL10*150	2	370	0.1	3.6
C/111	Assembly	1	20.4	1439.5	
PG/1003	Assembly	1	1.2	49.4	
PG/1004	Assembly	2	1.7	73.6	
PG/2002	Assembly	1	1.0	56.5	
PG/2003	Assembly	1	0.8	31.9	
Total			31.0	1931.2	

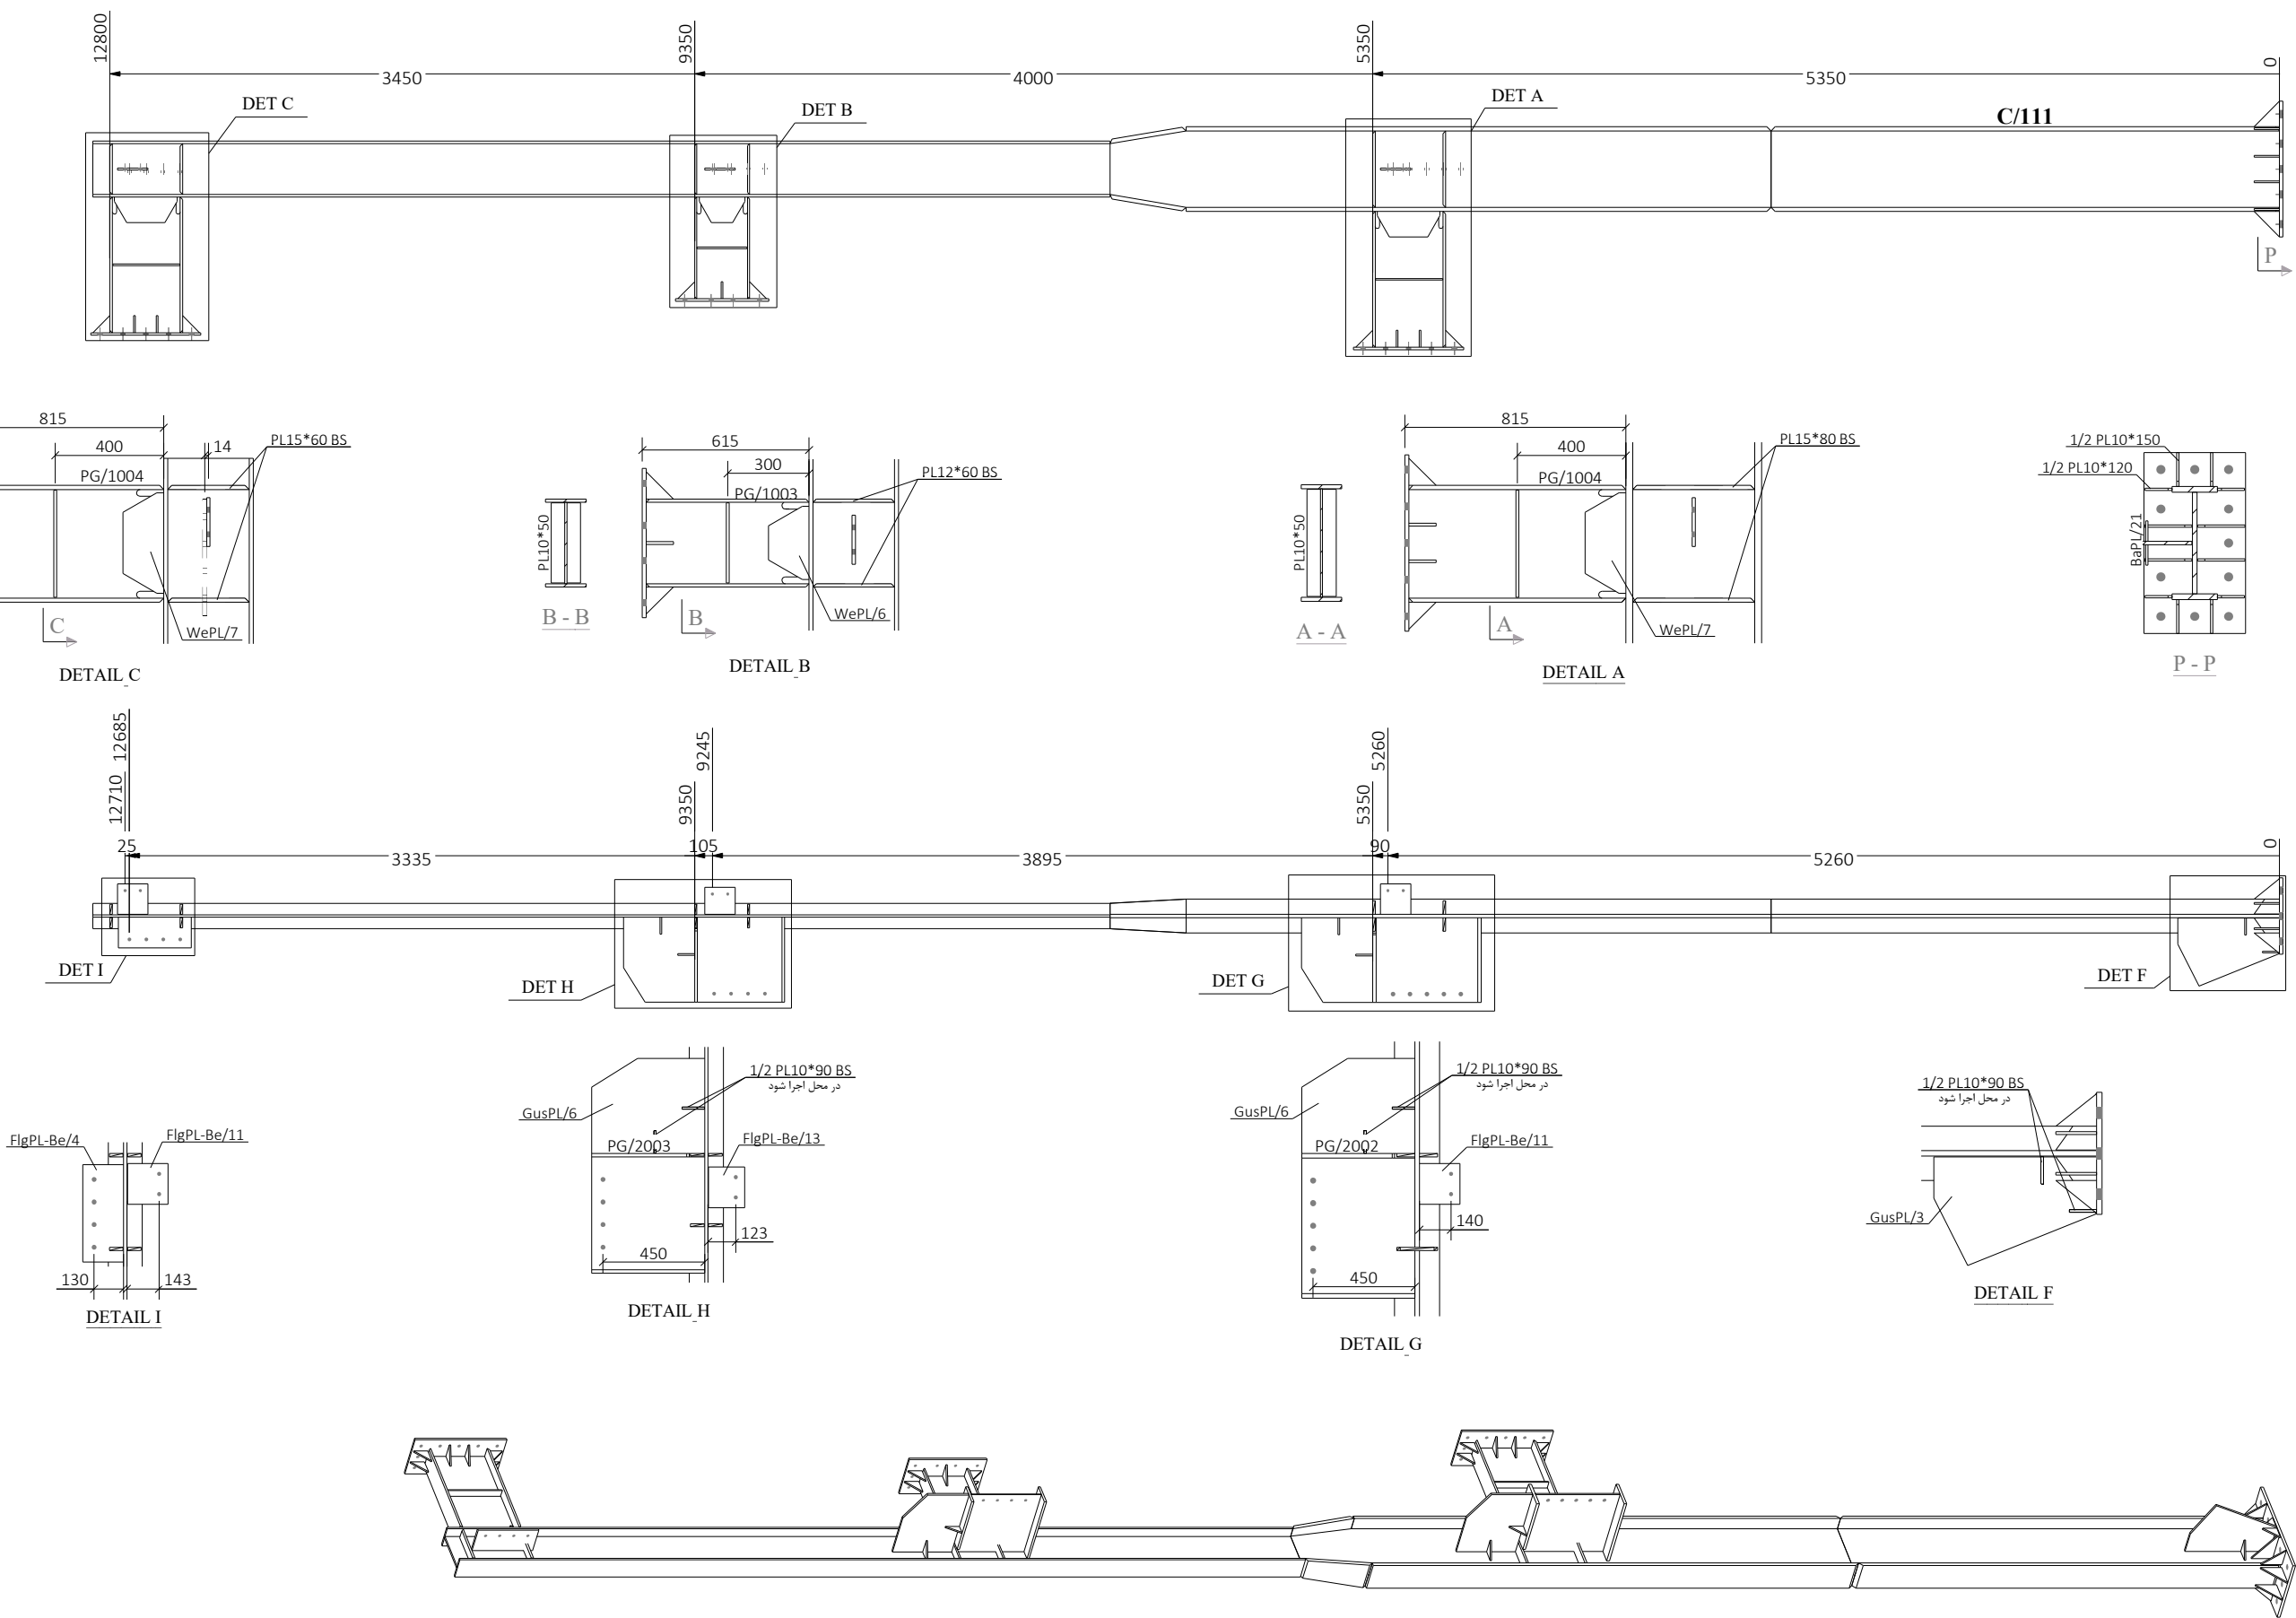

TITLE		ستون تکمیل		
CLIENT				
CONTRACTOR		ISSUED 04.03.		
MODELLED BY	EN ALMASI	SCALE	1:25 1:28	A3
DRAWING No	[C.18]	REVISION No.	0	





Tekla Structures

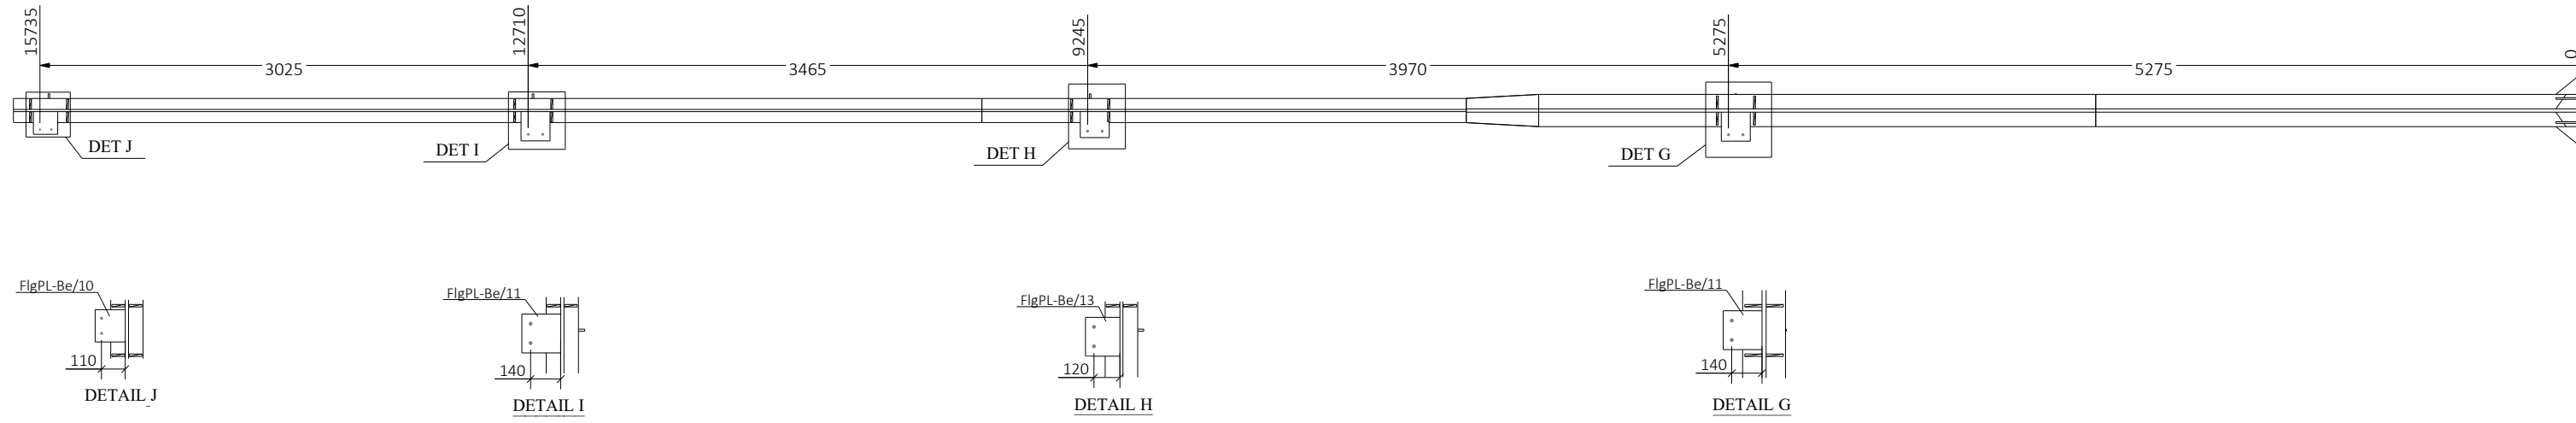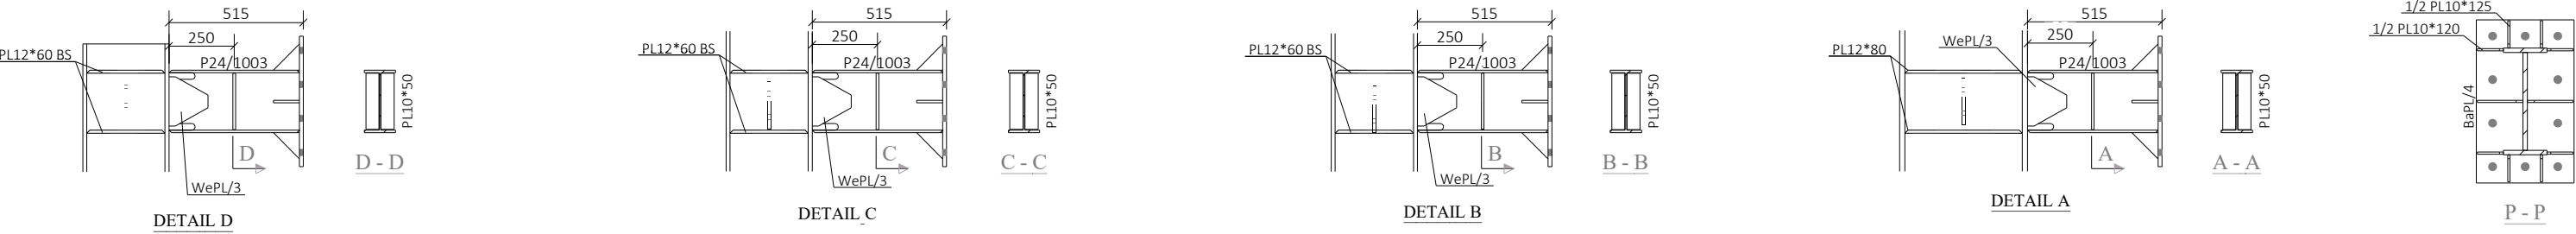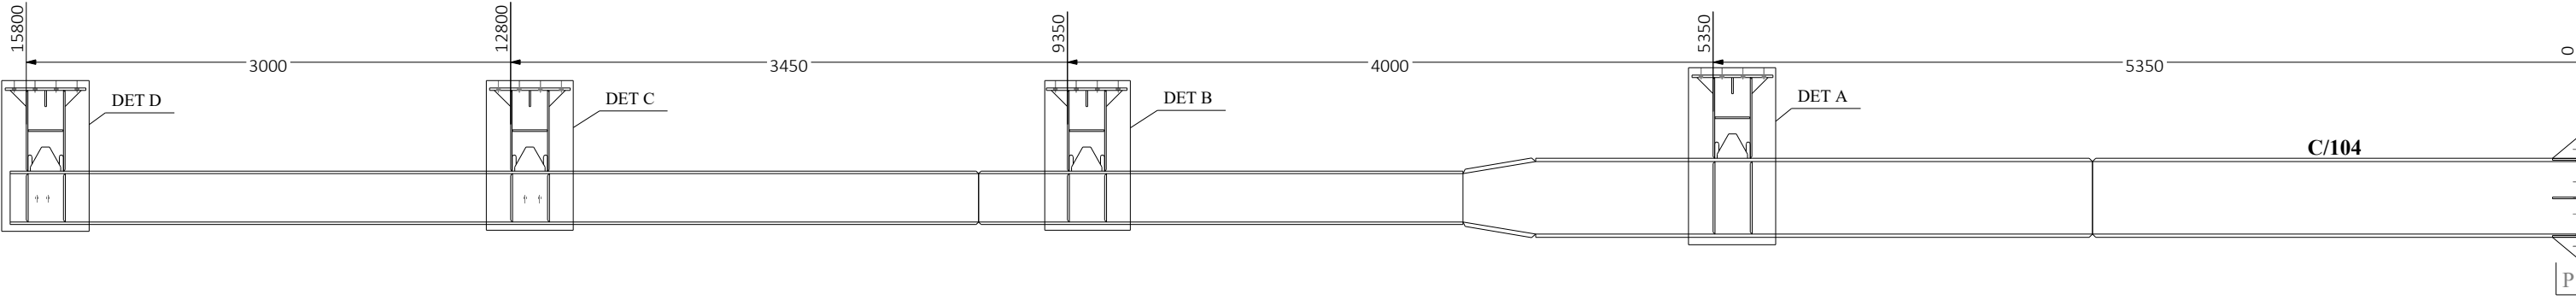

MATERIAL LIST FOR C/21 N=1					
Mark	Profile	No.	Length	Area	Weight
1/2PL/1002	PL10*120	4	150	0.0	0.7
1/2PL/1004	PL10*150	2	210	0.0	1.2
1/2PL/1007	PL10*125	4	150	0.0	0.7
BaPL/4	PL20*450	1	750	0.7	53.0
FlgPL-Be/10	PL12*140	1	150	0.0	2.0
FlgPL-Be/11	PL12*180	2	180	0.1	3.1
FlgPL-Be/13	PL12*160	1	180	0.1	2.7
Stf/8	PL12*80	4	450	0.1	3.3
Stf/9	PL12*60	12	300	0.0	1.6
Stf/15	PL10*50	8	215	0.0	0.8
WePL/3	PL8*150	4	188	0.0	1.2
C/104	Assembly	1		24.2	1550.7
P24/1003	Assembly	4		0.7	28.7
Total				29.6	1781.9





TITLE		ستون تکمیل		
CLIENT				
CONTRACTOR		ISSUED 04.03.		
MODELLED BY	EN ALMASI	SCALE 1:25	1:28	
DRAWING No	[C.21]	REVISION No.	0	
				A3

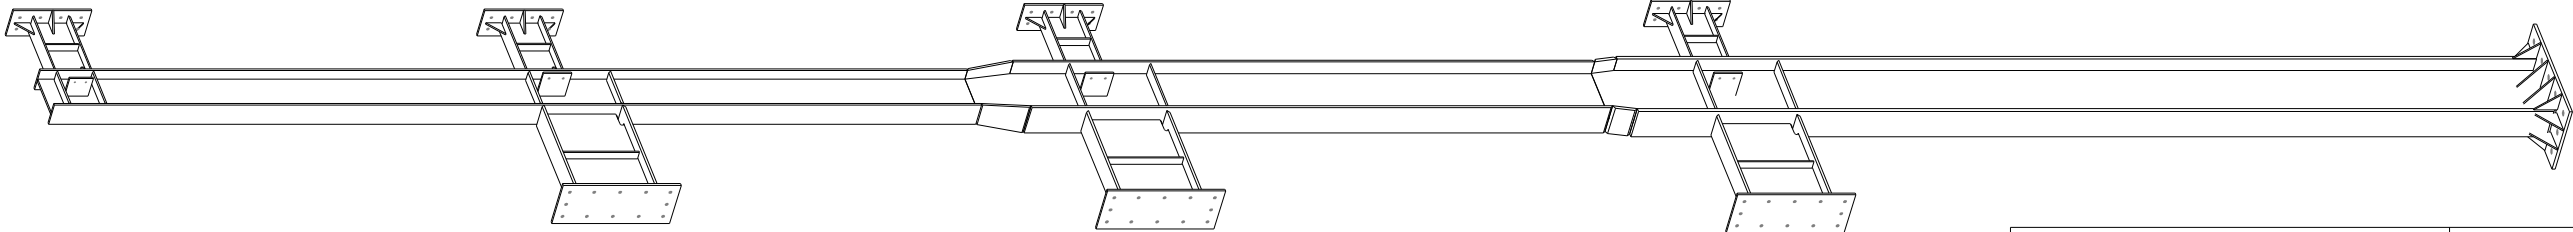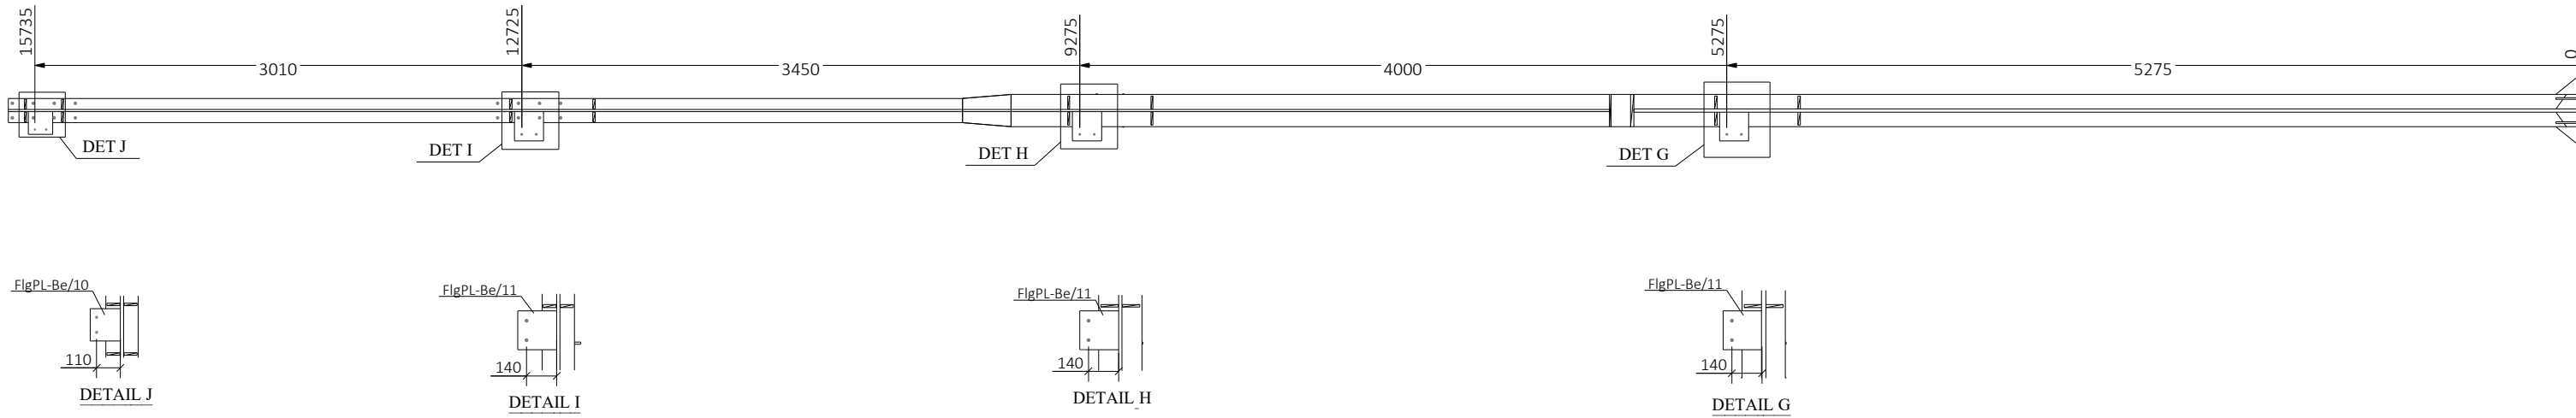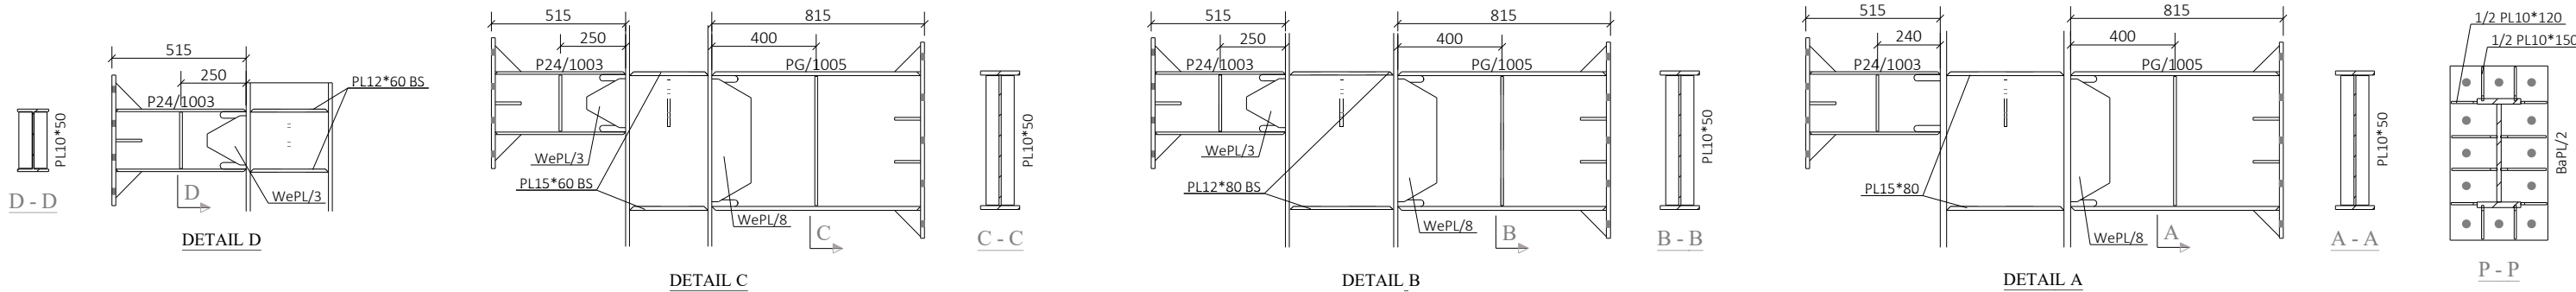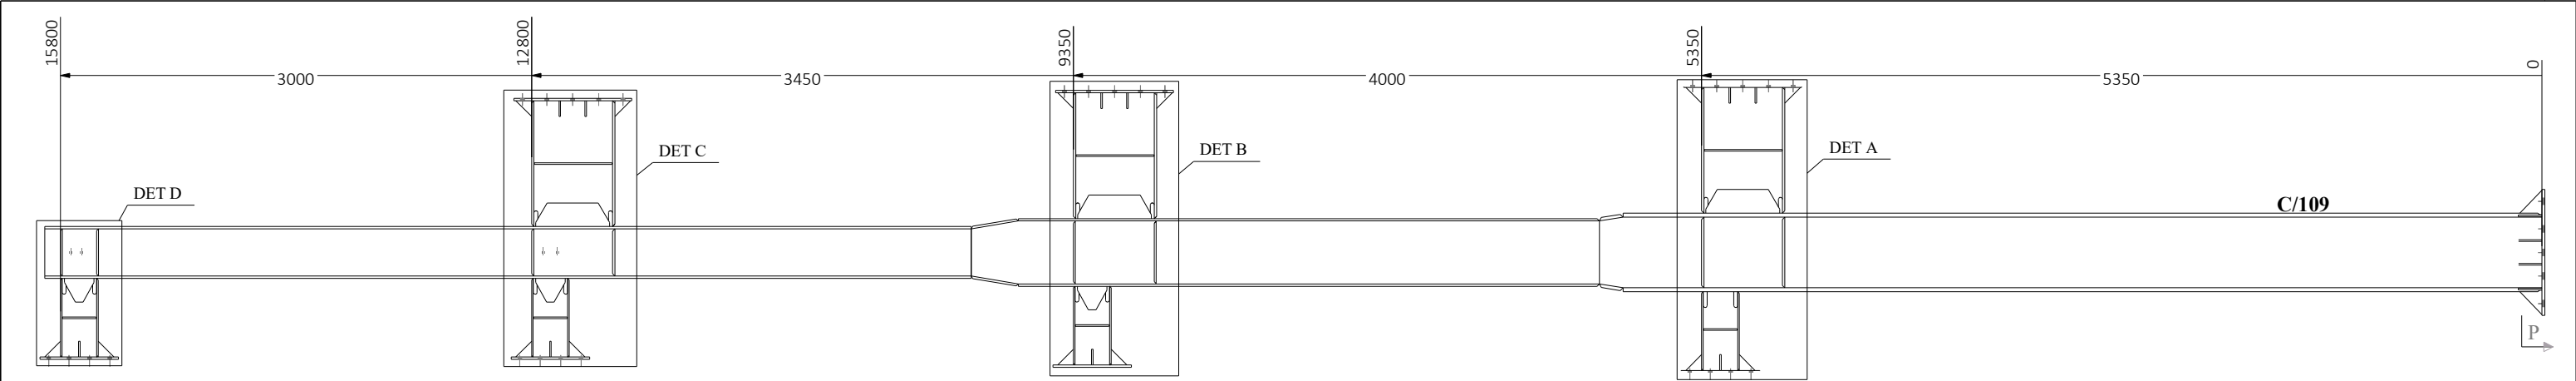


MATERIAL LIST FOR C/22 N=1					
Mark	Profile	No.	Length	Area	Weight
1/2PL/1002	PL10*120	4	150	0.0	0.7
1/2PL/1004	PL10*150	4	210	0.0	1.2
1/2PL/1008	PL10*150	4	155	0.0	0.9
BaPL/2	PL20*450	1	800	0.8	56.5
FlgPL-Be/10	PL12*140	1	150	0.0	2.0
FlgPL-Be/11	PL12*180	3	180	0.1	3.1
Stf/3	PL15*80	4	450	0.1	4.1
Stf/5	PL15*60	2	300	0.0	2.0
Stf/6	PL15*60	2	303	0.0	2.0
Stf/9	PL12*60	4	300	0.0	1.6
Stf/10	PL12*80	4	394	0.1	2.9
Stf/15	PL10*50	8	215	0.0	0.8
Stf/18	PL10*50	6	495	0.1	1.9
WePL/3	PL8*150	4	188	0.0	1.2
WePL/8	PL10*150	3	470	0.1	4.8
C/109	Assembly	1		25.4	1679.6
P24/1003	Assembly	4		0.7	28.7
PG/1005	Assembly	3		1.9	82.2
Total			37.7		2200.3


TITLE		ستون تکمیل		
CLIENT				
CONTRACTOR		ISSUED 04.03.		
MODELLED BY		EN ALMASI		A3
DRAWING No		[C.22]		
		SCALE 1:25 1:28		
		REVISION No. 0		

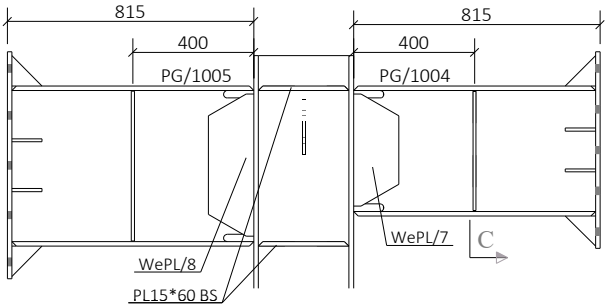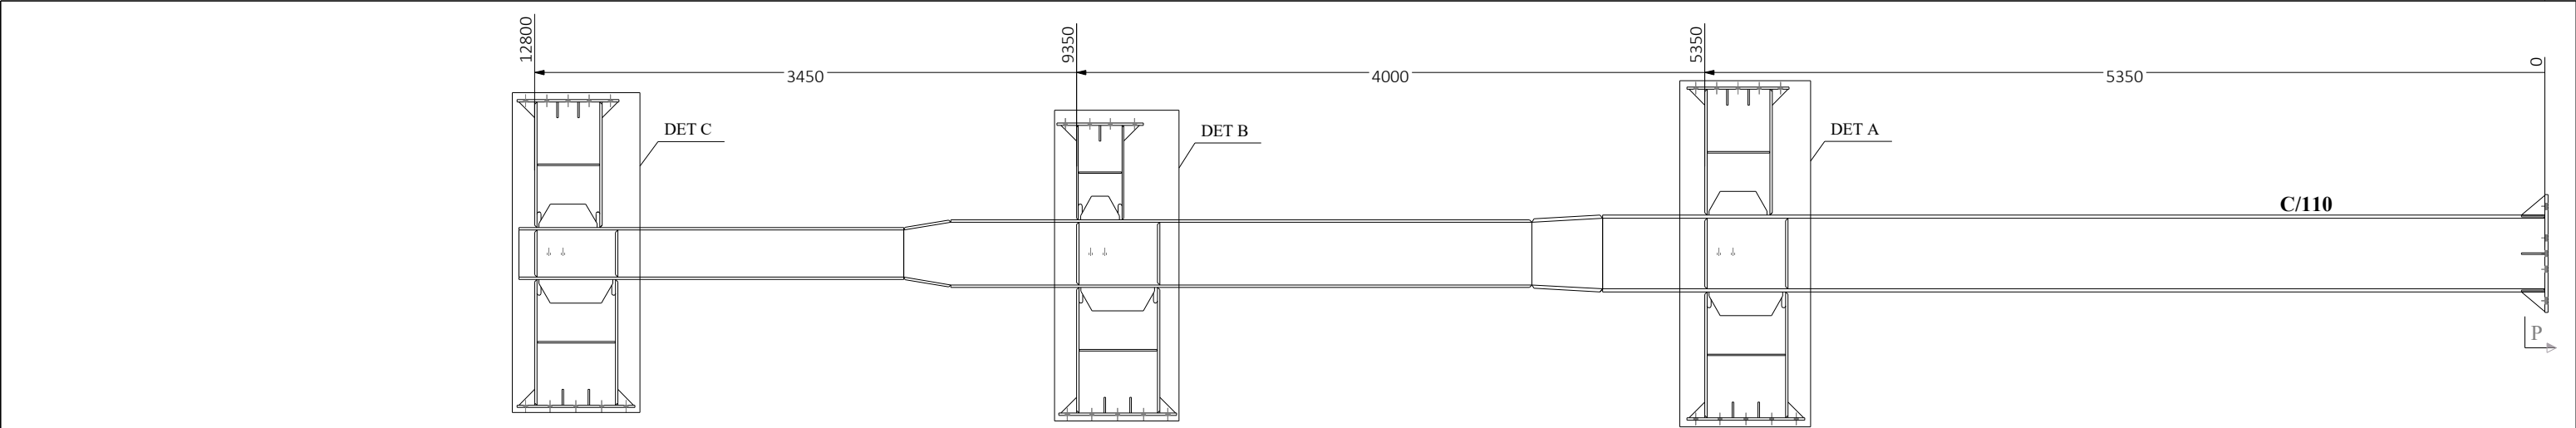


DETAIL_C

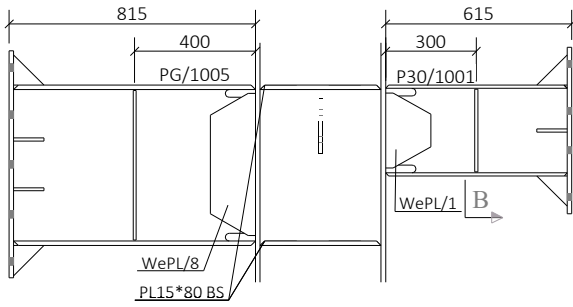



DETAIL_B

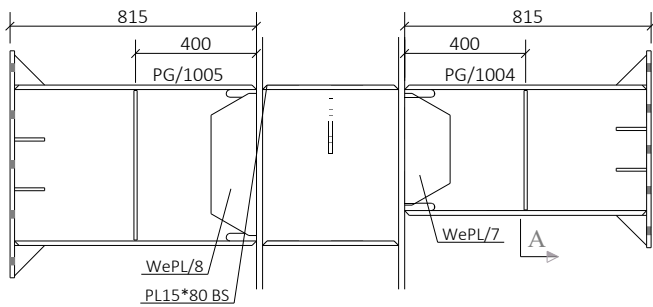


DETAIL_A

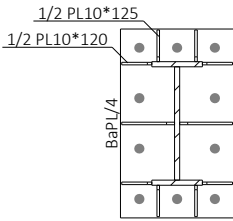


P - P

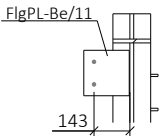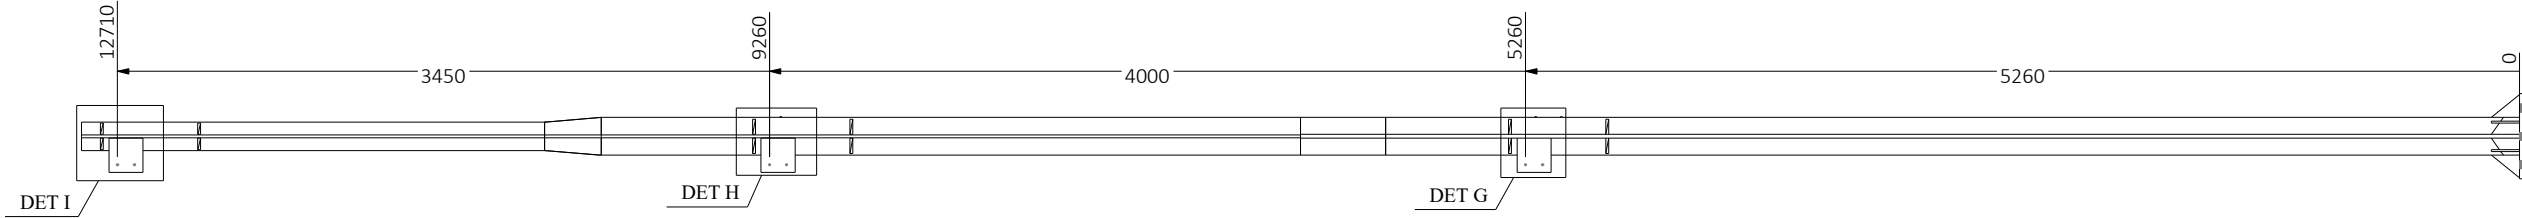


DETAIL_I

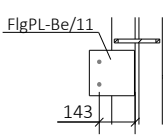

DETAIL_H

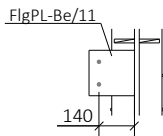


DETAIL_G

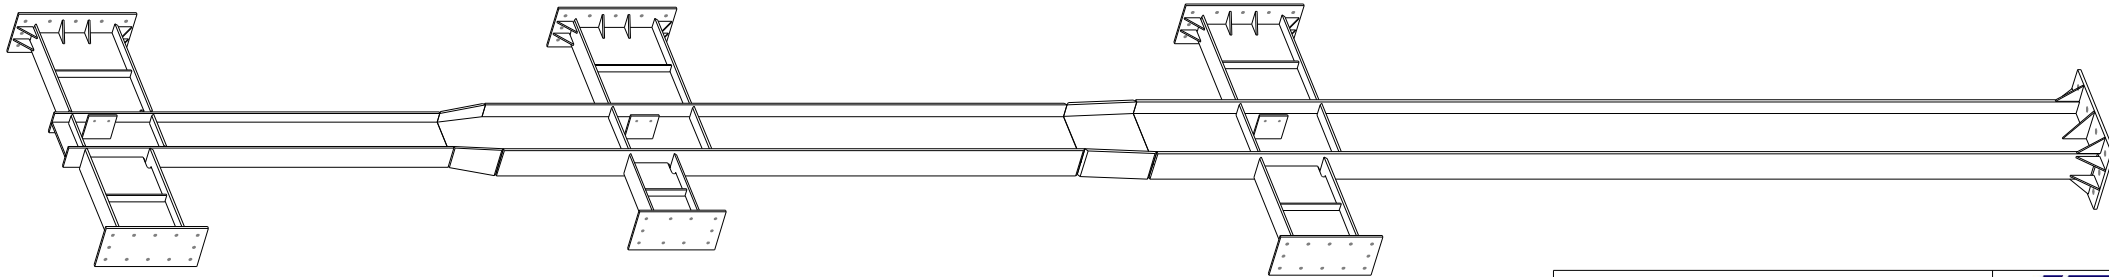

MATERIAL LIST FOR C/23 N=1					
Mark	Profile	No.	Length	Area	Weight
1/2PL/1002	PL10*120	4	150	0.0	0.7
1/2PL/1004	PL10*150	2	210	0.0	1.2
1/2PL/1007	PL10*125	4	150	0.0	0.7
BaPL/4	PL20*450	1	750	0.7	53.0
FlgPL-Be/11	PL12*180	3	180	0.1	3.1
Stf/3	PL15*80	4	450	0.1	4.1
Stf/4	PL15*80	4	400	0.1	3.6
Stf/5	PL15*60	4	300	0.0	2.0
Stf/14	PL10*50	2	274	0.0	1.1
Stf/17	PL10*50	4	395	0.0	1.6
Stf/18	PL10*50	6	495	0.1	1.9
WePL/1	PL8*150	1	248	0.1	1.8
WePL/7	PL10*150	2	370	0.1	3.6
WePL/8	PL10*150	3	470	0.1	4.8
C/110	Assembly	1		21.7	1403.2
P30/1001	Assembly	1		1.1	47.1
PG/1004	Assembly	2		1.7	73.6
PG/1005	Assembly	3		1.9	82.2
Total				35.3	1997.0

TITLE		ستون تکمیل		
CLIENT				
CONTRACTOR		ISSUED 04.03.		
MODELLED BY	EN ALMASI	SCALE 1:25	1:28	A3
DRAWING No	[C.23]	REVISION No. 0		

MATERIAL LIST FOR C/24 N=1					
Mark	Profile	No.	Length	Area	Weight
1/2PL/1002	PL10*120	4	150	0.0	0.7
1/2PL/1004	PL10*150	2	210	0.0	1.2
1/2PL/1008	PL10*150	4	155	0.0	0.9
BaPL/4	PL20*450	1	750	0.7	53.0
FlgPL-Be/11	PL12*180	2	180	0.1	3.1
FlgPL-Be/13	PL12*160	1	180	0.1	2.7
Stf/4	PL15*80	4	400	0.1	3.6
Stf/5	PL15*60	4	300	0.0	2.0
Stf/9	PL12*60	4	300	0.0	1.6
Stf/14	PL10*50	2	274	0.0	1.1
Stf/17	PL10*50	4	395	0.0	1.6
WePL/1	PL8*150	1	248	0.1	1.8
WePL/7	PL10*150	2	370	0.1	3.6
C/107	Assembly	1		19.4	1069.0
P30/1001	Assembly	1		1.1	47.1
PG/1004	Assembly	2		1.7	73.6
Total				26.4	1380.6






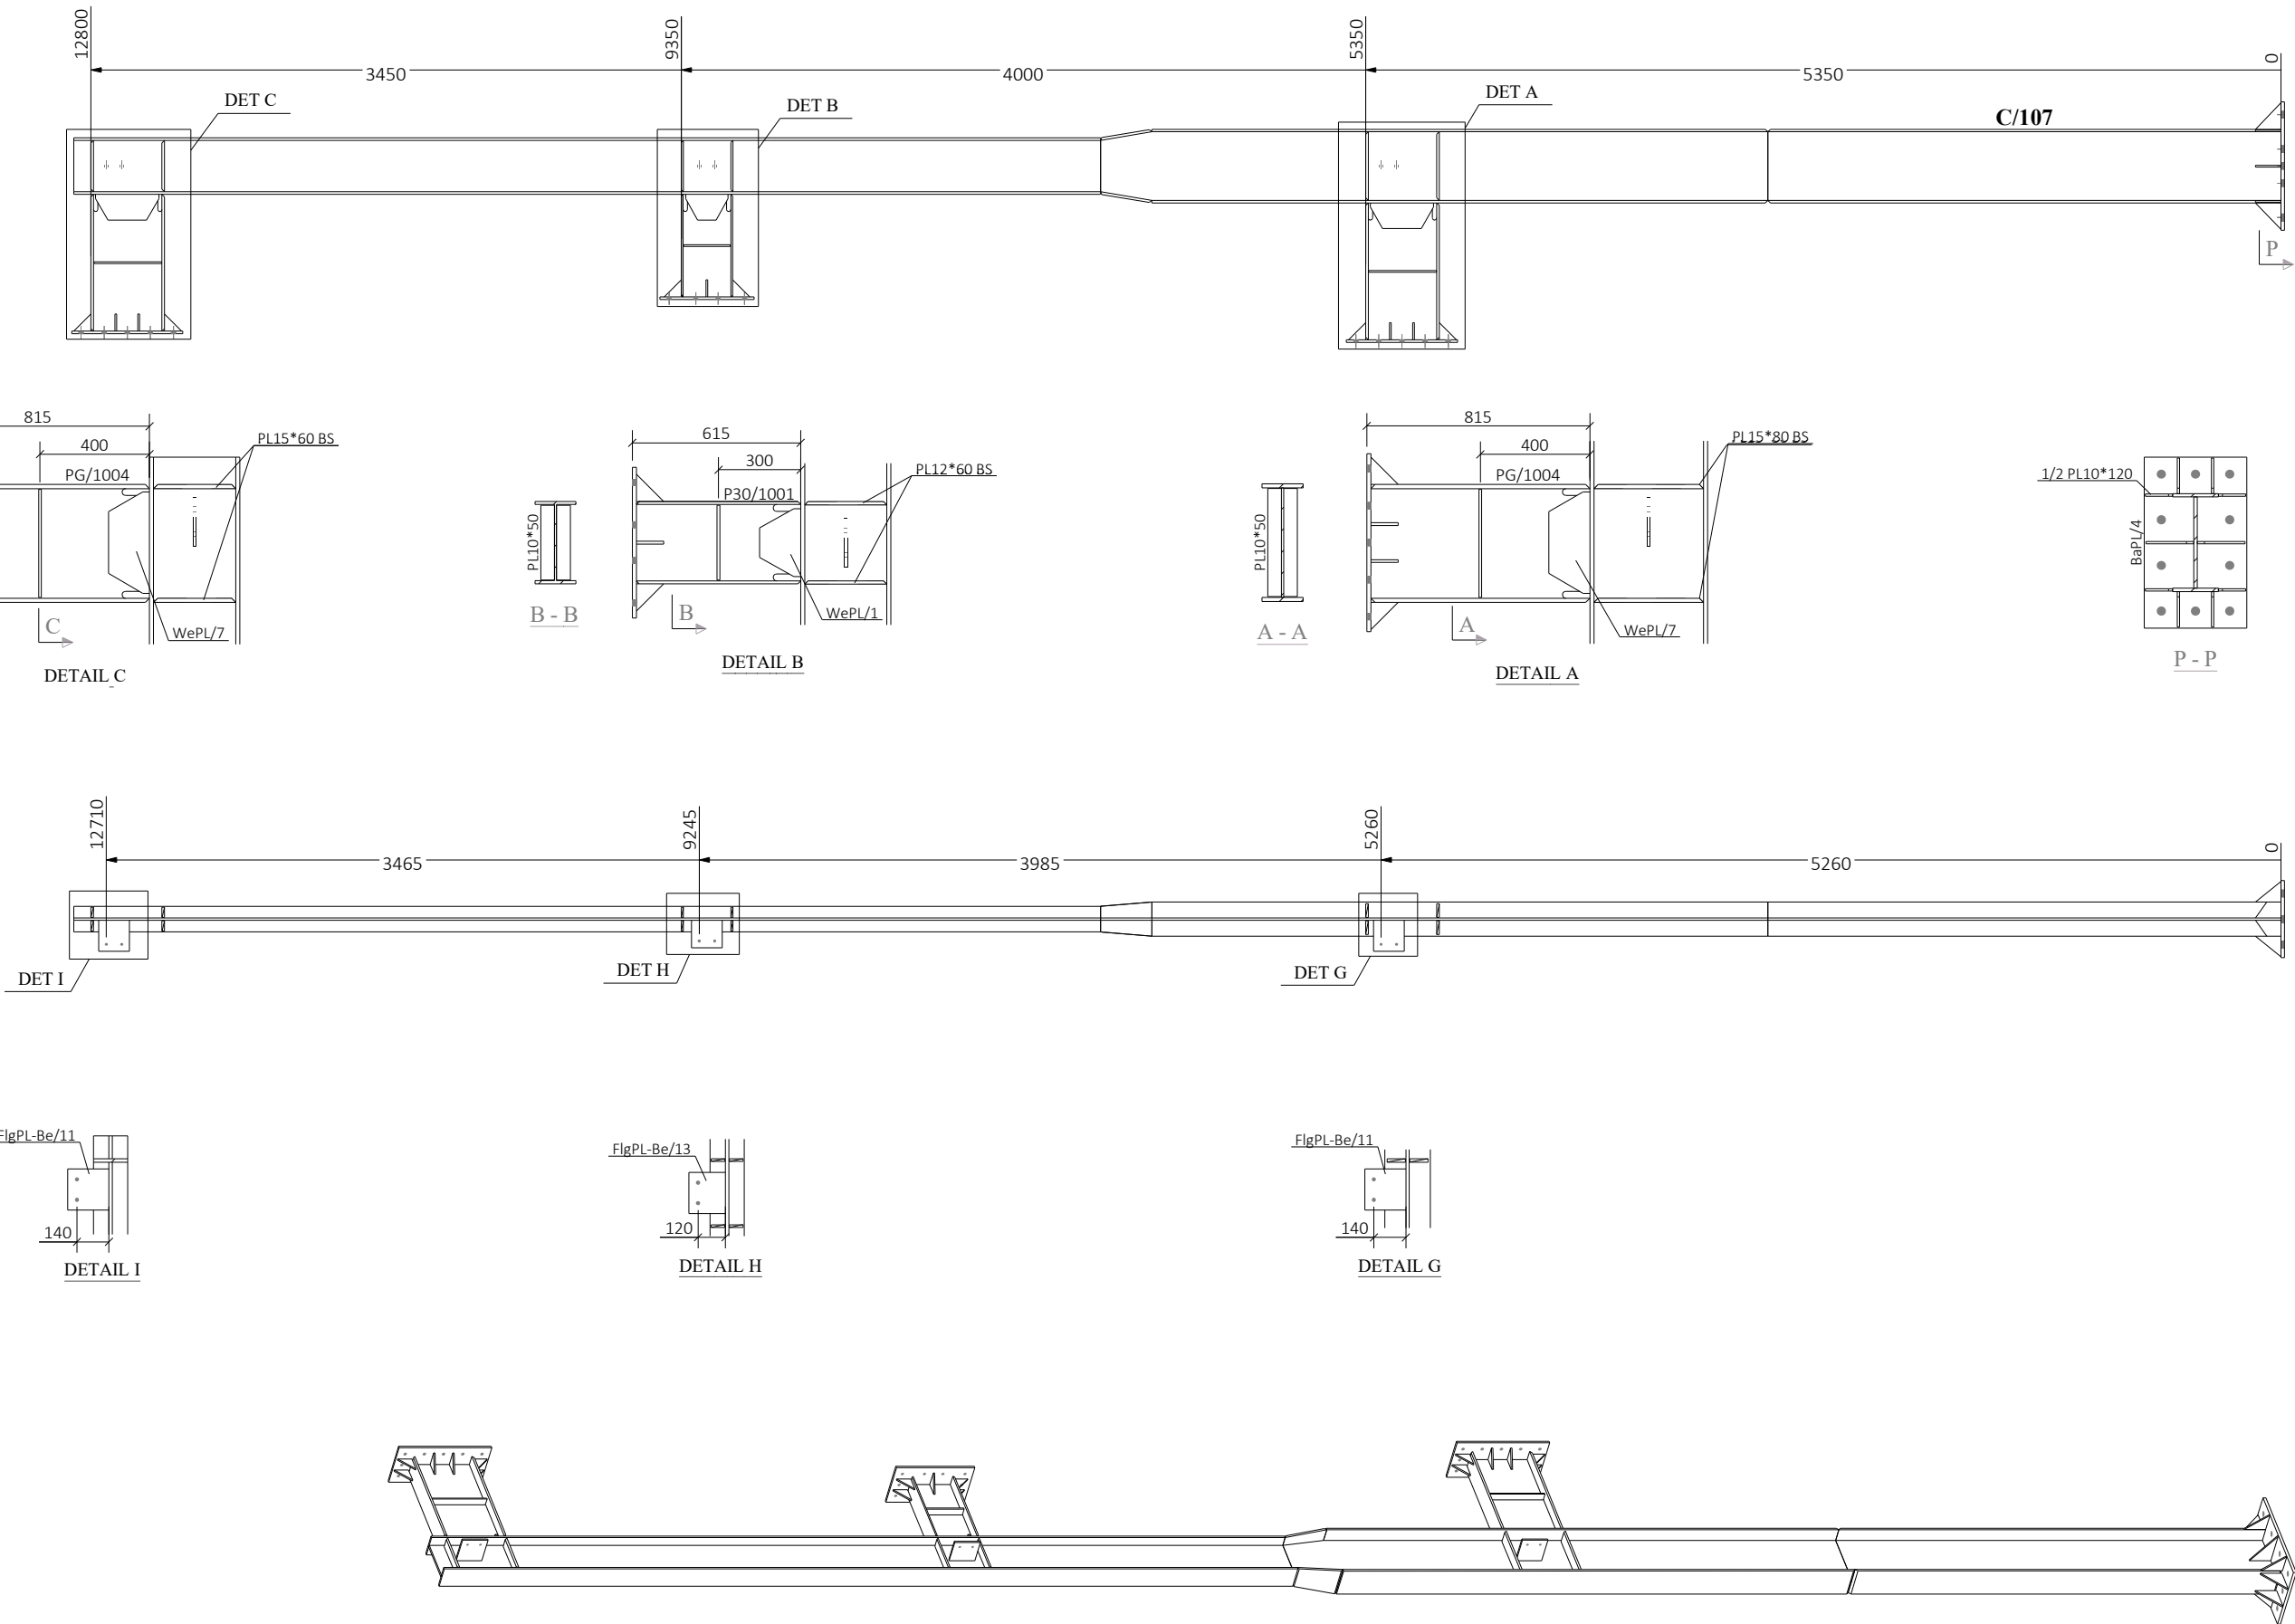








TITLE		ستون تکمیل		
CLIENT				
CONTRACTOR		ISSUED 04.03.		
MODELLED BY	EN ALMASI	SCALE	1:25 1:28	A3
DRAWING No	[C.24]	REVISION No.	0	

Tekla Structures

MATERIAL LIST FOR C/19 N=1					
Mark	Profile	No.	Length	Area	Weight
1/2PL/1009	PL10*130	6	150	0.0	0.8
BaPL/3	PL15*300	1	600	0.4	21.2
FlgPL-Be/9	PL12*60	1	100	0.0	0.6
FlgPL-Be/12	PL12*90	2	180	0.0	1.5
C/105	Assembly	1		7.0	384.8
Total			7.7	414.2	

TITLE		ستون تکمیل			
CLIENT					
CONTRACTOR			ISSUED 04.03.		
MODELLED BY		EN ALMASI	SCALE 1:28	1:30	A4
DRAWING No		[C.19]	REVISION No. 0		

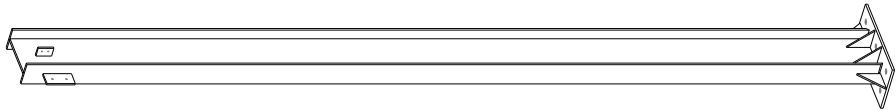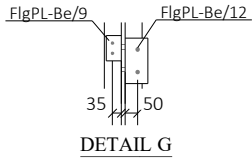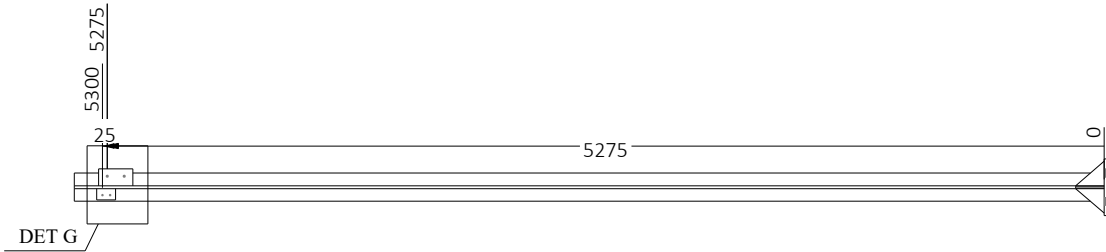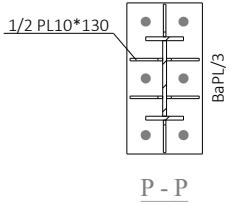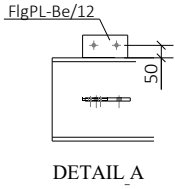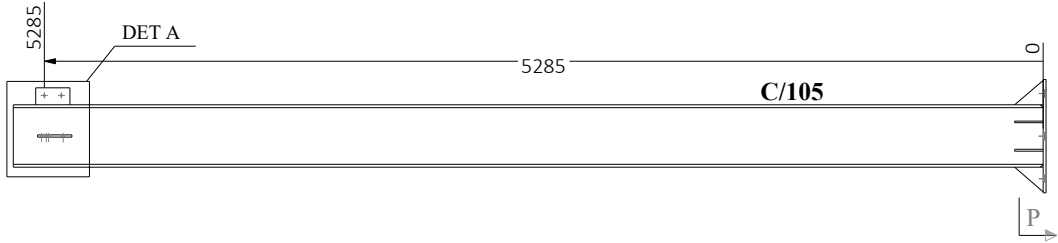


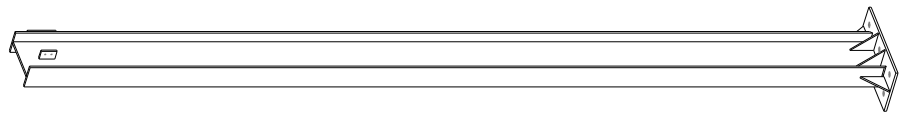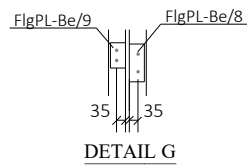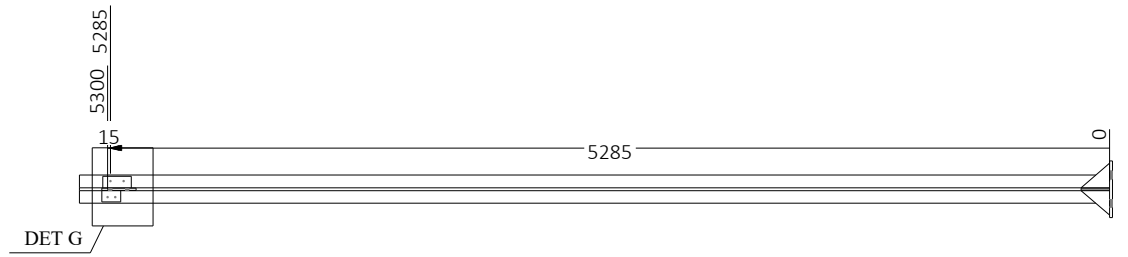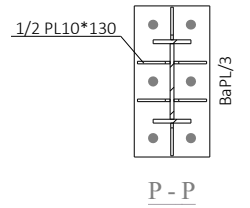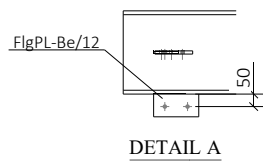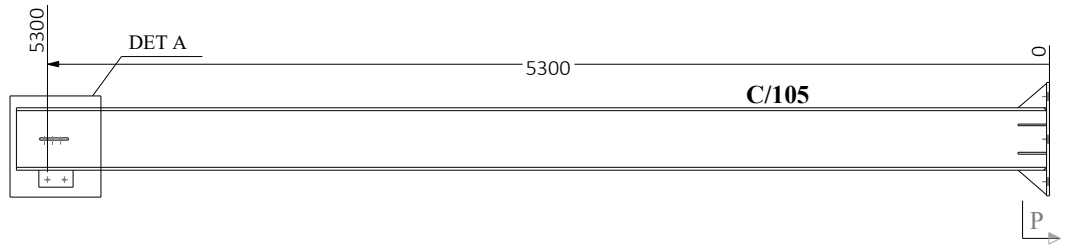


MATERIAL LIST FOR C/20 N=1

Mark	Profile	No.	Length	Area	Weight
1/2PL/1009	PL10*130	6	150	0.0	0.8
BaPL/3	PL15*300	1	600	0.4	21.2
FlgPL-Be/8	PL12*60	1	150	0.0	0.8
FlgPL-Be/9	PL12*60	1	100	0.0	0.6
FlgPL-Be/12	PL12*90	1	180	0.0	1.5
C/105	Assembly	1		7.0	384.8
Total				7.7	413.5

TITLE		ستون تکمیل		
CLIENT				
CONTRACTOR		ISSUED 04.03.		
MODELLED BY	EN ALMASI	SCALE	1:28 1:30	A4
DRAWING No	[C.20]	REVISION No.	0	

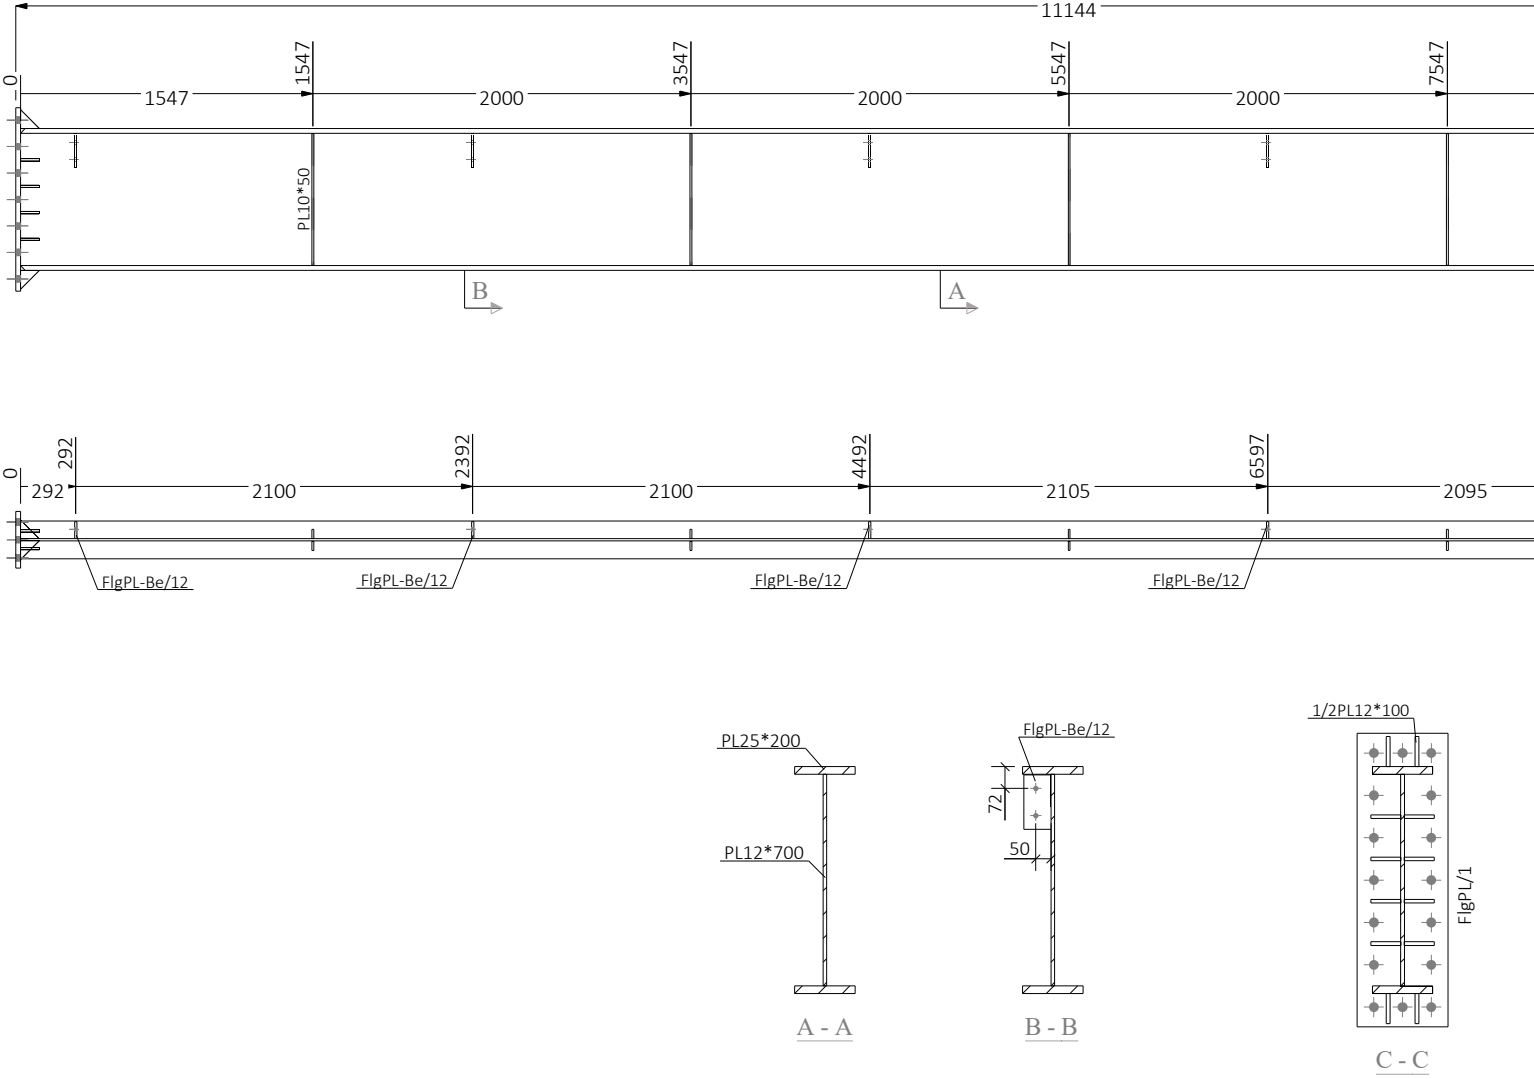


MATERIAL LIST FOR PG/1 N=1					
Mark	Profile	No.	Length	Area	Weight
pg/17	PL12*700	1	11094	15.8	731.5
1/2PL/1001	PL12*100	24	100	0.0	0.5
FlgPL-Be/12	PL12*90	6	180	0.0	1.5
FlgPL/1	PL25*300	2	970	0.6	57.1
Stf/11	PL10*50	10	695	0.1	2.7
pg/1	PL25*200	2	11094	5.0	434.5
Total				28.5	1762.4

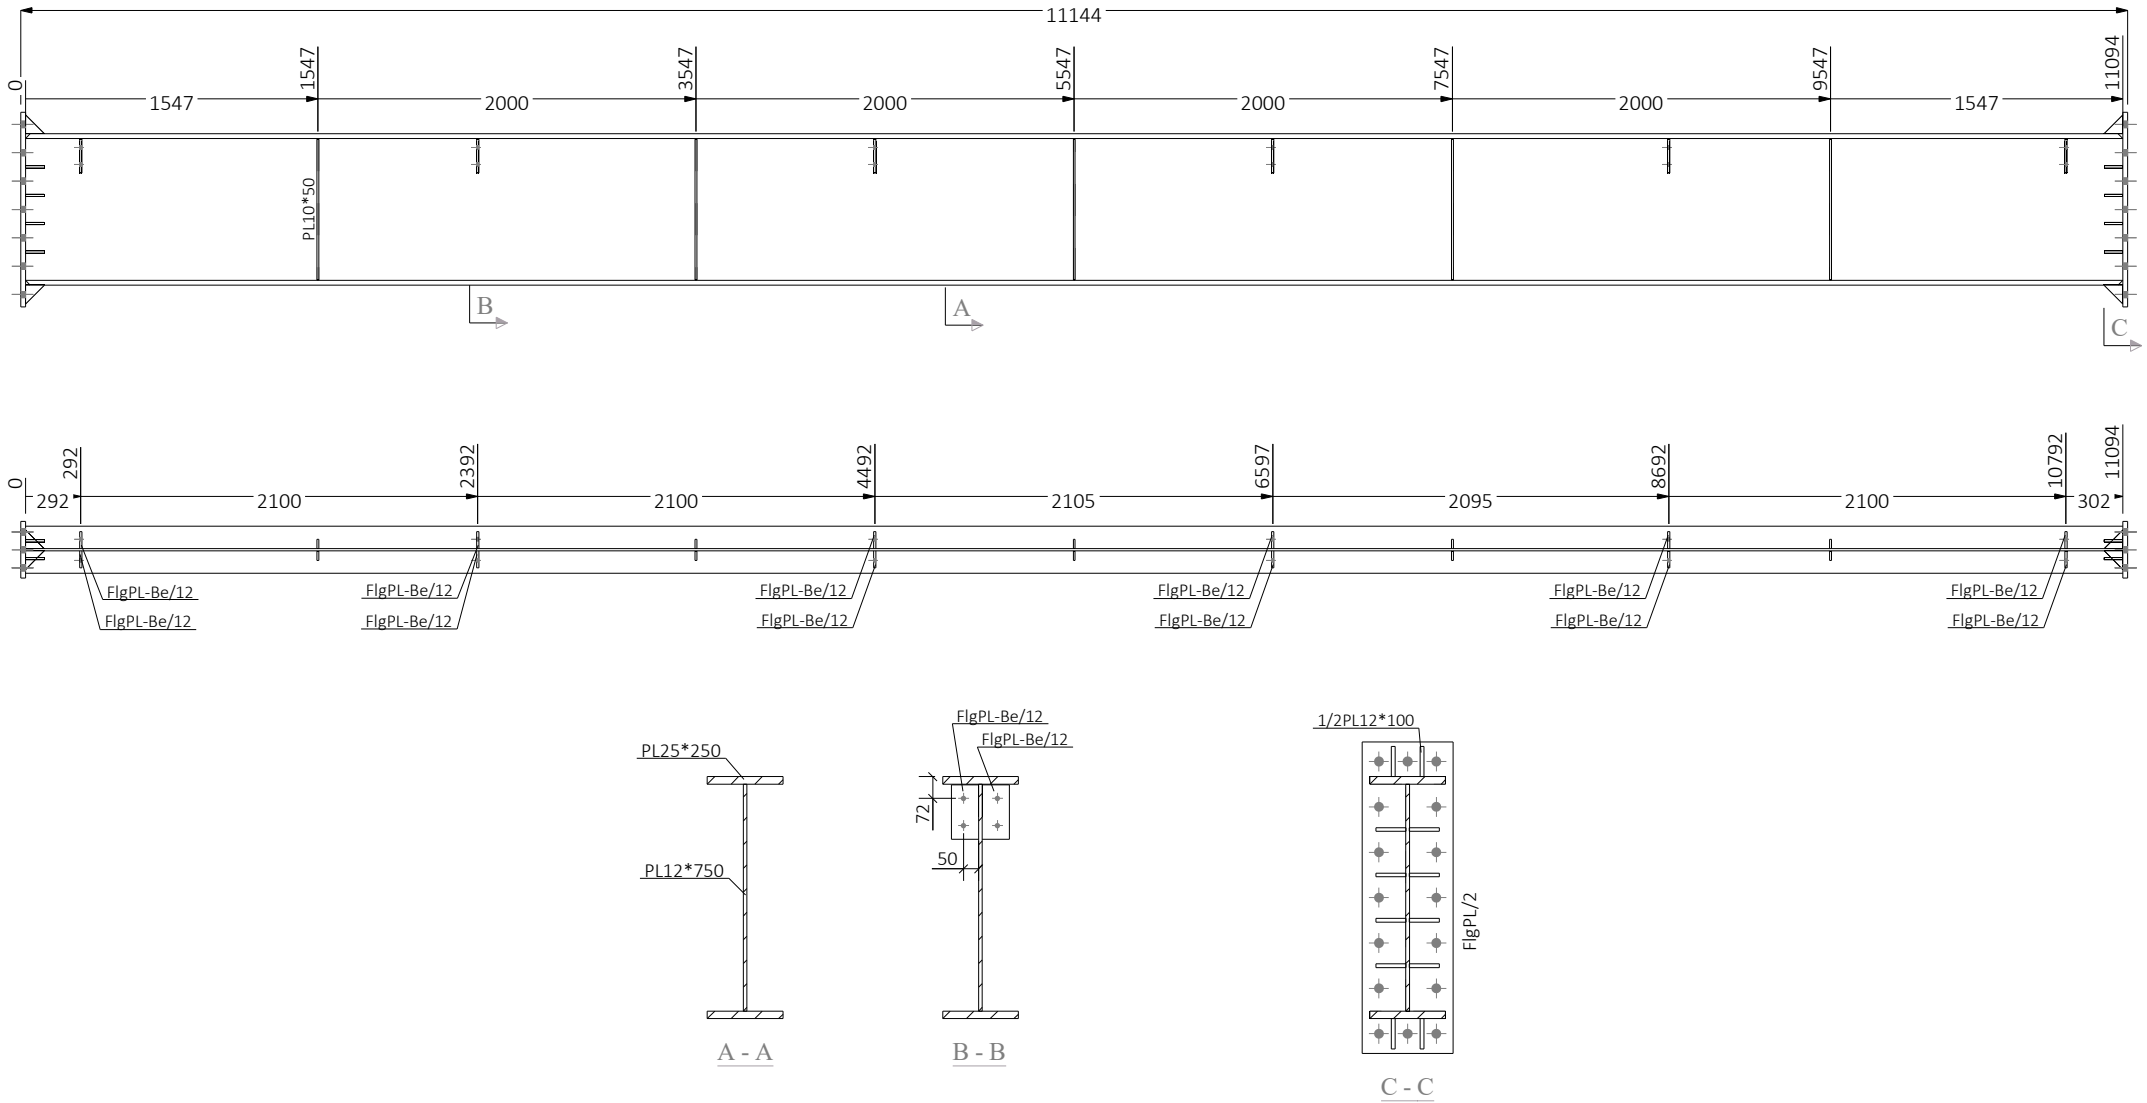

MATERIAL LIST FOR PG/2 N=1					
Mark	Profile	No.	Length	Area	Weight
pg/18	PL12*750	1	11094	16.9	783.8
1/2PL/1001	PL12*100	24	100	0.0	0.5
FlgPL-Be/12	PL12*90	12	180	0.0	1.5
FlgPL/2	PL25*300	2	1030	0.7	60.6
Stf/12	PL10*50	10	745	0.1	2.9
pg/2	PL25*250	2	11094	6.1	543.1
Total			32.2	2050.1	


TITLE			پل		
CLIENT					
CONTRACTOR		ISSUED			
MODELLED BY	EN ALMASI	SCALE	1:25	1:40	
DRAWING No	[PG.2]	REVISION No.	0	A4	

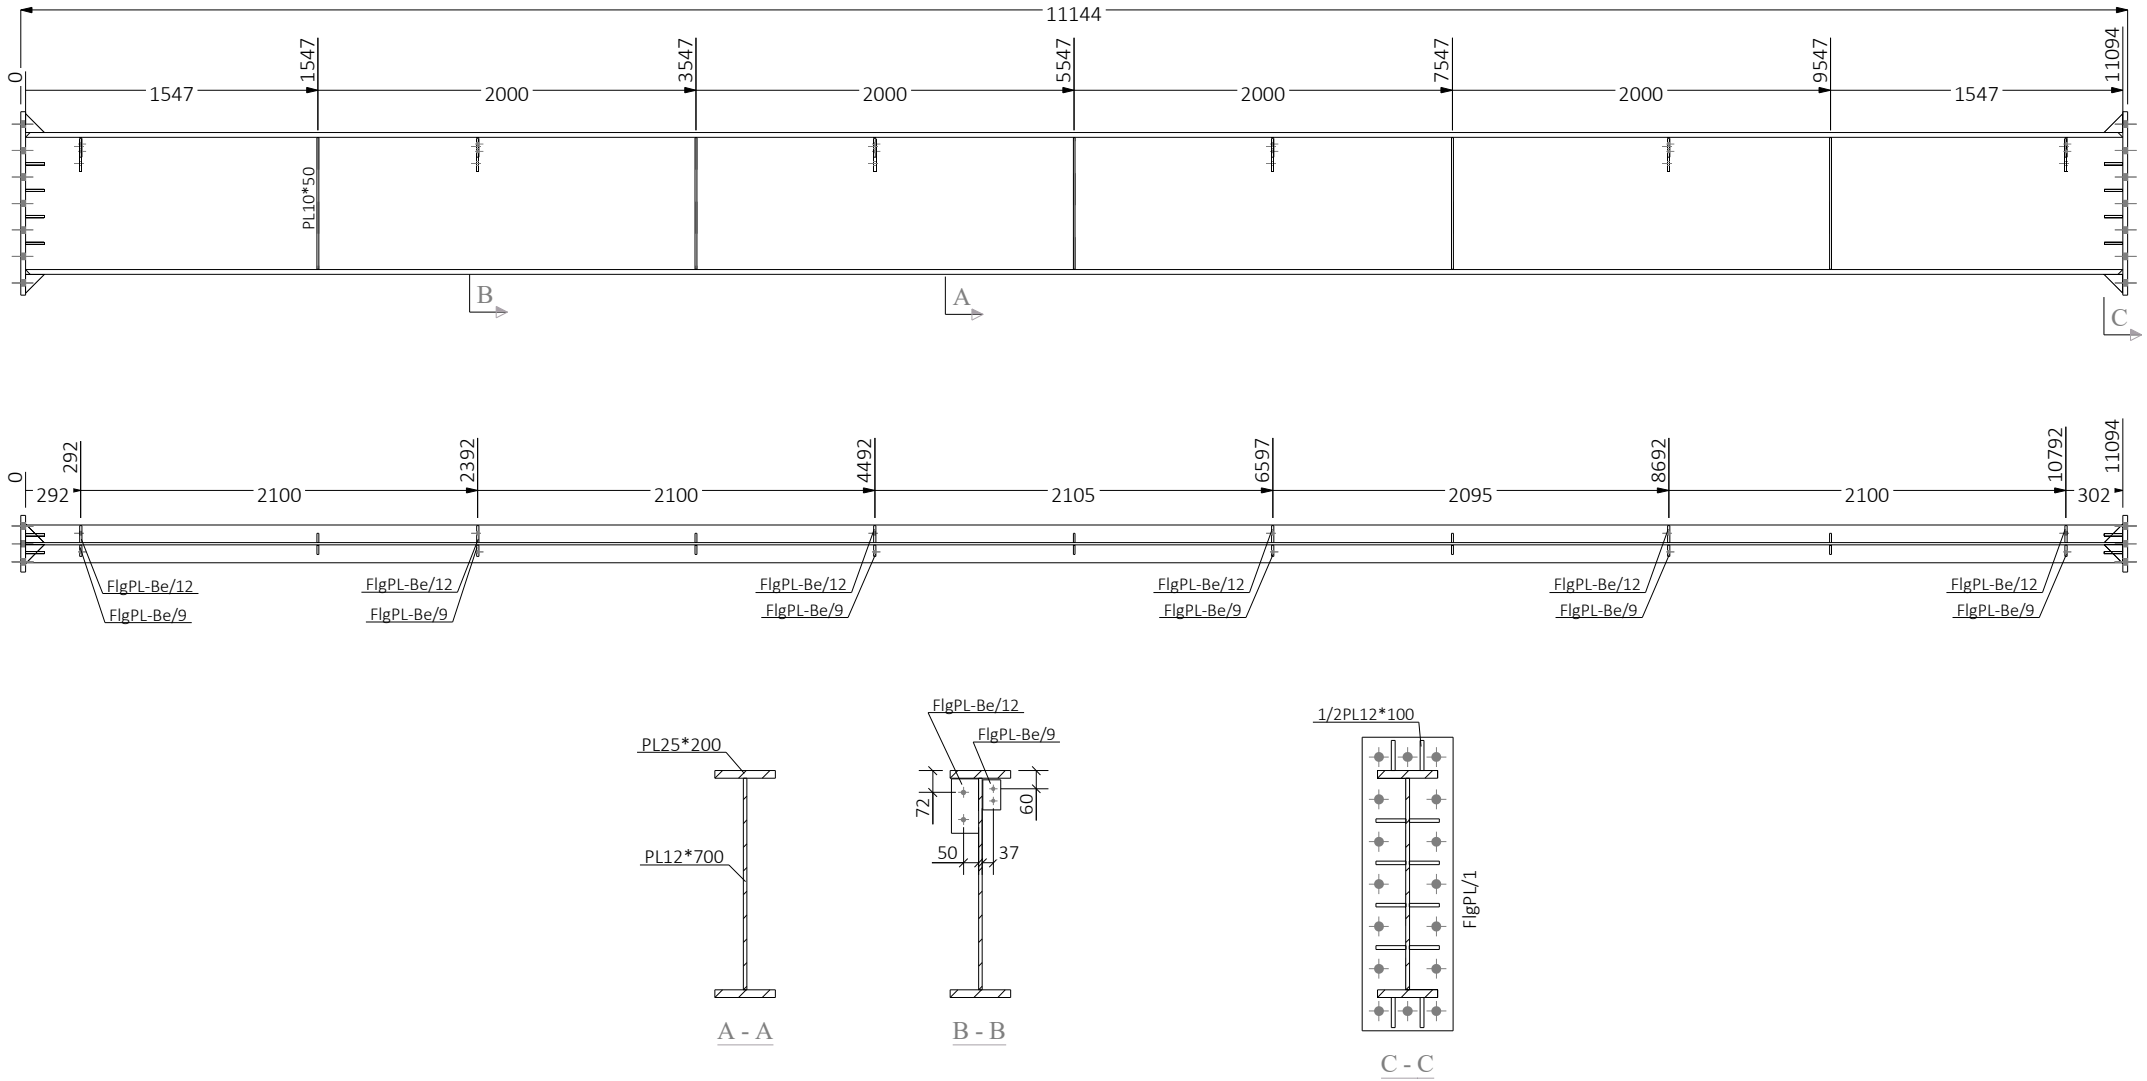

MATERIAL LIST FOR PG/3 N=1					
Mark	Profile	No.	Length	Area	Weight
pg/17	PL12*700	1	11094	15.8	731.5
1/2PL/1001	PL12*100	24	100	0.0	0.5
FlagPL-Be/9	PL12*60	6	100	0.0	0.6
FlagPL-Be/12	PL12*90	6	180	0.0	1.5
FlagPL/1	PL25*300	2	970	0.6	57.1
Stf/11	PL10*50	10	695	0.1	2.7
pg/1	PL25*200	2	11094	5.0	434.5
Total			28.6	1765.8	

TITLE			پل		
CLIENT					
CONTRACTOR		ISSUED			
MODELLED BY	EN ALMASI	SCALE	1:25	1:40	
DRAWING No	[PG.3]	REVISION No.	0	A4	




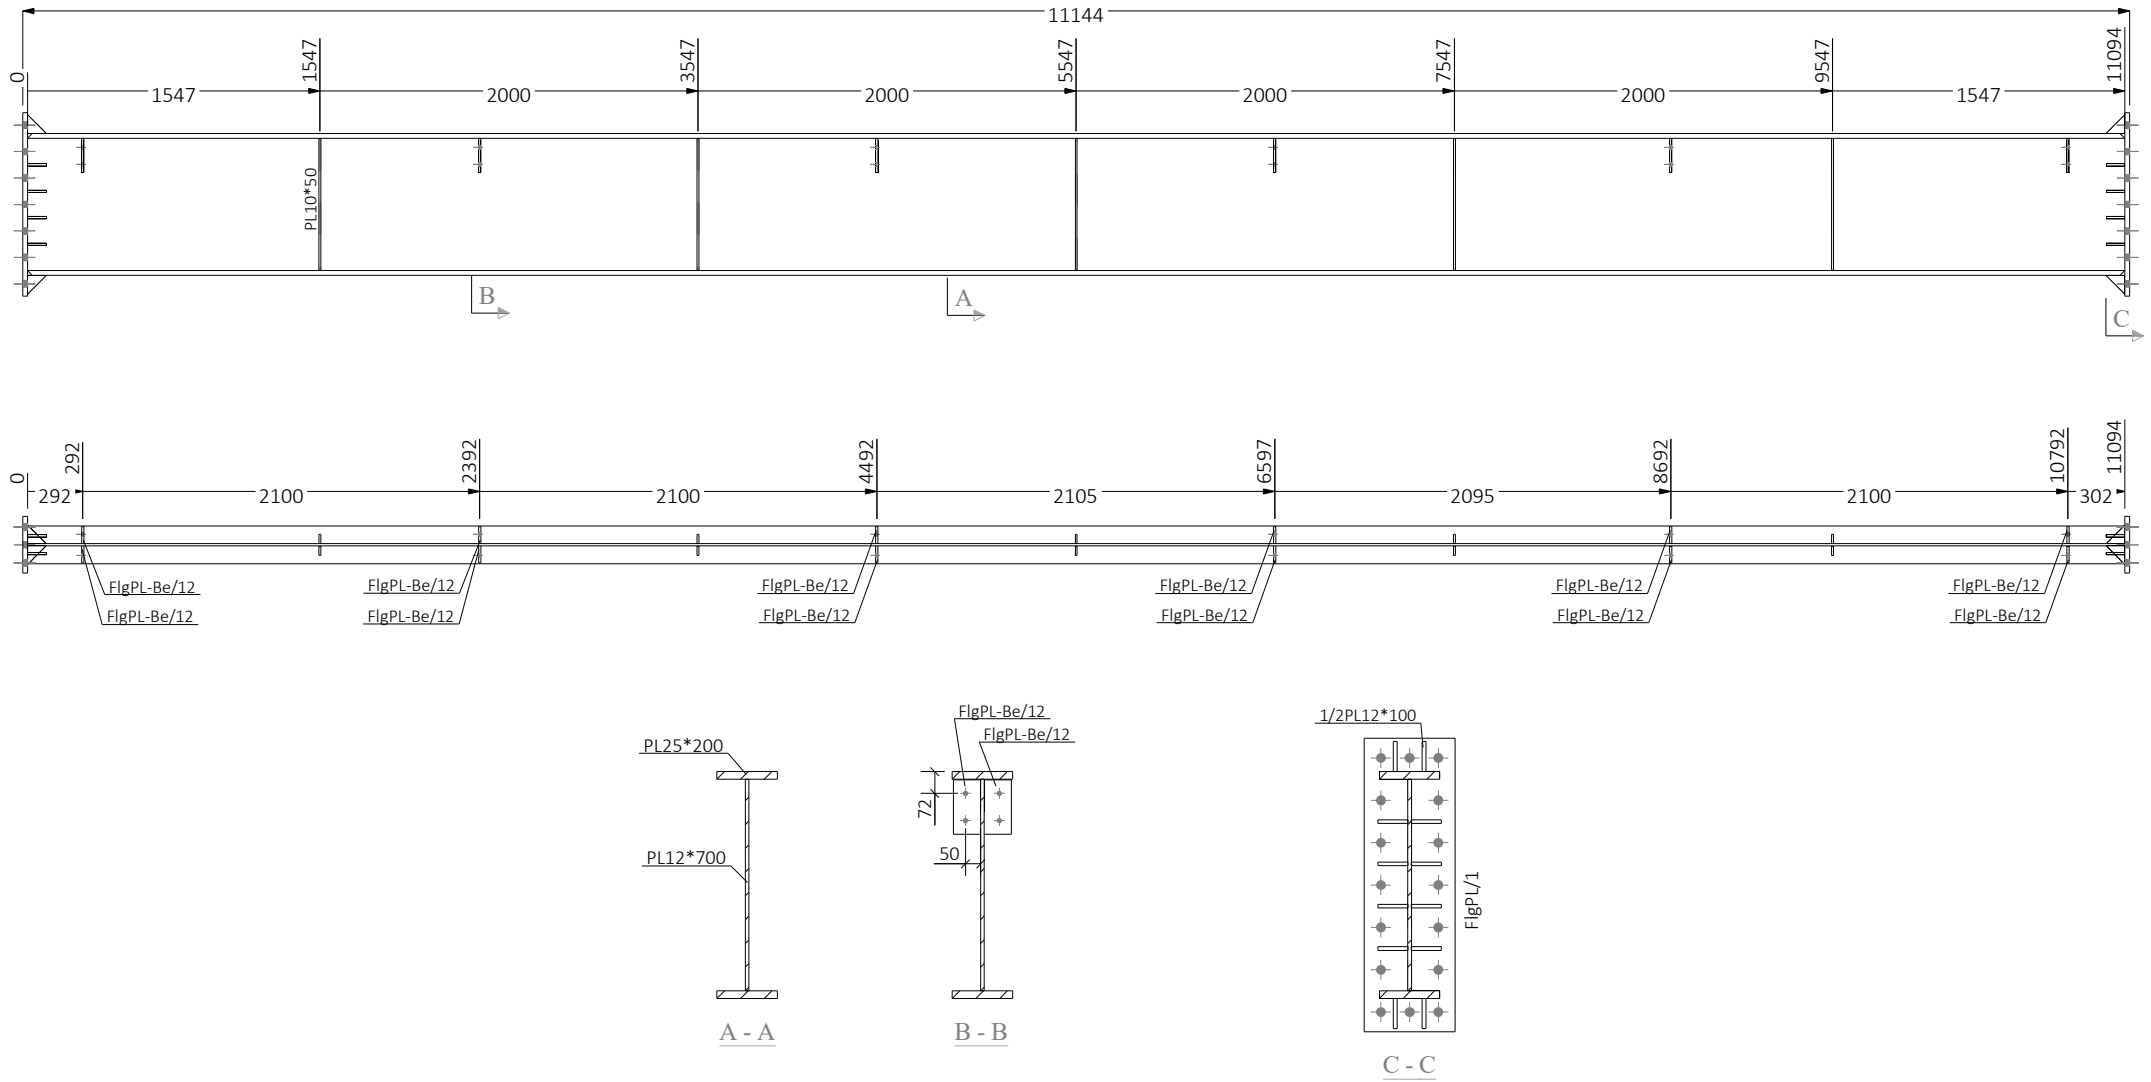

MATERIAL LIST FOR PG/4 N=2					
Mark	Profile	No.	Length	Area	Weight
pg/17	PL12*700	1	11094	15.8	731.5
1/2PL/1001	PL12*100	24	100	0.0	0.5
FlgPL-Be/12	PL12*90	12	180	0.0	1.5
FlgPL/1	PL25*300	2	970	0.6	57.1
Stf/11	PL10*50	10	695	0.1	2.7
pg/1	PL25*200	2	11094	5.0	434.5
Total			28.7	1771.6	

TITLE			پل		
CLIENT					
CONTRACTOR		ISSUED			
MODELLED BY	EN ALMASI		SCALE	1:25 1:40	A4
DRAWING No	[PG.4]		REVISION No.	0	






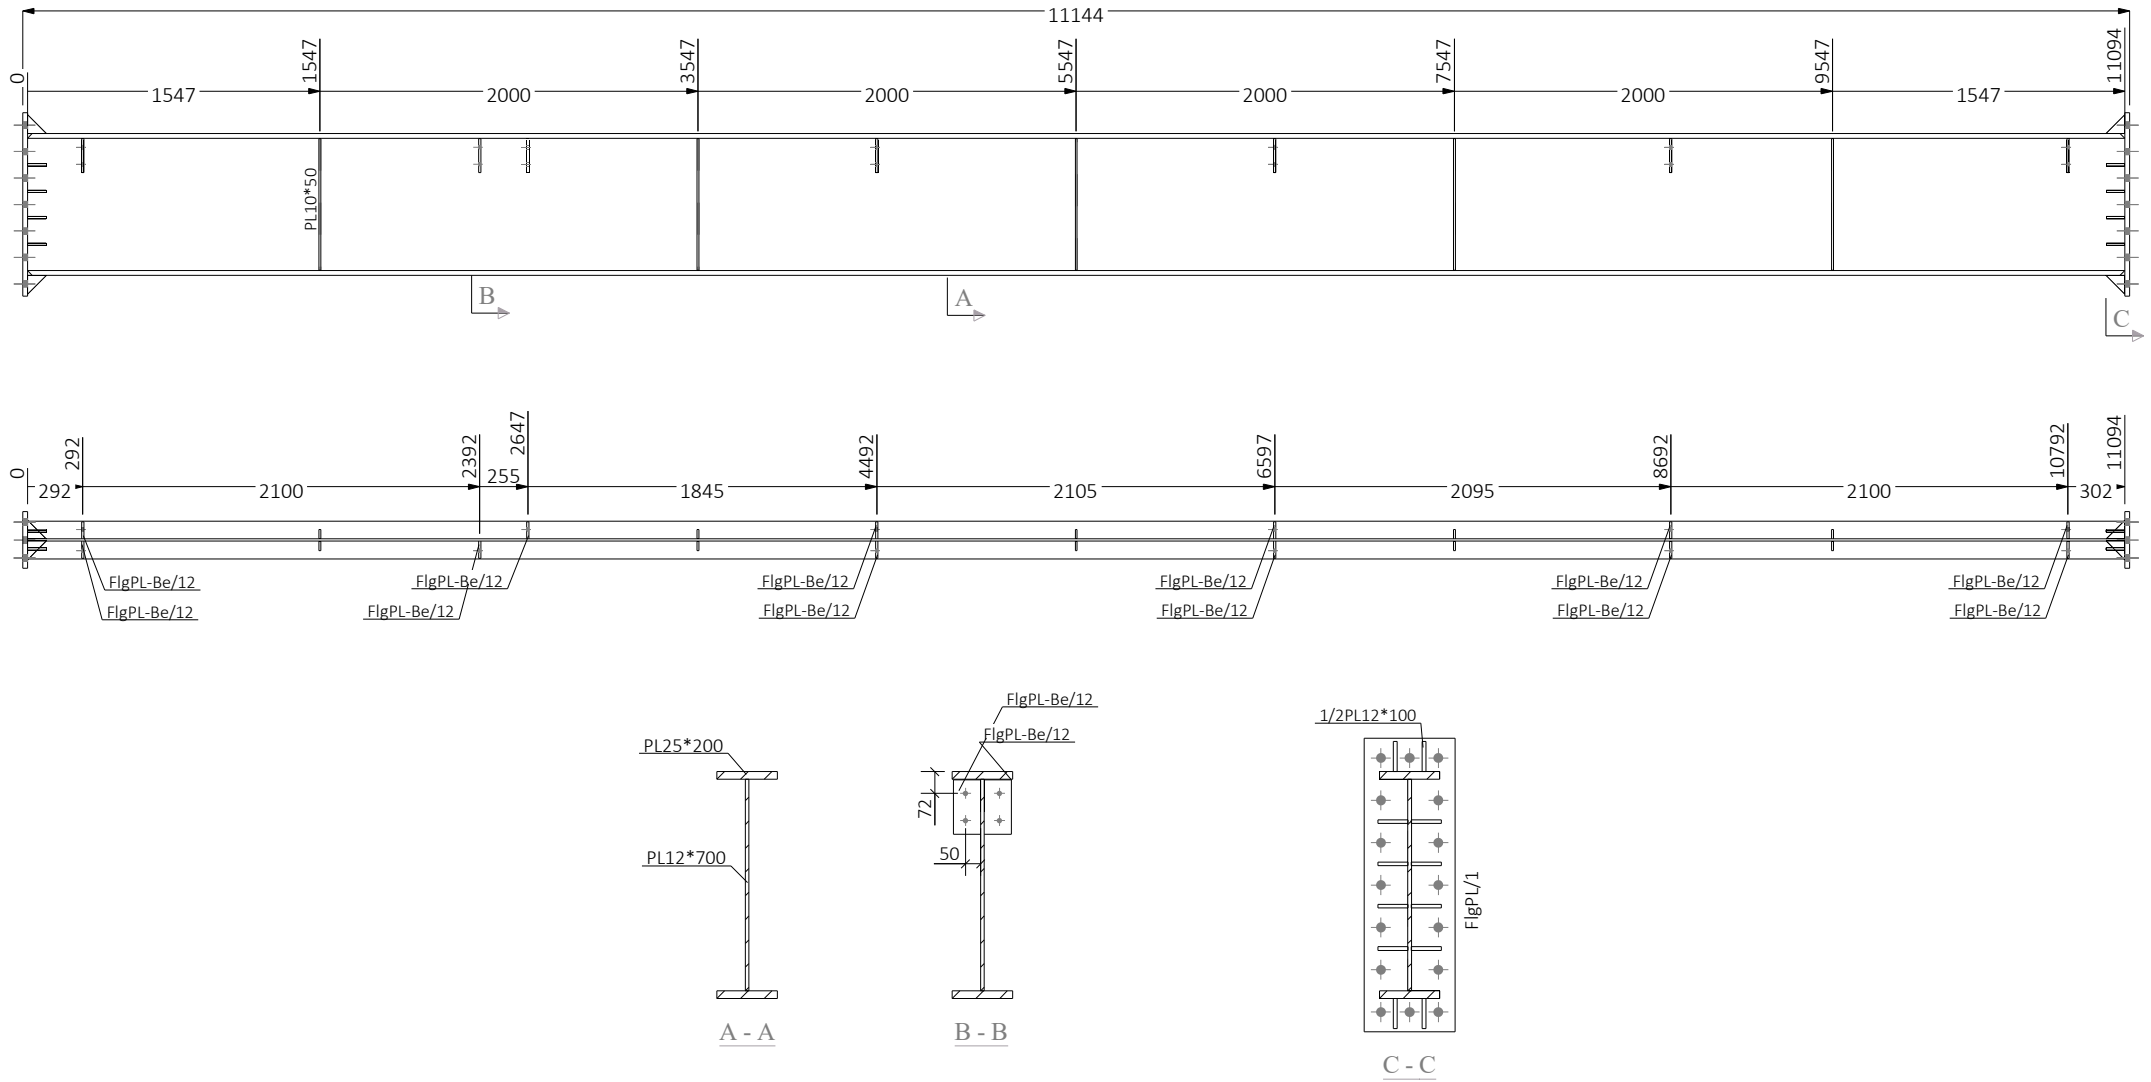

MATERIAL LIST FOR PG/5 N=2					
Mark	Profile	No.	Length	Area	Weight
pg/17	PL12*700	1	11094	15.8	731.5
1/2PL/1001	PL12*100	24	100	0.0	0.5
FlgPL-Be/12	PL12*90	12	180	0.0	1.5
FlgPL/1	PL25*300	2	970	0.6	57.1
Stf/11	PL10*50	10	695	0.1	2.7
pg/1	PL25*200	2	11094	5.0	434.5
Total			28.7	1771.6	

TITLE			پل	
CLIENT				
CONTRACTOR		ISSUED		
MODELLED BY	EN ALMASI	SCALE	1:25 1:40	A4
DRAWING No	[PG.5]	REVISION No.	0	






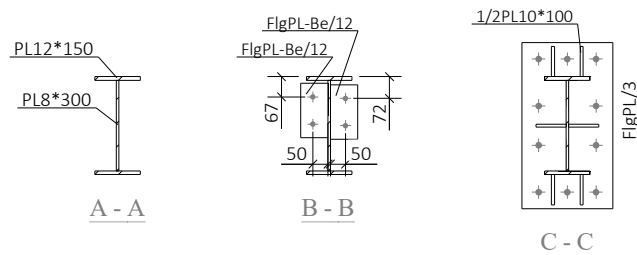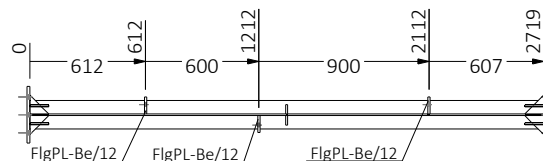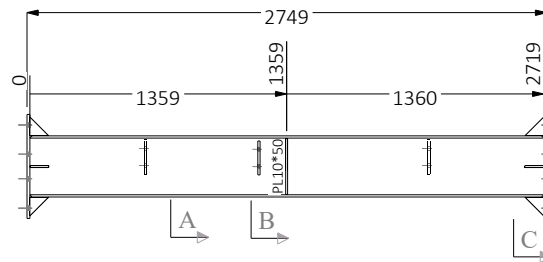

MATERIAL LIST FOR PG/6 N=1					
Mark	Profile	No.	Length	Area	Weight
pg/9	PL8*300	1	2719	1.7	51.2
1/2PL/1010	PL10*100	12	100	0.0	0.4
FlgPL-Be/12	PL12*90	3	180	0.0	1.5
FlgPL/3	PL15*300	2	550	0.4	19.4
Stf/13	PL10*50	2	295	0.0	1.2
pg/19	PL12*150	2	2719	0.9	38.2
Total			4.5	178.2	

TITLE			پل	
CLIENT				
CONTRACTOR		ISSUED		
MODELLED BY	EN ALMASI	SCALE	1:25 1:40	
DRAWING No	[PG.6]	REVISION No.	0	A4



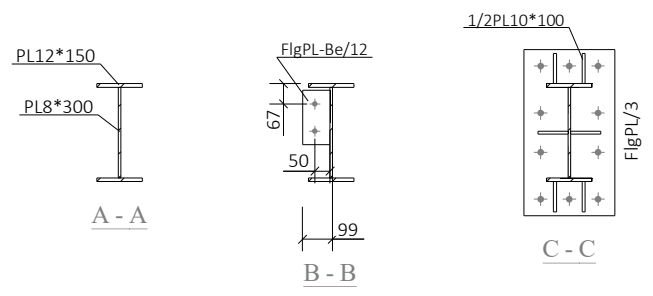
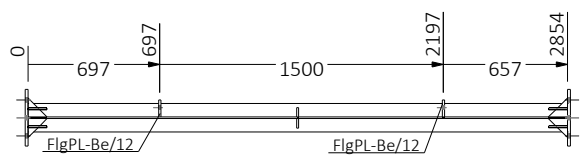
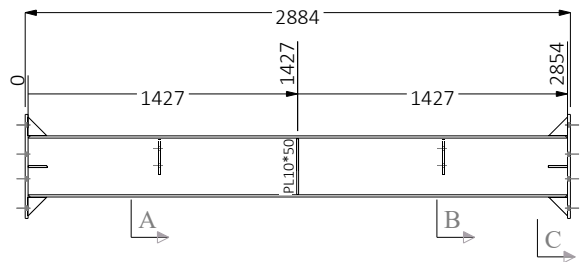


MATERIAL LIST FOR PG/7 N=1					
Mark	Profile	No.	Length	Area	Weight
pg/13	PL8*300	1	2854	1.8	53.8
1/2PL/1010	PL10*100	12	100	0.0	0.4
FlgPL-Be/12	PL12*90	2	180	0.0	1.5
FlgPL/3	PL15*300	2	550	0.4	19.4
Stf/13	PL10*50	2	295	0.0	1.2
pg/20	PL12*150	2	2854	0.9	40.2
Total			4.6	183.0	

TITLE			
CLIENT			
CONTRACTOR		ISSUED	
MODELLED BY		EN ALMASI	SCALE 1:25 1:40
DRAWING No		[PG.7]	REVISION No. 0






A4

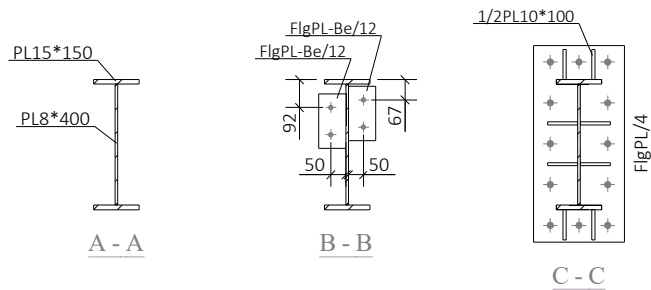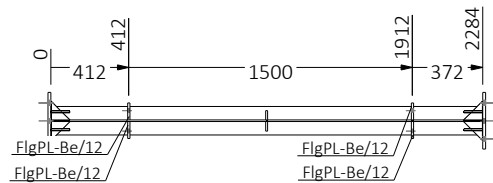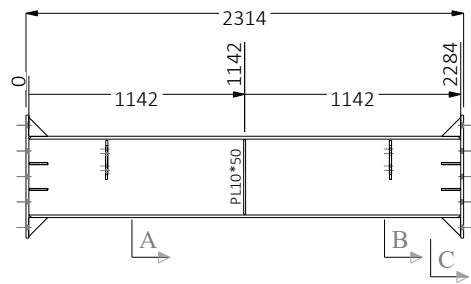

MATERIAL LIST FOR PG/8 N=1					
Mark	Profile	No.	Length	Area	Weight
pg/10	PL8*400	1	2284	1.9	57.4
1/2PL1010	PL10*100	16	100	0.0	0.4
FlgPL-Be/12	PL12*90	4	180	0.0	1.5
FlgPL/4	PL15*300	2	650	0.4	23.0
Stf/17	PL10*50	2	395	0.0	1.6
pg/3	PL15*150	2	2284	0.8	40.1
Total			4.7	198.9	




TITLE		پل		
CLIENT				
CONTRACTOR		ISSUED	A4	
MODELLED BY	EN ALMASI	SCALE 1:25 1:40		
DRAWING No	[PG.8]	REVISION No. 0		

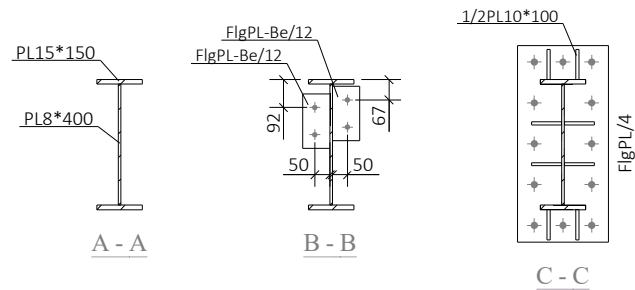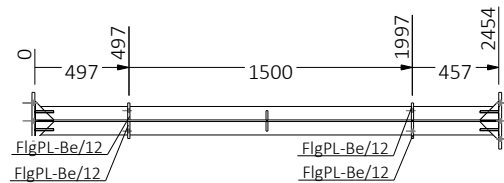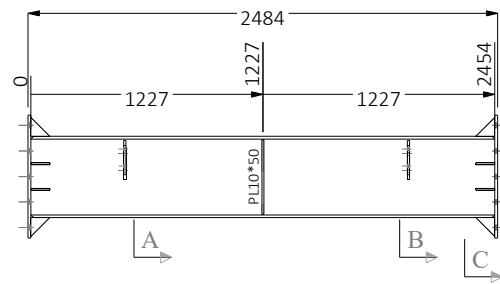

MATERIAL LIST FOR PG/9 N=1

Mark	Profile	No.	Length	Area	Weight
pg/16	PL8*400	1	2454	2.0	61.6
1/2PL/1010	PL10*100	16	100	0.0	0.4
FlgPL-Be/12	PL12*90	4	180	0.0	1.5
FlgPL/4	PL15*300	2	650	0.4	23.0
Stf/17	PL10*50	2	395	0.0	1.6
pg/8	PL15*150	2	2454	0.8	43.1
Total			4.9	209.2	




TITLE			پل	
CLIENT				
CONTRACTOR		ISSUED		
MODELLED BY	EN ALMASI	SCALE	1:25 1:40	A4
DRAWING No	[PG.9]	REVISION No.	0	

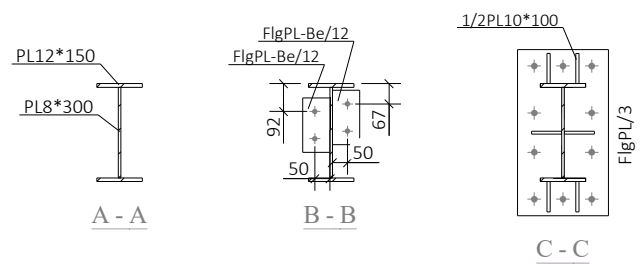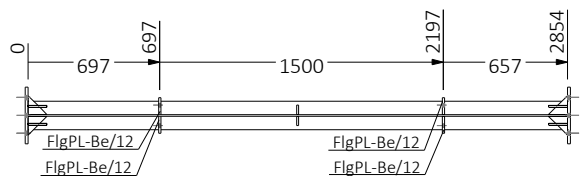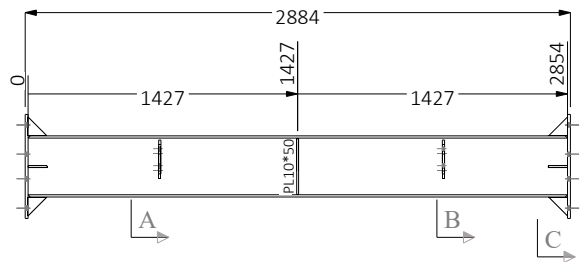

MATERIAL LIST FOR PG/10 N=1					
Mark	Profile	No.	Length	Area	Weight
pg/13	PL8*300	1	2854	1.8	53.8
1/2PL/1010	PL10*100	12	100	0.0	0.4
FigPL-Be/12	PL12*90	4	180	0.0	1.5
FigPL/3	PL15*300	2	550	0.4	19.4
Stf/13	PL10*50	2	295	0.0	1.2
pg/20	PL12*150	2	2854	0.9	40.2
Total			4.7	186.1	




TITLE			
CLIENT		ISSUED	
CONTRACTOR		SCALE	1:25 1:40
MODELLED BY	EN ALMASI	REVISION No.	0
DRAWING No	[PG.10]		



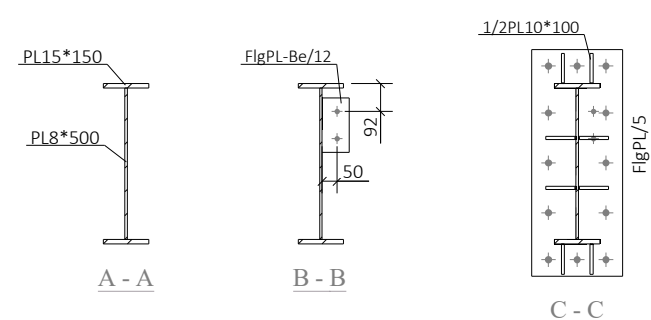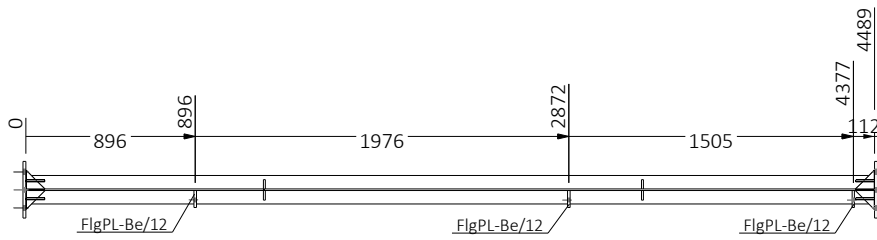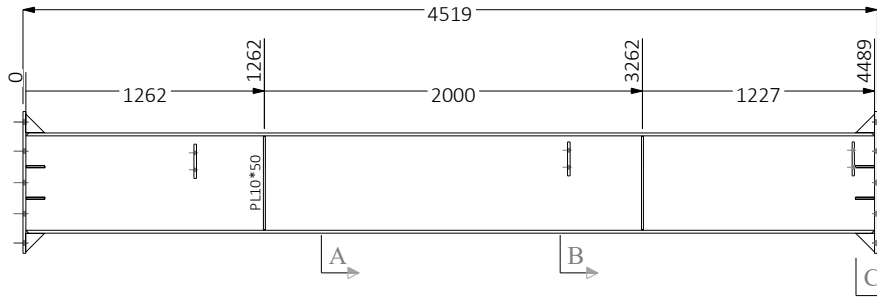




MATERIAL LIST FOR PG/11 N=1					
Mark	Profile	No.	Length	Area	Weight
pg/12	PL8*500	1	4489	4.6	141.0
1/2PL/1010	PL10*100	16	100	0.0	0.4
FlgPL-Be/12	PL12*90	3	180	0.0	1.5
FlgPL/5	PL15*300	2	750	0.5	26.5
Stf/18	PL10*50	4	495	0.1	1.9
pg/5	PL15*150	2	4489	1.5	79.0
Total			9.1	370.6	

TITLE			پل	
CLIENT				
CONTRACTOR		ISSUED		
MODELLED BY	EN ALMASI	SCALE	1:25 1:40	
DRAWING No	[PG.11]	REVISION No.	0	A4

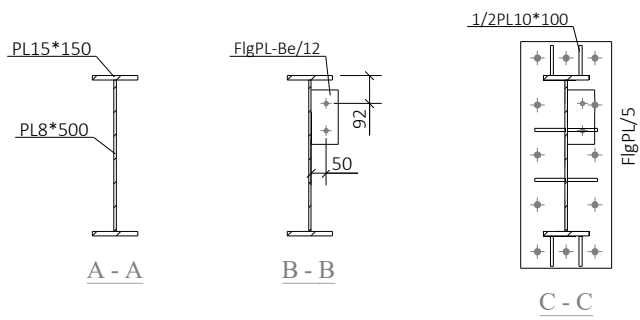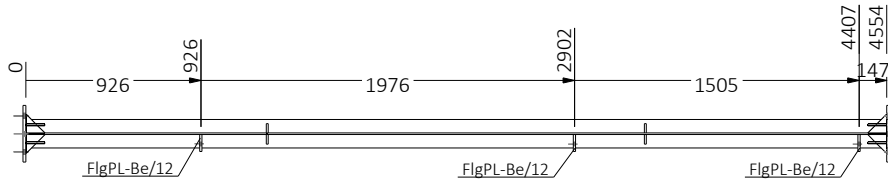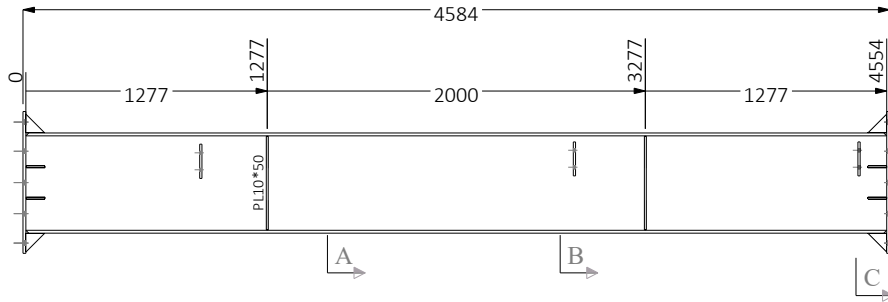




MATERIAL LIST FOR PG/12 N=1					
Mark	Profile	No.	Length	Area	Weight
pg/14	PL8*500	1	4554	4.6	143.0
1/2PL/1010	PL10*100	16	100	0.0	0.4
FlgPL-Be/12	PL12*90	3	180	0.0	1.5
FlgPL/5	PL15*300	2	750	0.5	26.5
Stf/18	PL10*50	4	495	0.1	1.9
pg/6	PL15*150	2	4554	1.5	80.2
Total			9.2	375.0	

TITLE		پل		
CLIENT				
CONTRACTOR		ISSUED		
MODELLED BY	EN ALMASI	SCALE	1:25	1:40
DRAWING No	[PG.12]	REVISION No.	0	A4

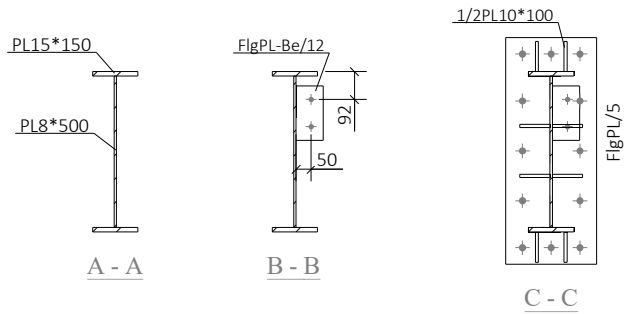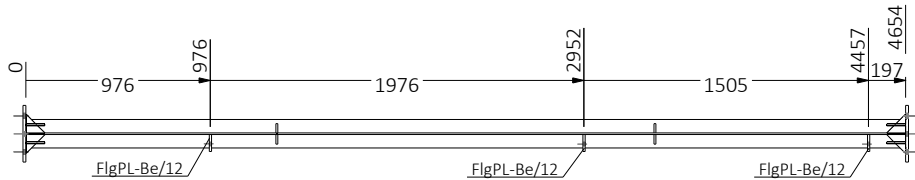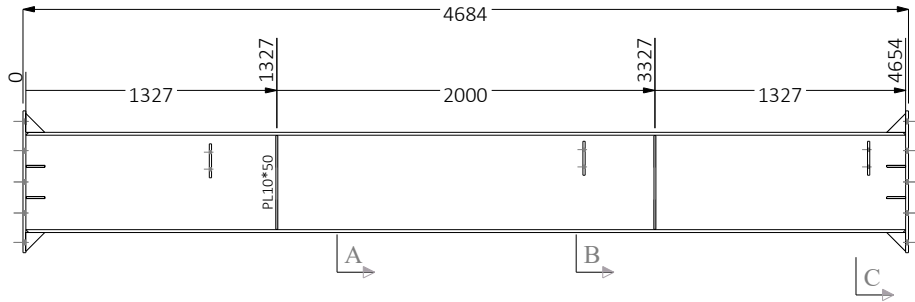

MATERIAL LIST FOR PG/13 N=1					
Mark	Profile	No.	Length	Area	Weight
pg/15	PL8*500	1	4654	4.7	146.1
1/2PL/1010	PL10*100	16	100	0.0	0.4
FlgPL-Be/12	PL12*90	3	180	0.0	1.5
FlgPL/5	PL15*300	2	750	0.5	26.5
Stf/18	PL10*50	4	495	0.1	1.9
pg/7	PL15*150	2	4654	1.5	81.9
Total			9.3	381.6	




TITLE		پل		
CLIENT				
CONTRACTOR		ISSUED		
MODELLED BY	EN ALMASI	SCALE	1:25 1:40	
DRAWING No	[PG.13]	REVISION No.	0	A4

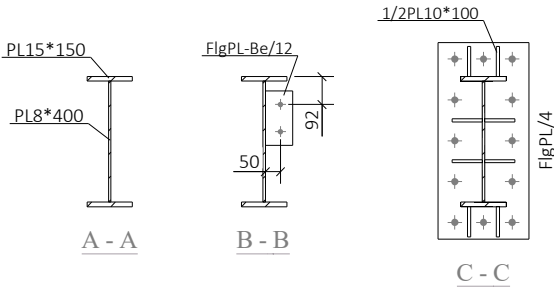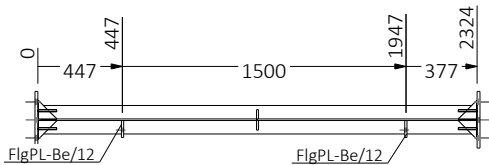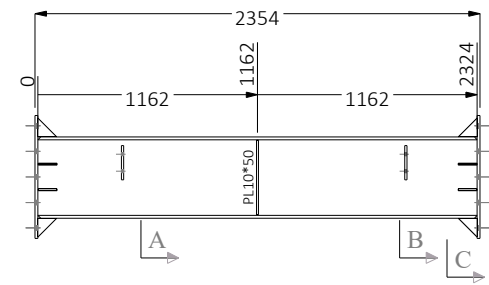

MATERIAL LIST FOR PG/14 N=1

Mark	Profile	No.	Length	Area	Weight
pg/11	PL8*400	1	2324	1.9	58.4
1/2PL/1010	PL10*100	16	100	0.0	0.4
FlgPL-Be/12	PL12*90	2	180	0.0	1.5
FlgPL/4	PL15*300	2	650	0.4	23.0
Stf/17	PL10*50	2	395	0.0	1.6
pg/4	PL15*150	2	2324	0.8	40.8
Total			4.7	198.3	




TITLE		پل			
CLIENT					
CONTRACTOR		ISSUED			
MODELLED BY	EN ALMASI	SCALE	1:25	1:40	A4
DRAWING No	[PG.14]	REVISION No.	0		

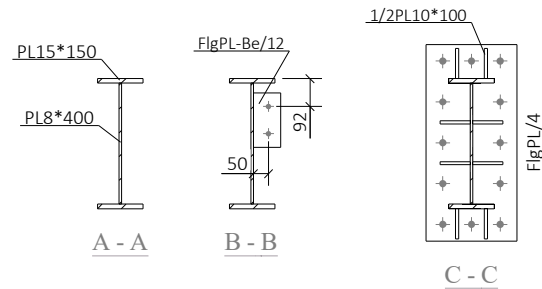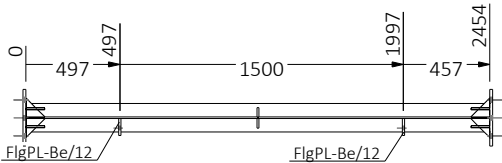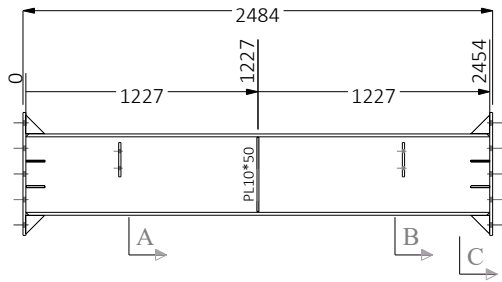


MATERIAL LIST FOR PG/15 N=1

Mark	Profile	No.	Length	Area	Weight
pg/16	PL8*400	1	2454	2.0	61.6
1/2PL/1010	PL10*100	16	100	0.0	0.4
FigPL-Be/12	PL12*90	2	180	0.0	1.5
FigPL/4	PL15*300	2	650	0.4	23.0
Stf/17	PL10*50	2	395	0.0	1.6
pg/8	PL15*150	2	2454	0.8	43.1
Total			4.9	206.2	


TITLE		پل				
CLIENT						
CONTRACTOR		ISSUED				
MODELLED BY	EN ALMASI	SCALE	1:25	1:40	A4	
DRAWING No	[PG.15]	REVISION No.	0			

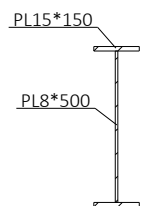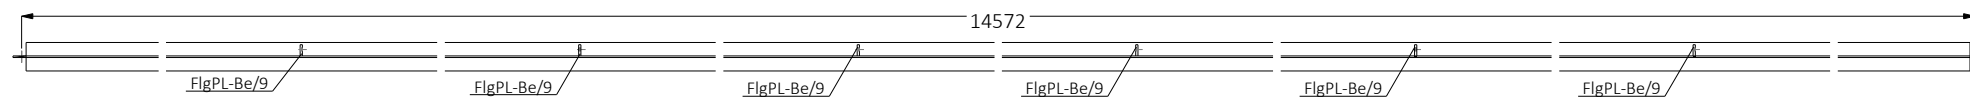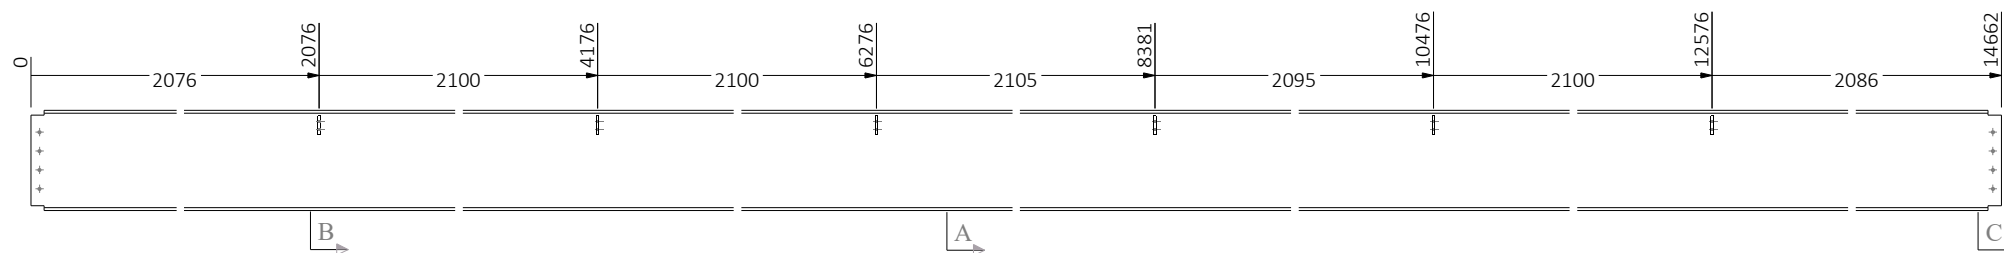


A - A

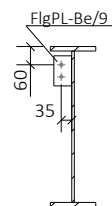

B - B

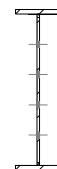

C - C


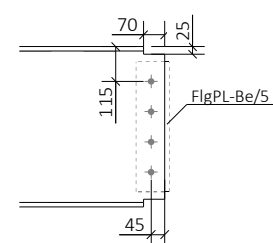


MATERIAL LIST FOR PG/201 N=1

Mark	Profile	No.	Length	Area	Weight
pg/207	PL8*500	1	14662	14.9	460.2
FlgPL-Be/9	PL12*60	6	100	0.0	0.6
pg/206	PL15*150	2	14522	4.8	256.5
Total			24.6	976.6	



TITLE		پل			
CLIENT					
CONTRACTOR		ISSUED			
MODELLED BY	EN ALMASI	SCALE	1:25	1:40	A4
DRAWING No	[PG.201]	REVISION No.	0		



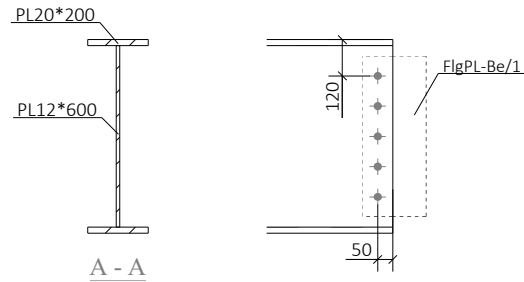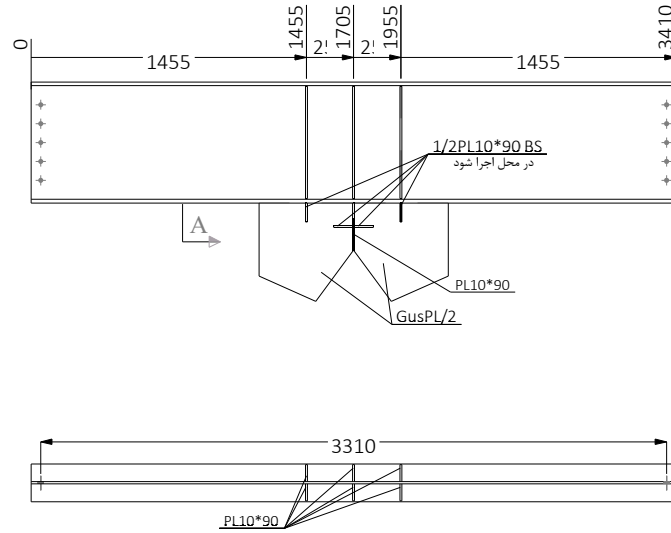



MATERIAL LIST FOR PG/202 N=2					
Mark	Profile	No.	Length	Area	Weight
pg/211	PL12*600	1	3410	4.2	192.7
1/2PL/1011	PL10*90	8	100	0.0	0.4
GusPL/2	PL15*520	2	500	0.5	25.1
Stf/19	PL10*90	6	595	0.1	4.2
Stf/20	PL10*90	2	250	0.1	1.8
pg/201	PL20*200	2	3410	1.5	107.1
Total			9.0	488.6	

TITLE		پل		
CLIENT				
CONTRACTOR		ISSUED		
MODELLED BY	EN ALMASI	SCALE	1:25	1:40
DRAWING No	[PG.202]	REVISION No.	0	A4

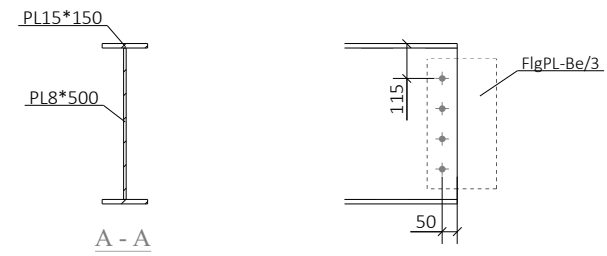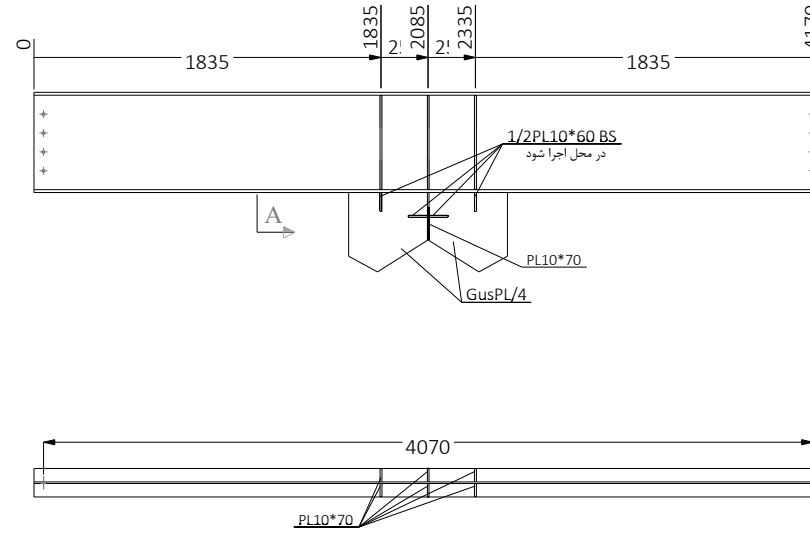





MATERIAL LIST FOR PG/203 N=2					
Mark	Profile	No.	Length	Area	Weight
pg/208	PL8*500	1	4170	4.2	130.9
1/2PL/1012	PL10*60	8	100	0.0	0.2
GusPL/4	PL15*420	2	420	0.3	17.3
Stf/21	PL10*70	6	495	0.1	2.7
Stf/22	PL10*70	2	250	0.0	1.4
pg/203	PL15*150	2	4170	1.4	73.7
Total			8.3	333.9	

TITLE			پل		
CLIENT					
CONTRACTOR		ISSUED			
MODELLED BY	EN ALMASI	SCALE	1:25	1:40	A4
DRAWING No	[PG.203]	REVISION No.	0		

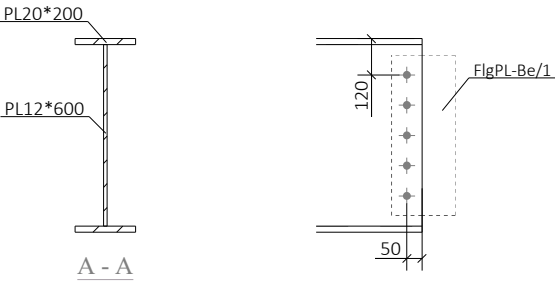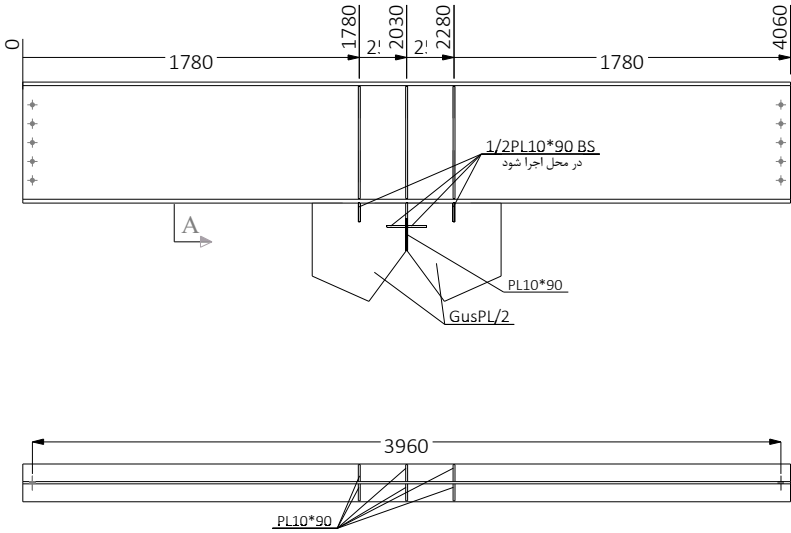




MATERIAL LIST FOR PG/204 N=2					
Mark	Profile	No.	Length	Area	Weight
pg/214	PL12*600	1	4060	5.0	229.5
1/2PL/1011	PL10*90	8	100	0.0	0.4
GusPL/2	PL15*520	2	500	0.5	25.1
Stf/19	PL10*90	6	595	0.1	4.2
Stf/20	PL10*90	2	250	0.1	1.8
pg/213	PL20*200	2	4060	1.8	127.5
Total			10.4	566.2	

TITLE		پل		پل	
CLIENT					
CONTRACTOR				ISSUED	
MODELLED BY		EN ALMASI		SCALE 1:25 1:40	
DRAWING No		[PG.204]		REVISION No. 0	

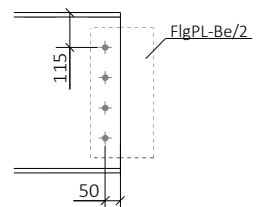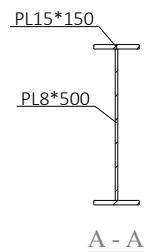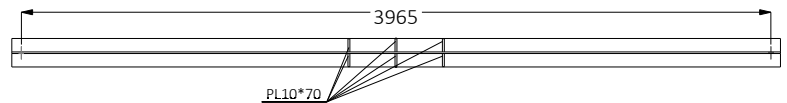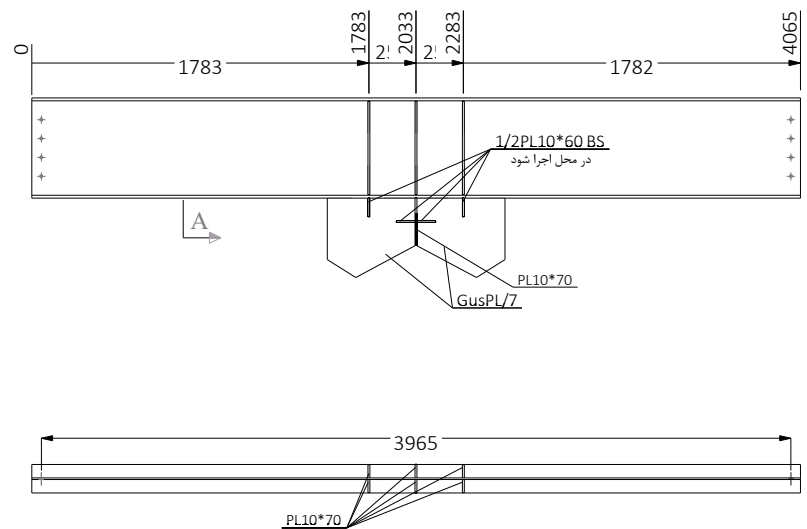

MATERIAL LIST FOR PG/205 N=2					
Mark	Profile	No.	Length	Area	Weight
pg/209	PL8*500	1	4065	4.1	127.6
1/2PL/1012	PL10*60	8	100	0.0	0.2
GusPL/7	PL15*420	2	470	0.4	19.2
Stf/21	PL10*70	6	495	0.1	2.7
Stf/22	PL10*70	2	250	0.0	1.4
pg/204	PL15*150	2	4065	1.3	71.8
Total				8.2	330.6


TITLE		پل		
CLIENT				
CONTRACTOR		ISSUED		
MODELLED BY	EN ALMASI	SCALE	1:25	1:40
DRAWING No	[PG.205]	REVISION No.	0	A4

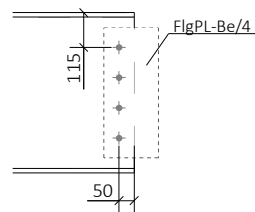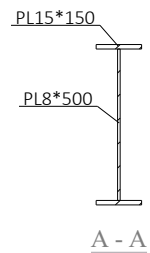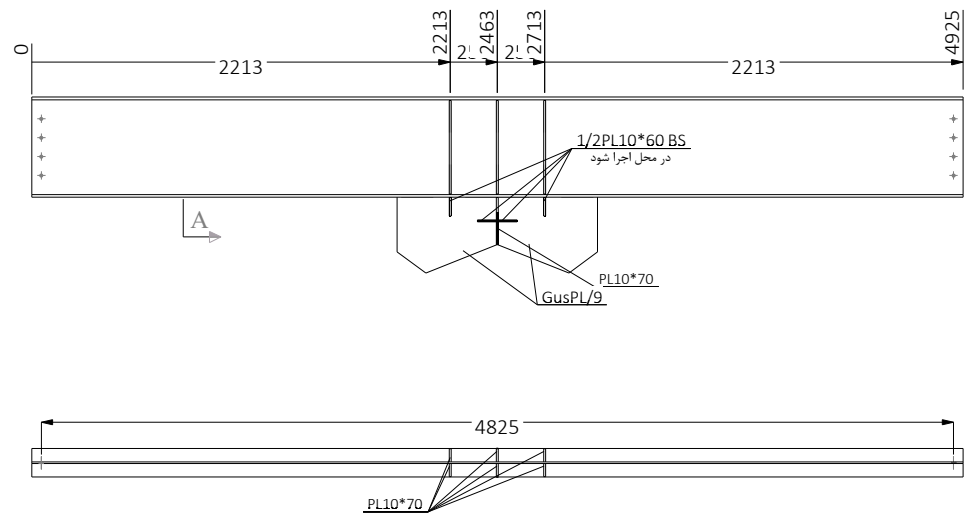


MATERIAL LIST FOR PG/206 N=2					
Mark	Profile	No.	Length	Area	Weight
pg/210	PL8*500	1	4925	5.0	154.6
1/2PL/1012	PL10*60	8	100	0.0	0.2
GusPL/9	PL15*400	2	530	0.4	20.6
Stf/21	PL10*70	6	495	0.1	2.7
Stf/22	PL10*70	2	250	0.0	1.4
pg/205	PL15*150	2	4925	1.6	87.0
Total			9.7	390.8	

TITLE		پل		
CLIENT				
CONTRACTOR		ISSUED		
MODELLED BY	EN ALMASI	SCALE	1:25	1:40
DRAWING No	[PG.206]	REVISION No.	0	A4




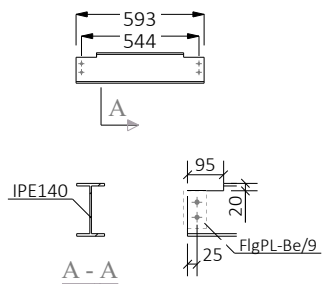


No. 6, Marked B14/1

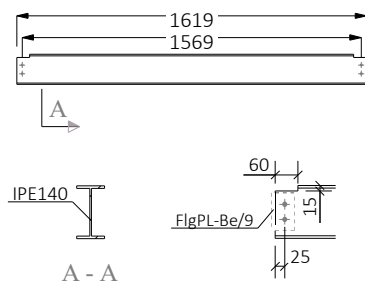

No. 2, Marked B14/2

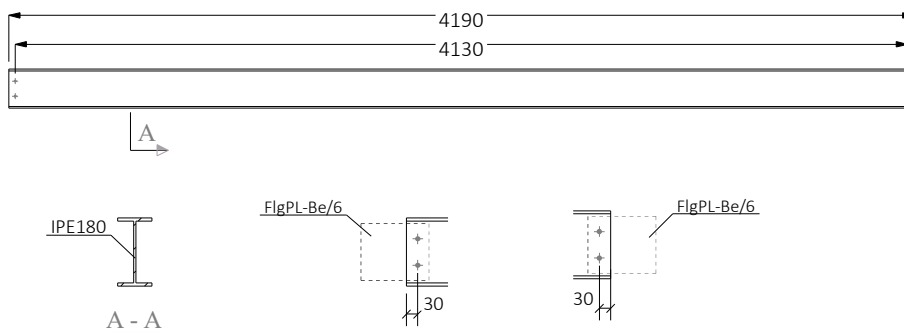


No. 4, Marked B18/1

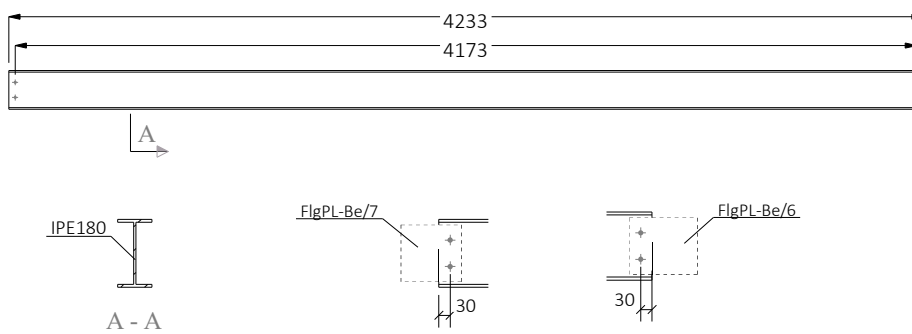


No. 2, Marked B18/2


TITLE		تیر ۱۸، ۱۴		
CLIENT				
CONTRACTOR		ISSUED		
MODELLED BY	EN ALMASI	SCALE	1:20	1:35
DRAWING No	[4]	REVISION No.	0	A4

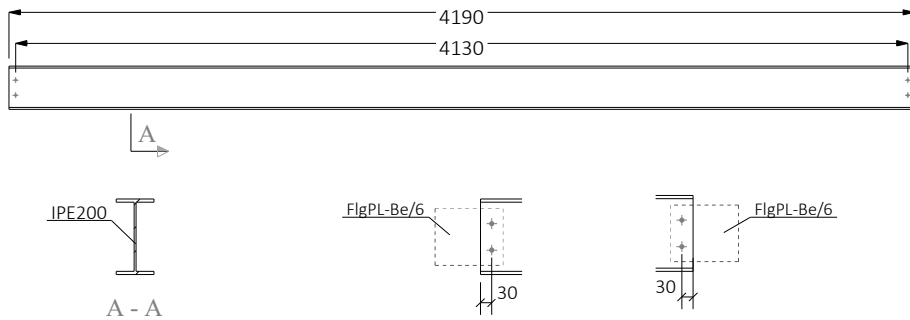

No. 2, Marked B20/1




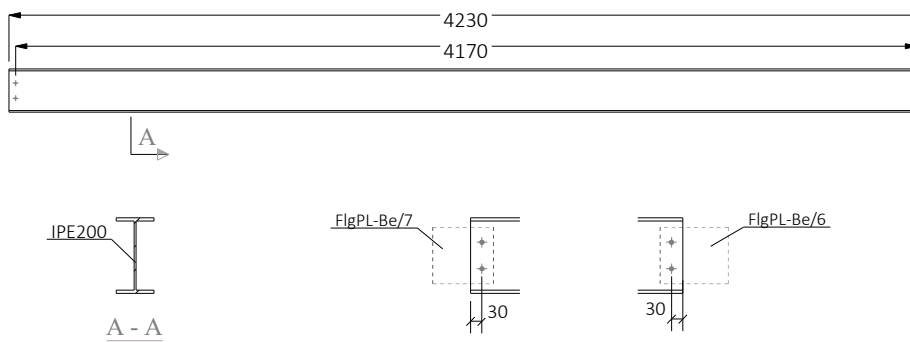


No. 2, Marked B20/2




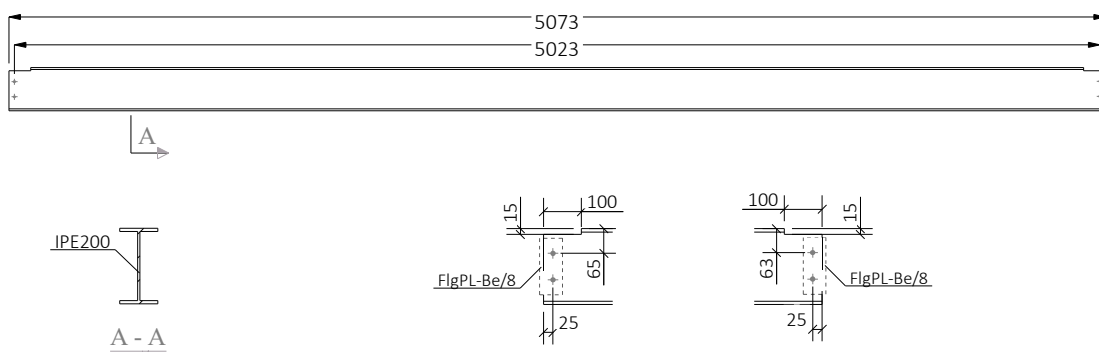


No. 2, Marked B20/3





TITLE		تیر ۱-۲۰			
CLIENT					
CONTRACTOR		ISSUED			
MODELLED BY	EN ALMASI	SCALE	1:20	1:35	A4
DRAWING No	[5]	REVISION No.	0		

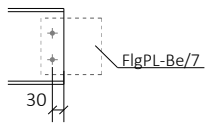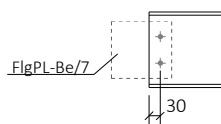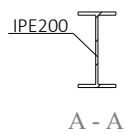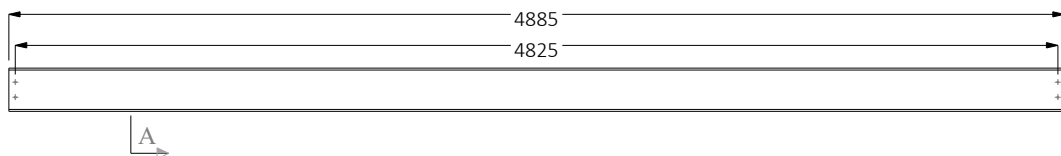

No. 1, Marked B20/4

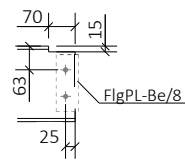
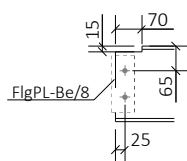
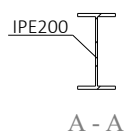
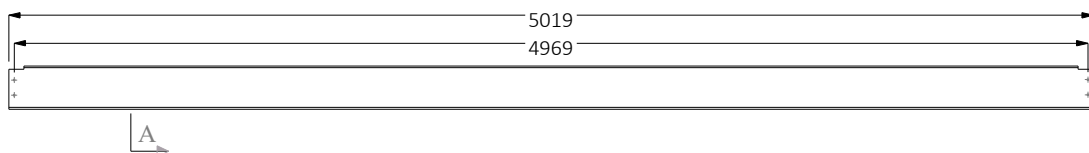


No. 1, Marked B20/5

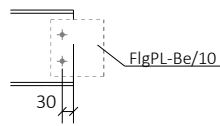
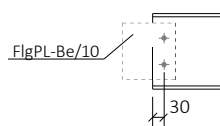
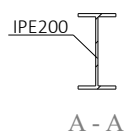
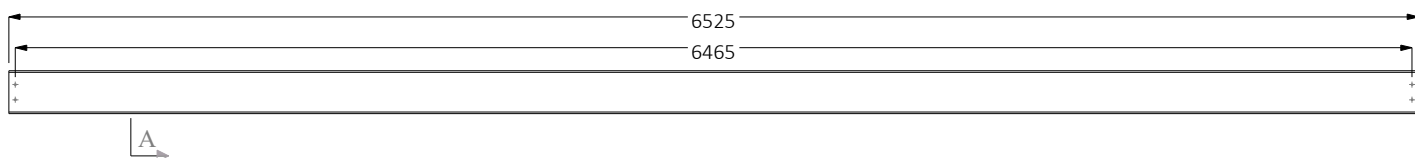


No. 2, Marked B20/6





TITLE		تیر ۲-۲۰		
CLIENT				
CONTRACTOR		ISSUED		
MODELLED BY	EN ALMASI	SCALE	1:20	1:35
DRAWING No	[6]	REVISION No.	0	A4

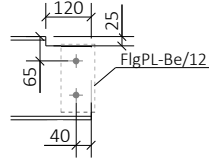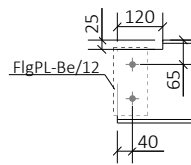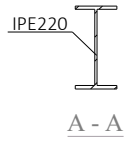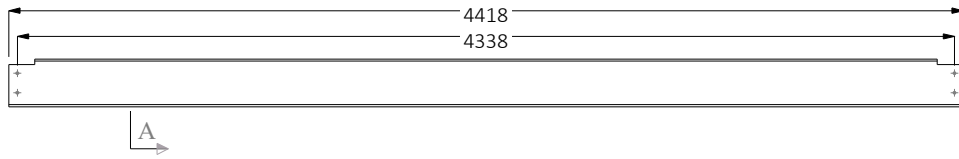

No. 30, Marked B22/1

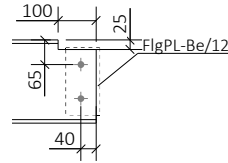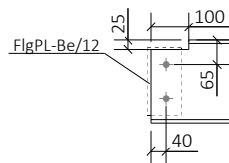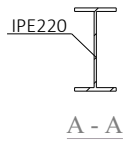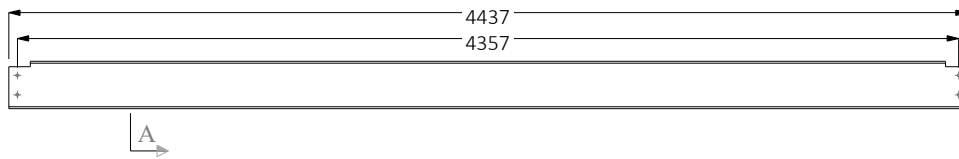


No. 4, Marked B22/2

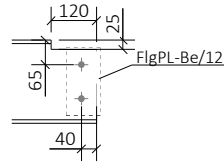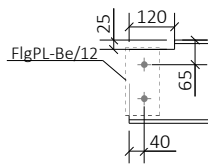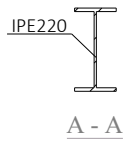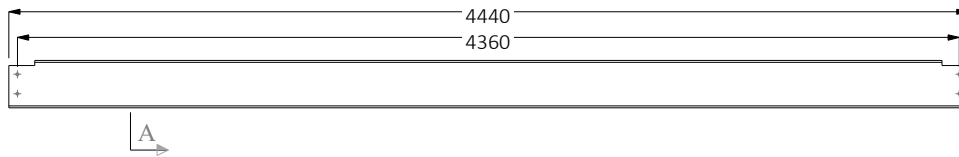


No. 8, Marked B22/3


TITLE		تیر ۱-۳۳		
CLIENT				
CONTRACTOR		ISSUED		
MODELLED BY	EN ALMASI	SCALE	1:20 1:35	
DRAWING No	[7]	REVISION No.	0	A4

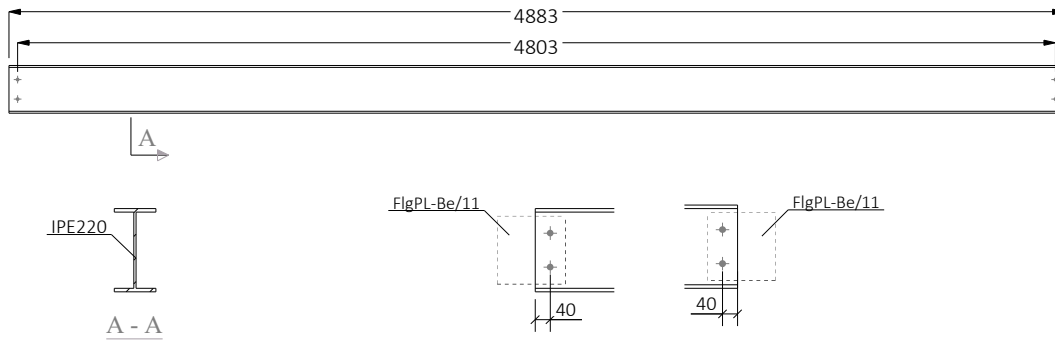


No. 8, Marked B22/4

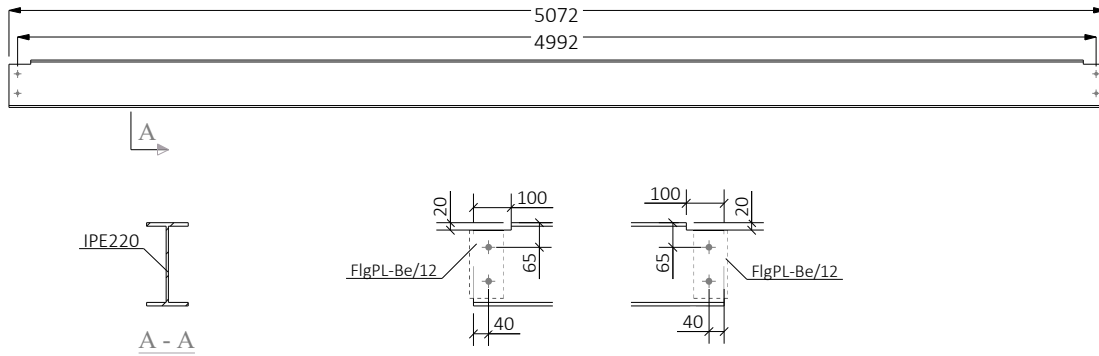

No. 7, Marked B22/5

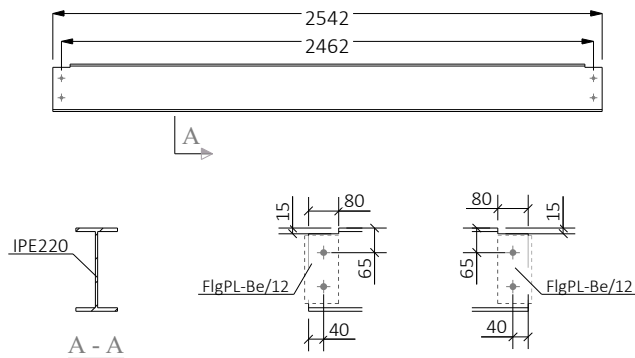


No. 2, Marked B22/6

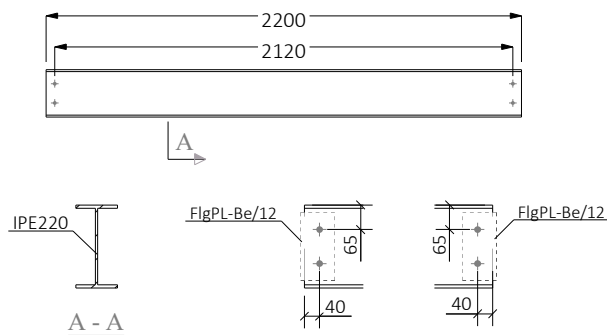


No. 1, Marked B22/7


TITLE		تیر ۲-۲		
CLIENT				
CONTRACTOR		ISSUED		
MODELLED BY	EN ALMASI	SCALE	1:20 1:35	A4
DRAWING No	[8]	REVISION No.	0	

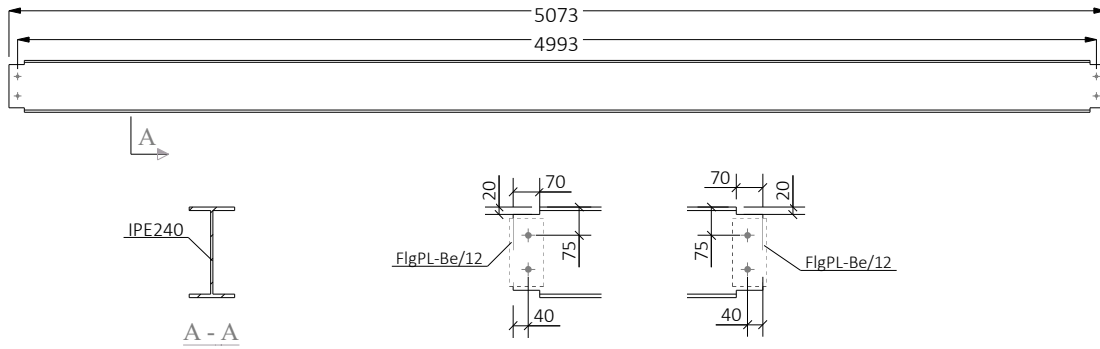

No. 2, Marked B24/1




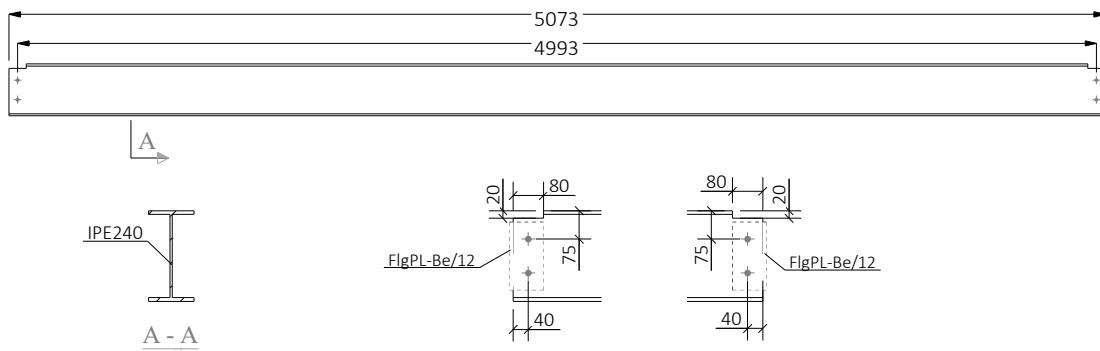


No. 3, Marked B24/2





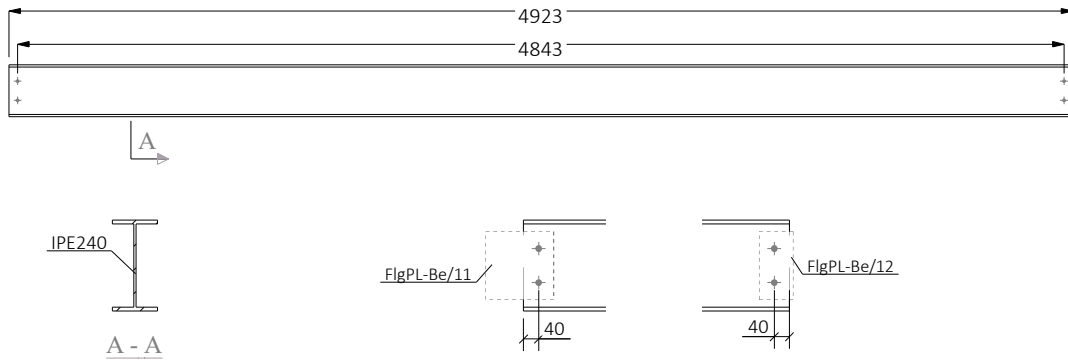


No. 1, Marked B24/3

TITLE		تير ۱-۴۴		
CLIENT				
CONTRACTOR		ISSUED		
MODELLED BY	EN ALMASI	SCALE	1:20	1:35
DRAWING No	[9]	REVISION No.	0	A4

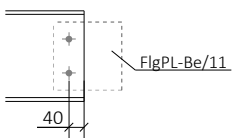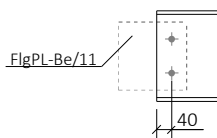
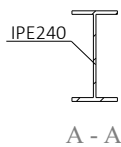
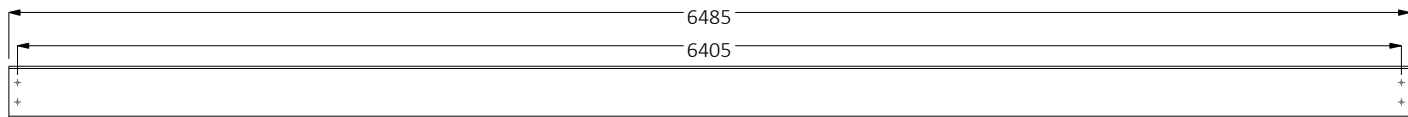


No. 3, Marked B24/4

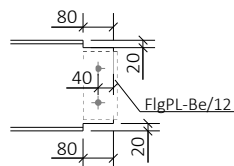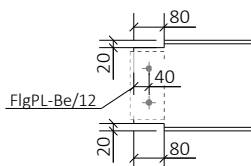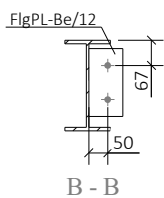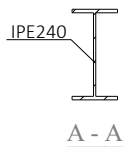
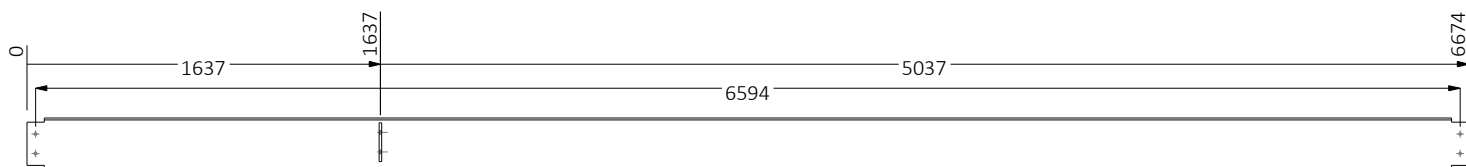


No. 2, Marked B24/5




TITLE		تیر ۲-۴		
CLIENT				
CONTRACTOR		ISSUED		
MODELLED BY	EN ALMASI	SCALE	1:20 1:35	A4
DRAWING No	[10]	REVISION No.	0	

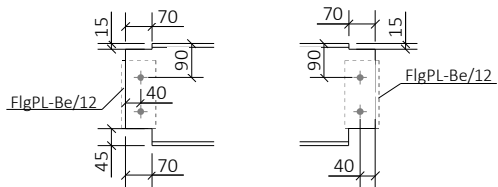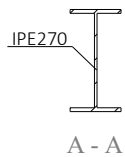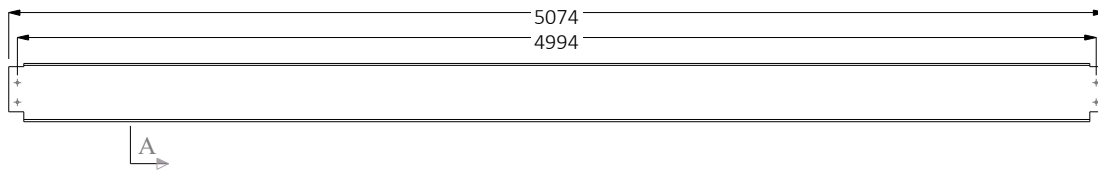

No. 1, Marked B27/1

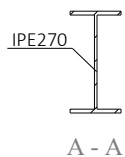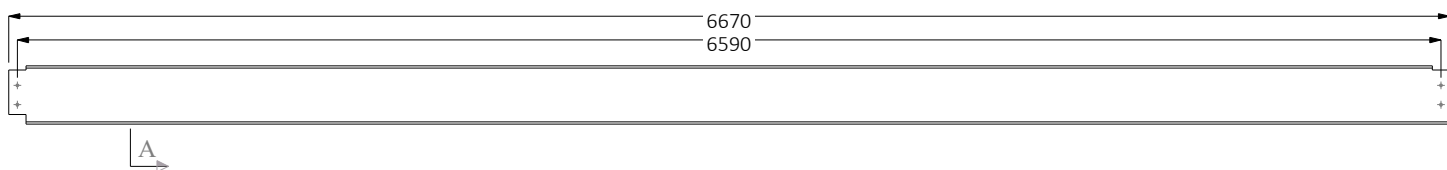


No. 6, Marked B27/2

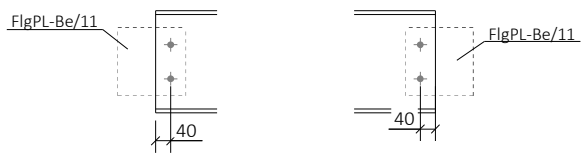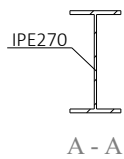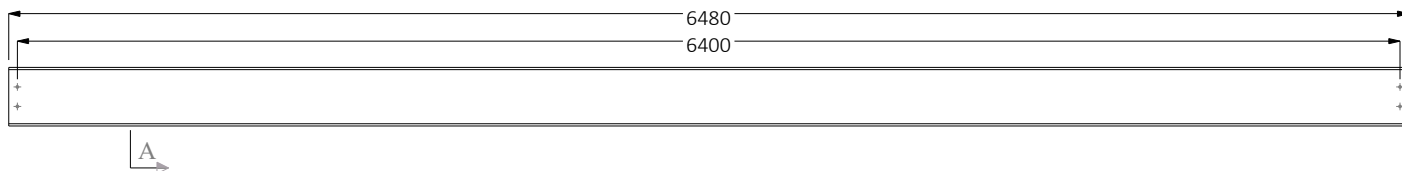


No. 3, Marked B27/3


TITLE		تیر ۱-۲۷		
CLIENT				
CONTRACTOR		ISSUED		
MODELLED BY	EN ALMASI	SCALE	1:20	1:35
DRAWING No	[11]	REVISION No.	0	A4

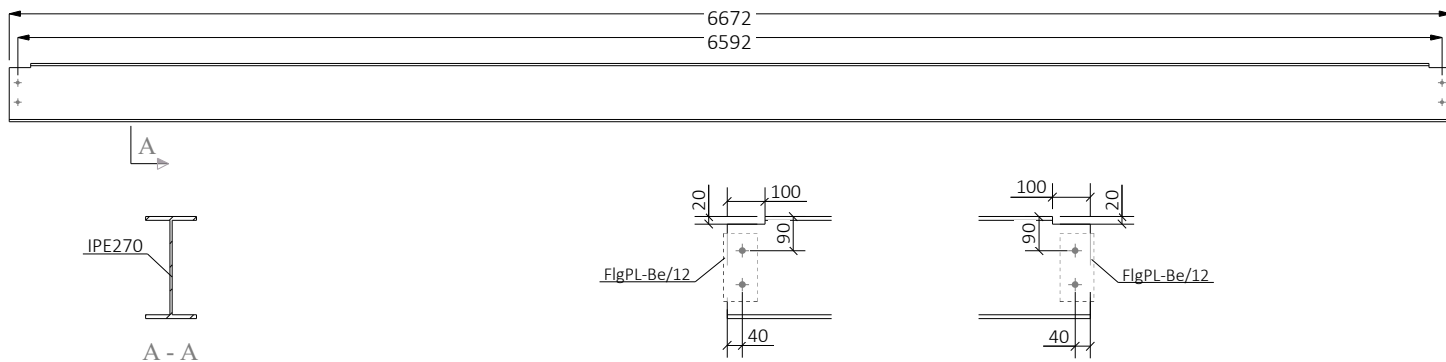

No. 6, Marked B27/4

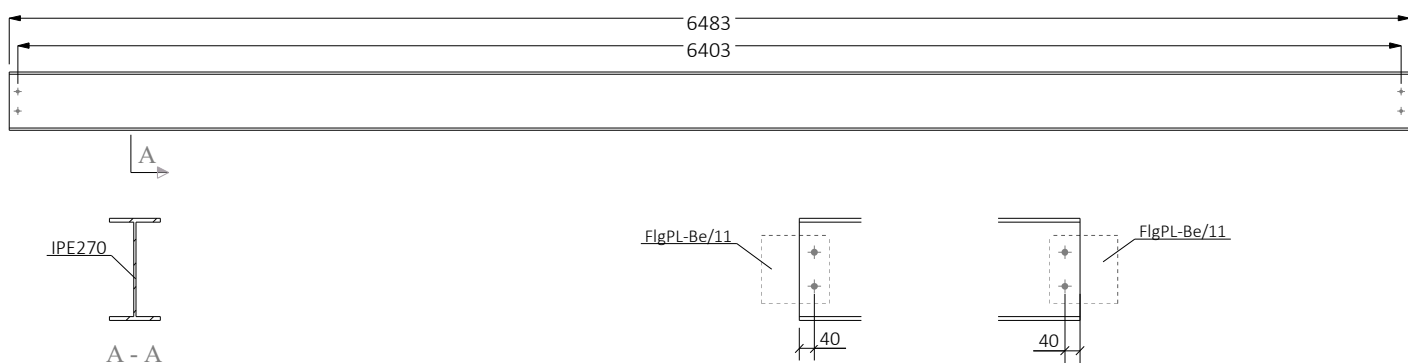


No. 2, Marked B27/5

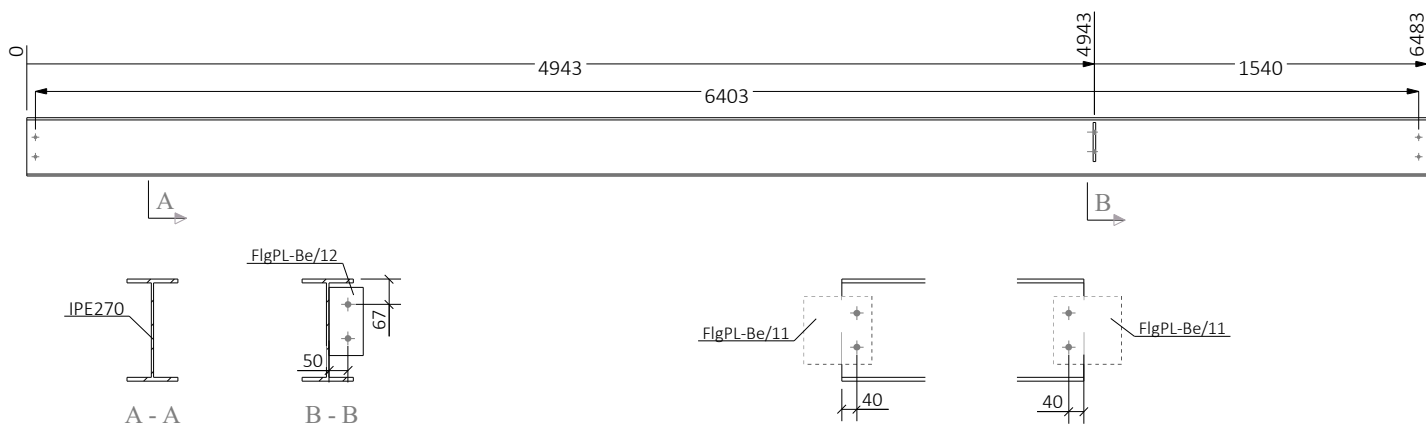


No. 1, Marked B27/6


TITLE		تیر ۲-۲۷		
CLIENT				
CONTRACTOR		ISSUED		
MODELLED BY	EN ALMASI	SCALE	1:20 1:35	A4
DRAWING No	[12]	REVISION No.	0	

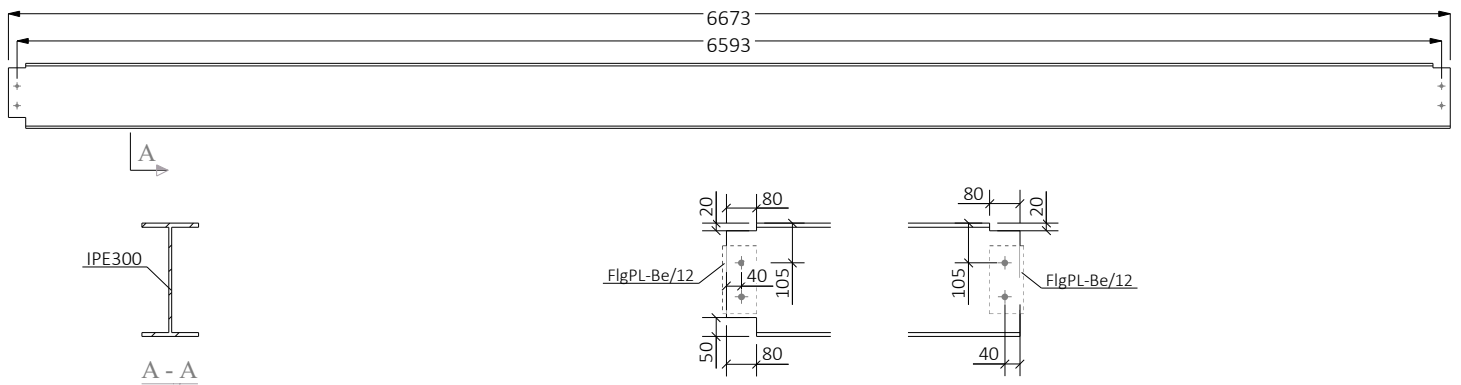


No. 3, Marked B30/1

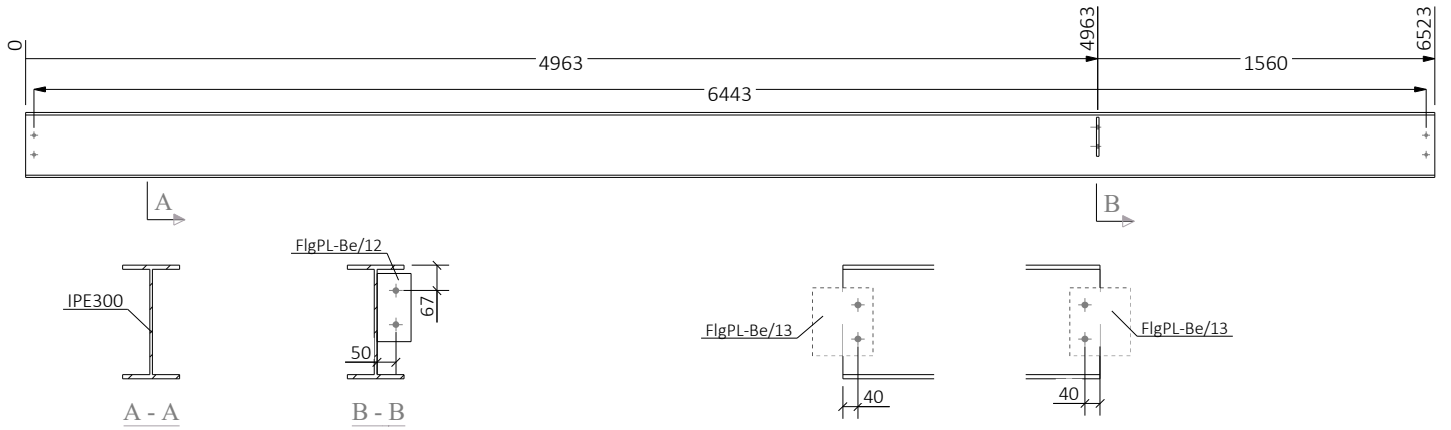

No. 1, Marked B30/2

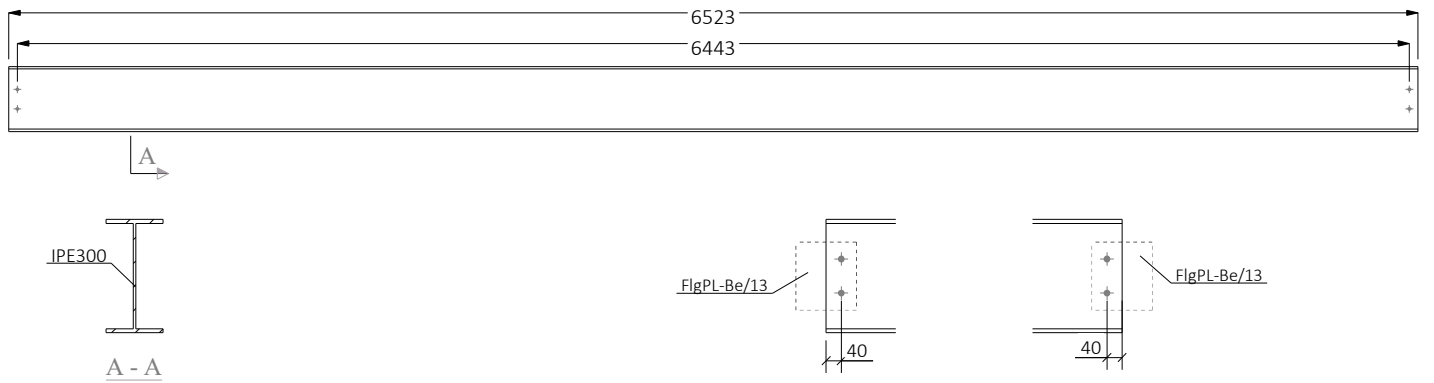


No. 1, Marked B30/3

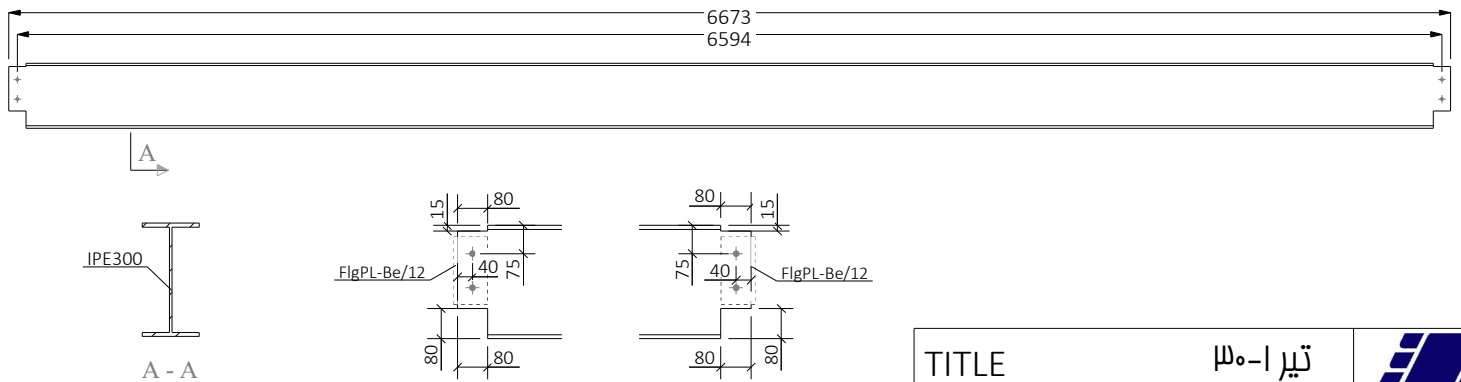


No. 1, Marked B30/4


TITLE		تیر ۱-۳۰		
CLIENT				
CONTRACTOR		ISSUED		
MODELLED BY	EN ALMASI	SCALE	1:20	1:35
DRAWING No	[13]	REVISION No.	0	A4

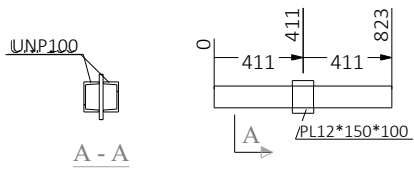


No. 2, Marked Br10/1

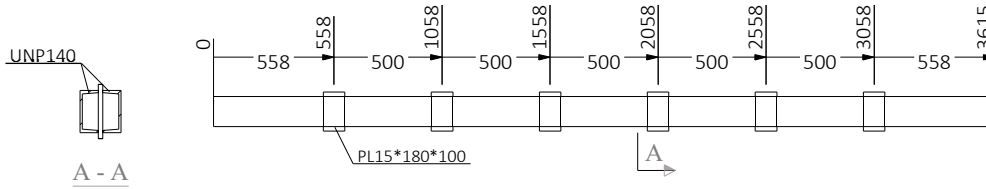


No. 4, Marked Br14/1

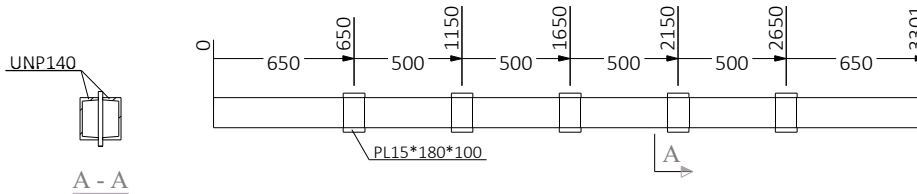


No. 4, Marked Br14/2

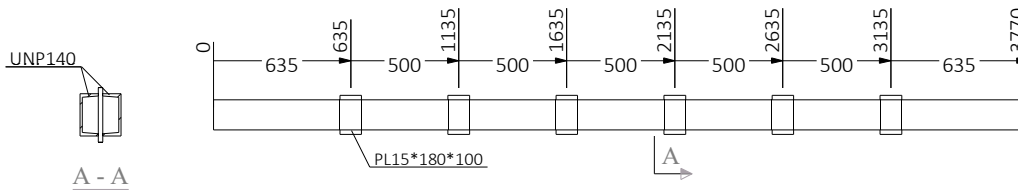

No. 4, Marked Br14/3






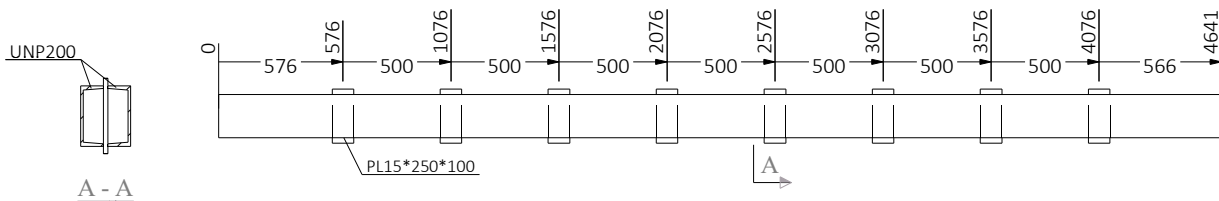


No. 4, Marked Br20/1

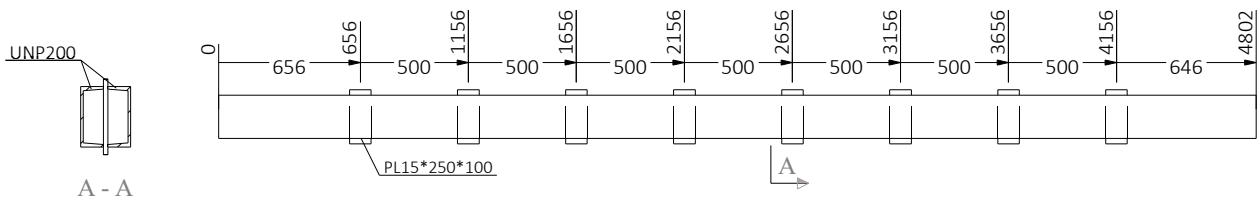







No. 4, Marked Br20/2

TITLE		مها ريند		
CLIENT				
CONTRACTOR		ISSUED		
MODELLED BY	EN ALMASI	SCALE	1:25 1:35	
DRAWING No	[14]	REVISION No.	0	A4

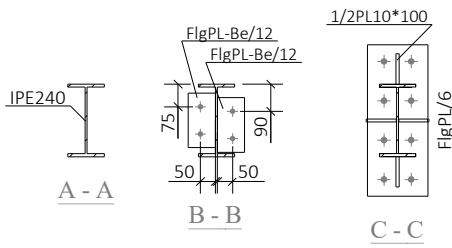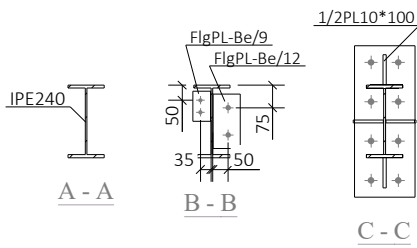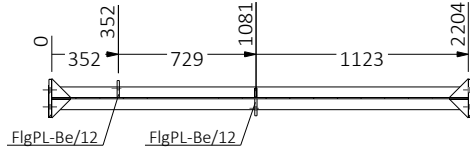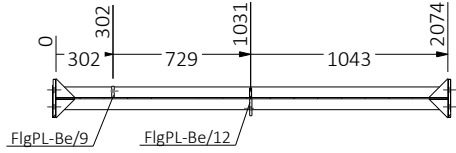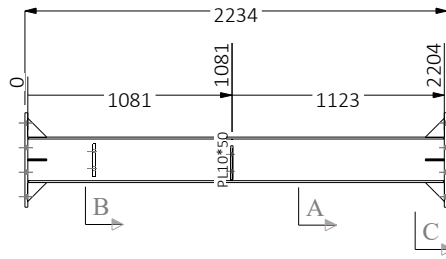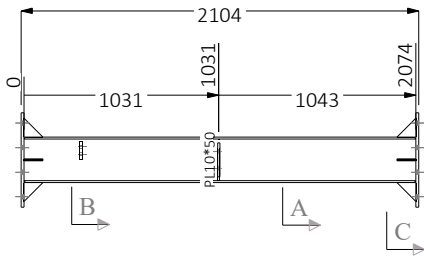

No. 1, Marked P24/1






No. 1, Marked P24/3

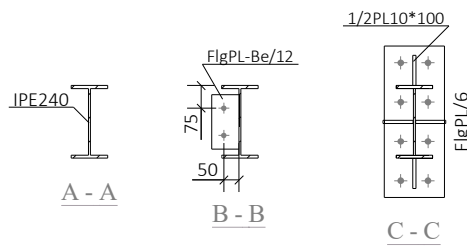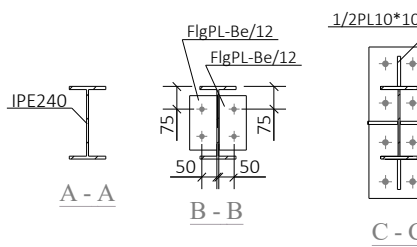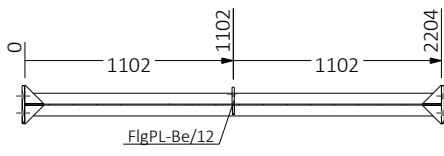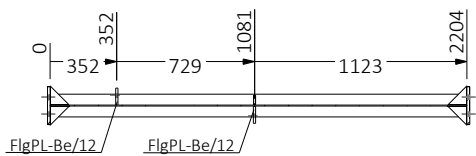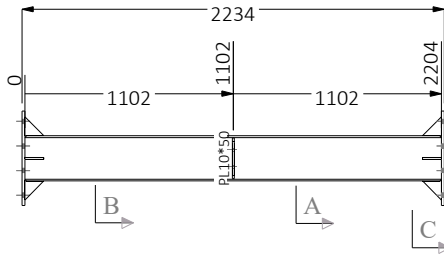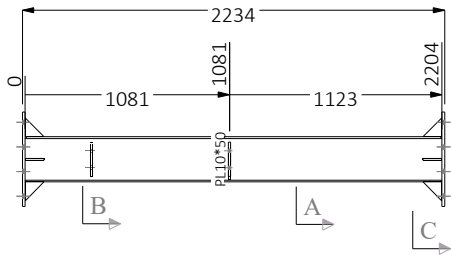


No. 1, Marked P24/2

No. 2, Marked P24/4




TITLE		پل -۱		
CLIENT				
CONTRACTOR		ISSUED		
MODELLED BY	EN ALMASI	SCALE	1:25	1:40
DRAWING No	[15]	REVISION No.	0	A4

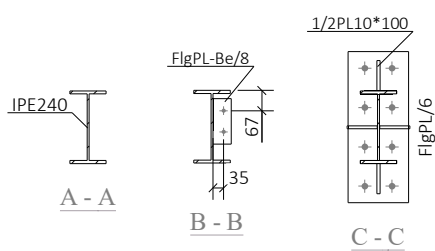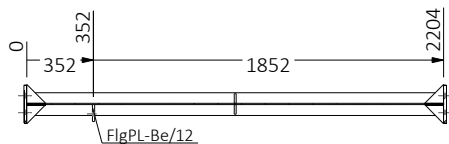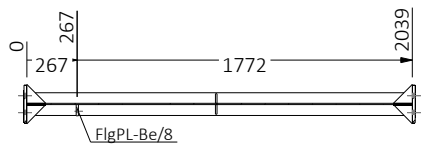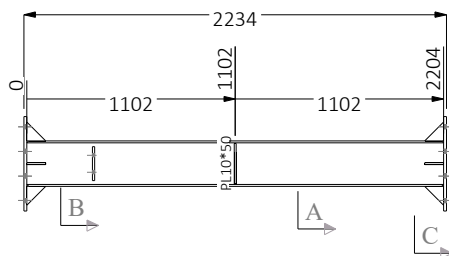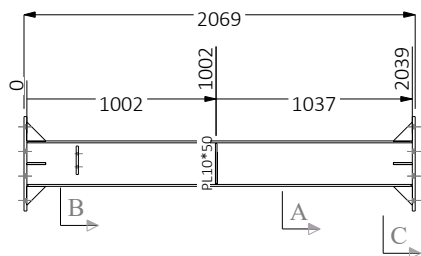

No. 1, Marked P24/5






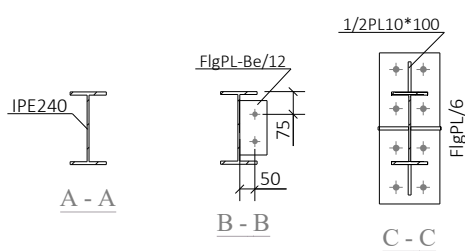


No. 1, Marked P24/7

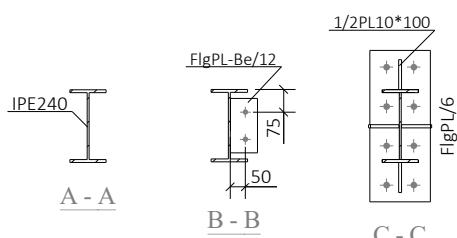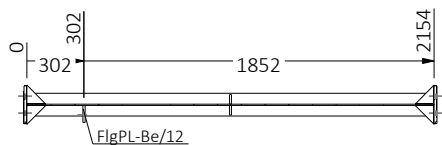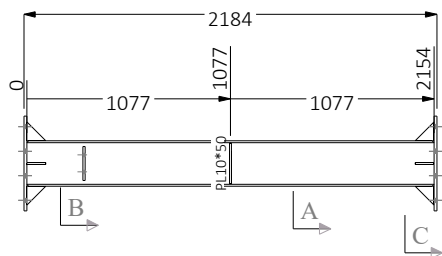







No. 1, Marked P24/6

TITLE			پل-پ		
CLIENT					
CONTRACTOR		ISSUED			
MODELLED BY	EN ALMASI	SCALE	1:25	1:40	A4
DRAWING No	[16]	REVISION No.	0		

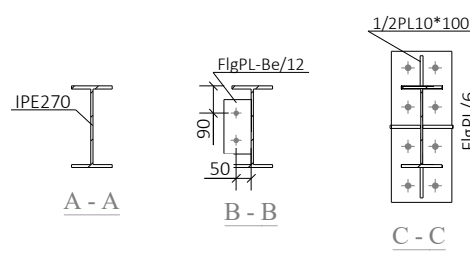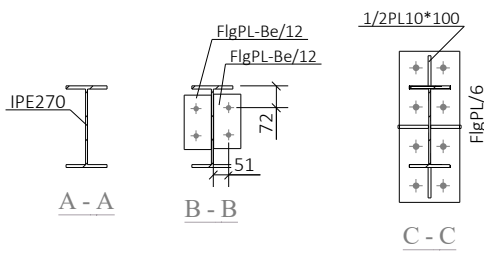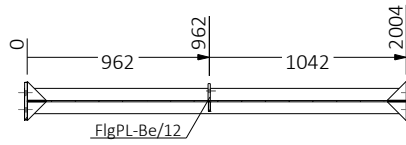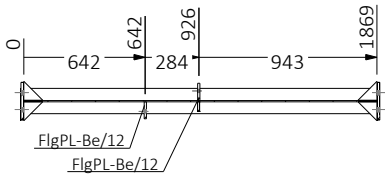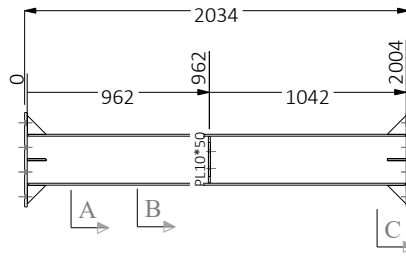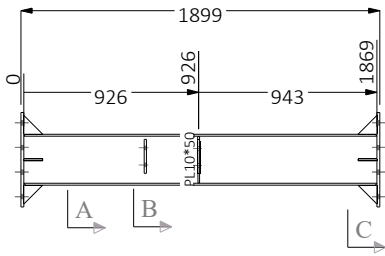

No. 1, Marked P27/1




No. 1, Marked P27/3

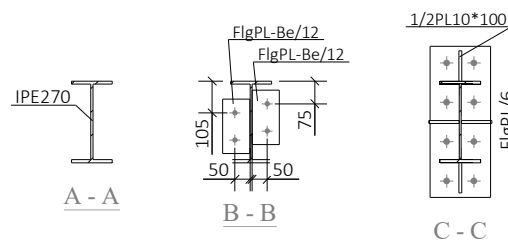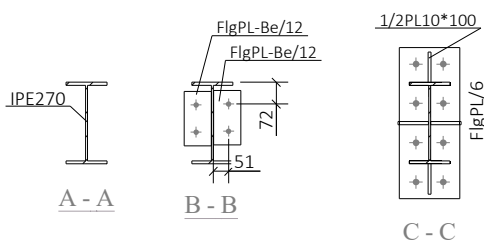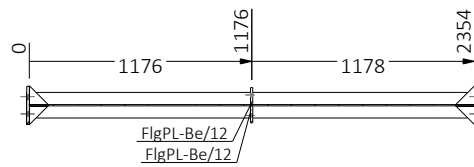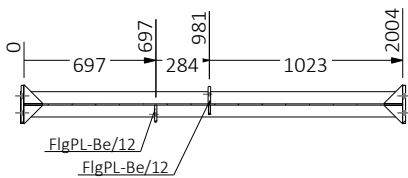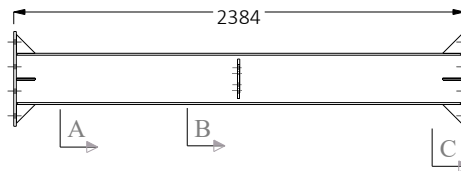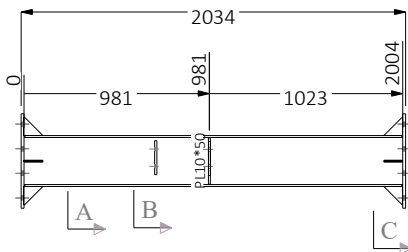




No. 1, Marked P27/2

No. 1, Marked P27/4




TITLE			پل -۱ PV-I		
CLIENT					
CONTRACTOR			ISSUED		
MODELLED BY		EN ALMASI		SCALE	1:25 1:40
DRAWING No		[17]		REVISION No.	0
					A4

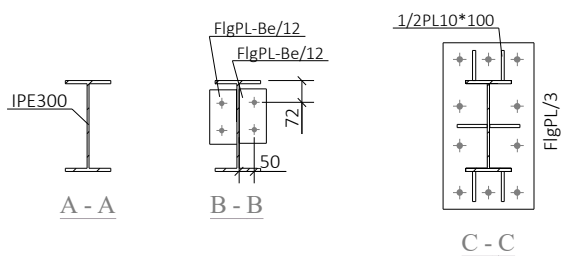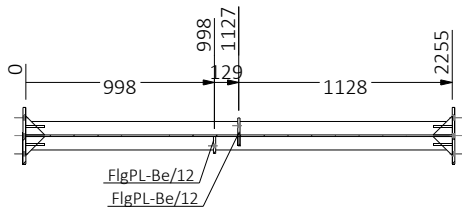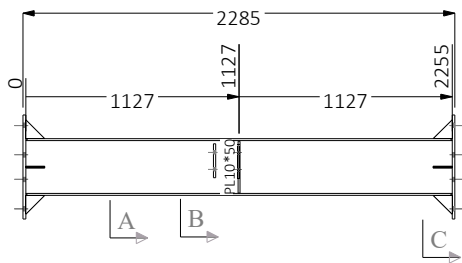




No. 1, Marked P30/1

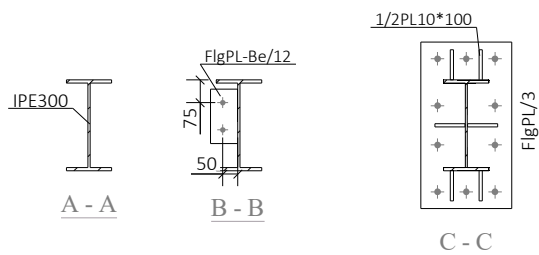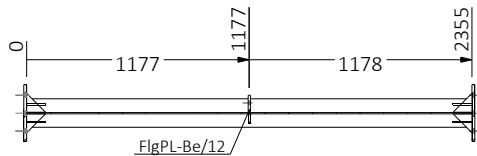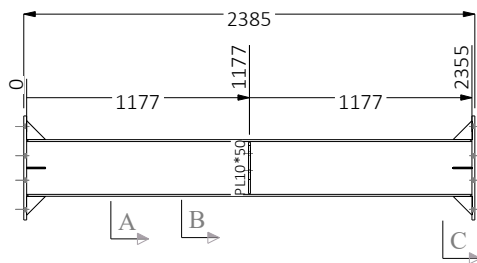

No. 1, Marked P30/3

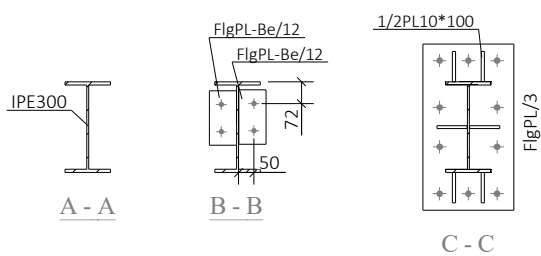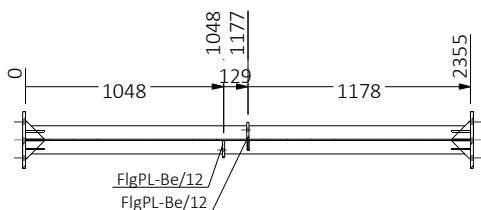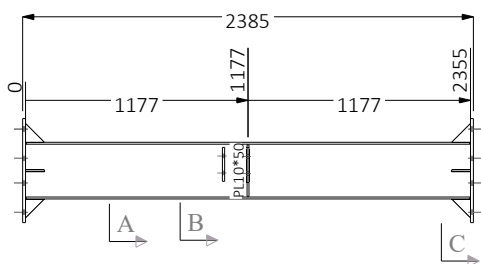


No. 1, Marked P30/2

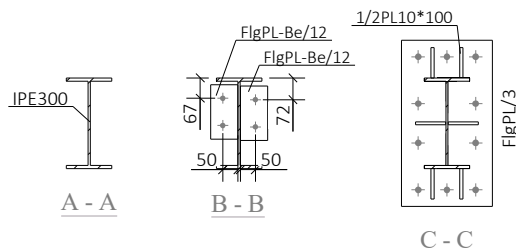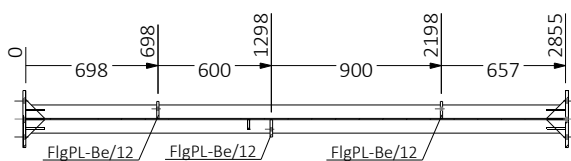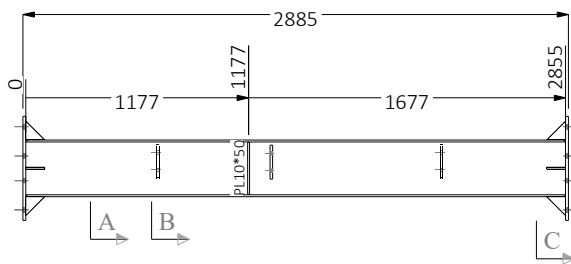


No. 1, Marked P30/4


TITLE		پل - ا-۳۵		
CLIENT				
CONTRACTOR		ISSUED		
MODELLED BY	EN ALMASI	SCALE	1:25 1:40	A4
DRAWING No	[18]	REVISION No.	0	

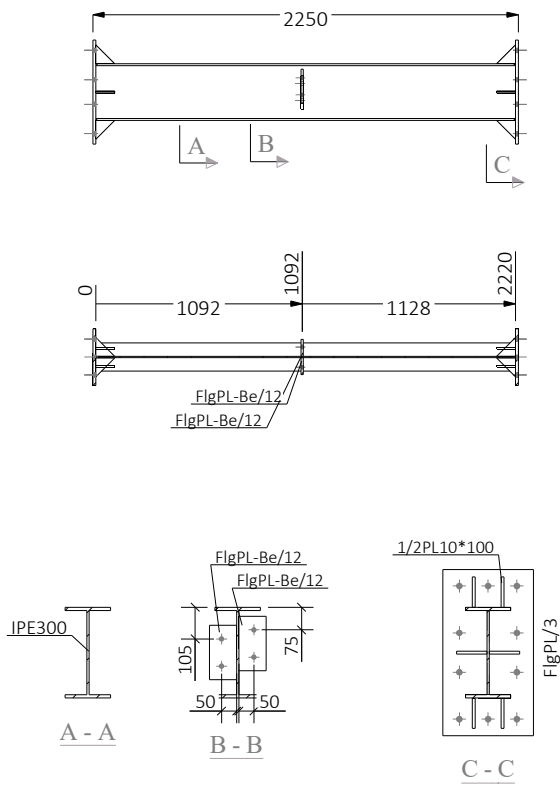

No. 1, Marked P30/5

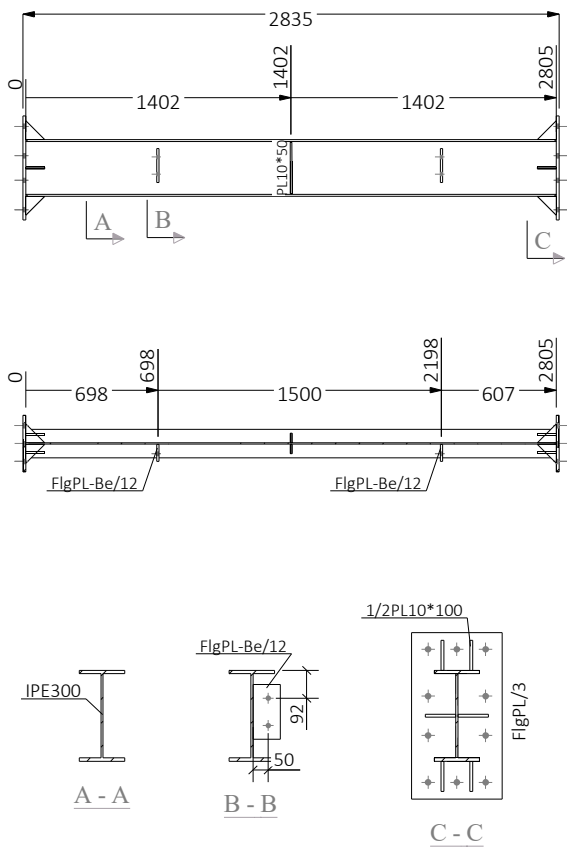


No. 1, Marked P30/7

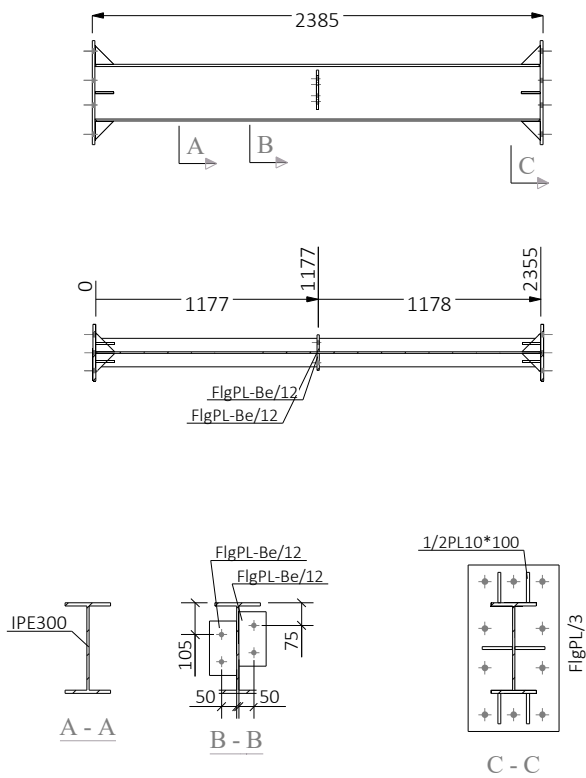


No. 1, Marked P30/6


TITLE		پل-۲		
CLIENT				
CONTRACTOR		ISSUED		
MODELLED BY	EN ALMASI	SCALE	1:25 1:40	A4
DRAWING No	[19]	REVISION No.	0	

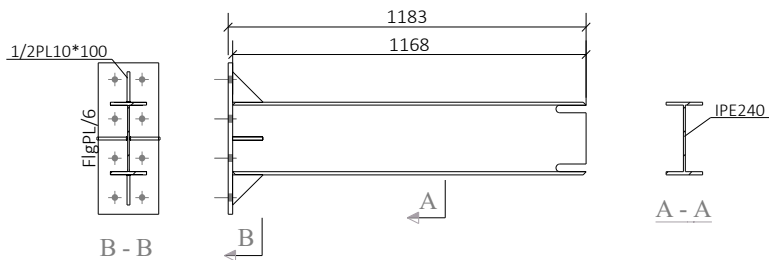


No. 6, Marked P24/1001

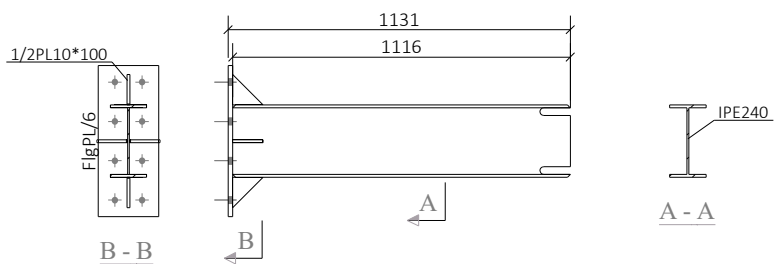


No. 2, Marked P24/1002

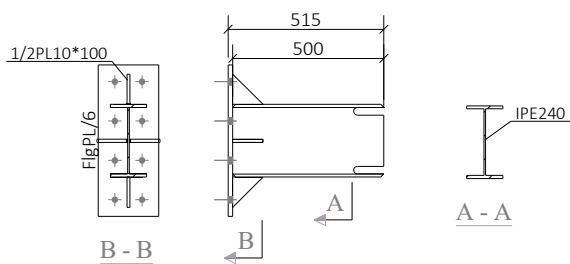


No. 16, Marked P24/1003

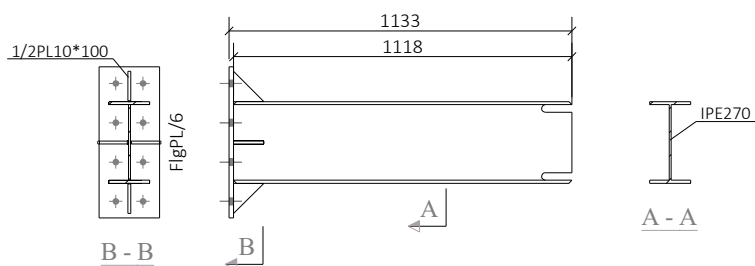


No. 2, Marked P27/1003

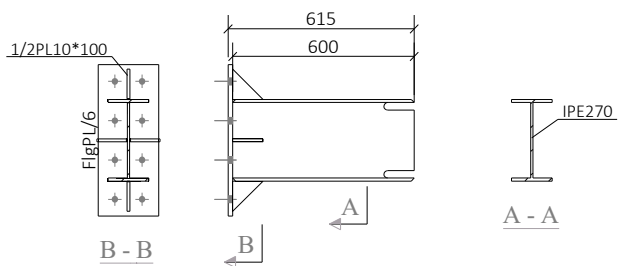

No. 8, Marked P27/1001

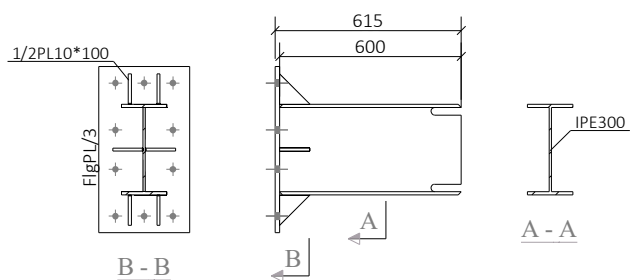


No. 14, Marked P30/1001

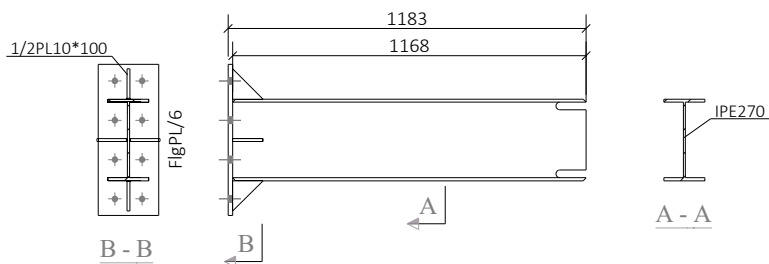


No. 2, Marked P27/1002


TITLE		دستک تیرآه		
CLIENT				
CONTRACTOR		ISSUED		
MODELLED BY	EN ALMASI	SCALE 1:25		
DRAWING No	[20]	REVISION No.	0	
				A4

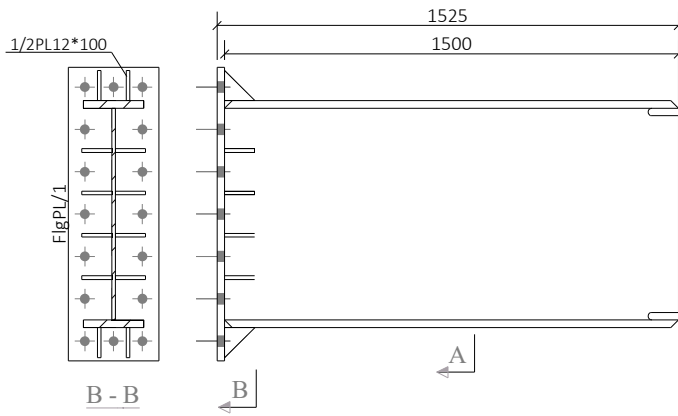


No. 12, Marked PG/1001

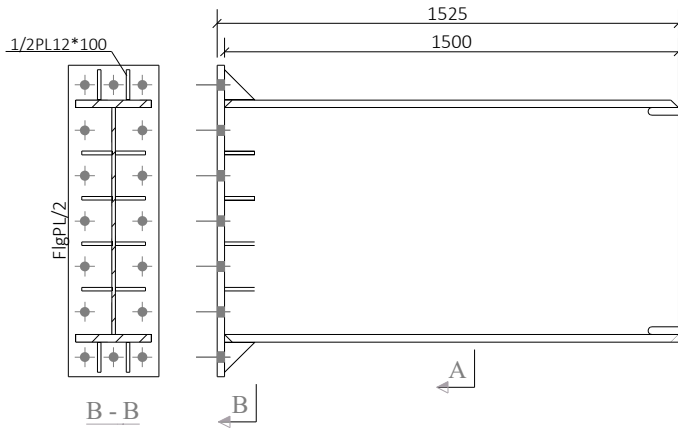


No. 2, Marked PG/1002

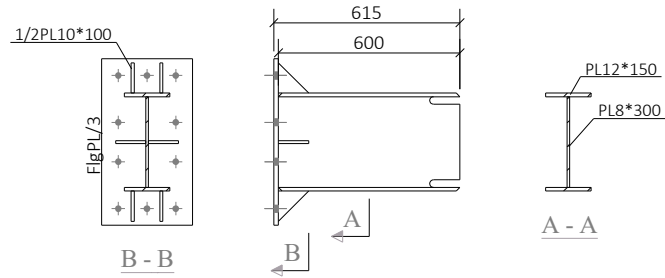


No. 6, Marked PG/1003

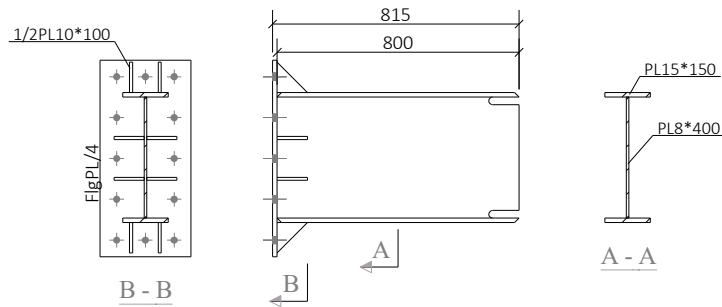


No. 8, Marked PG/1004

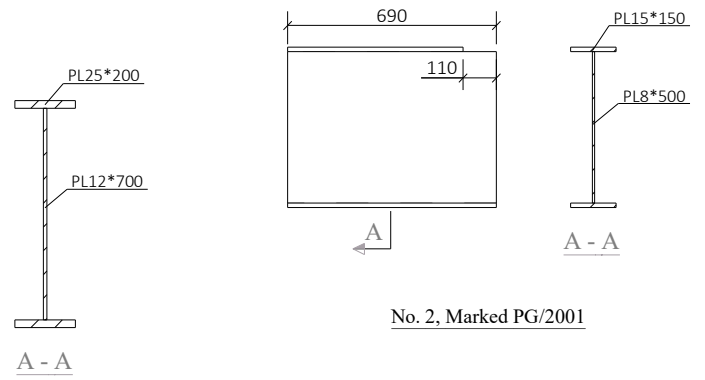


No. 2, Marked PG/2001

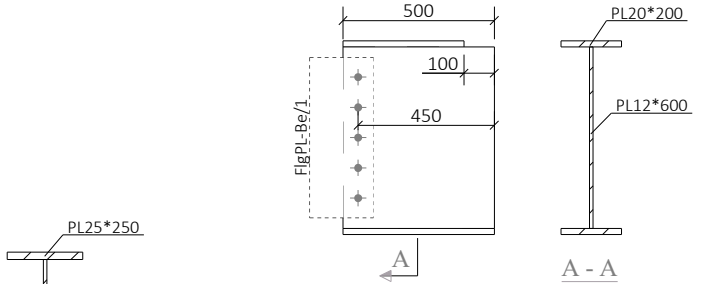

No. 8, Marked PG/2002

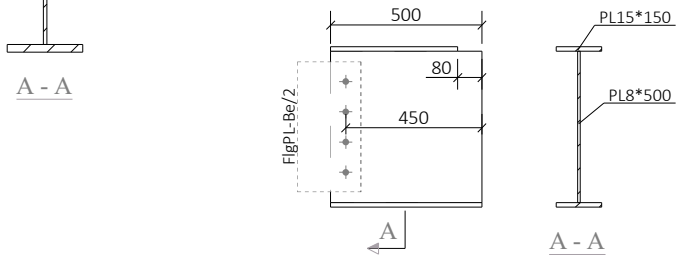


No. 4, Marked PG/2003

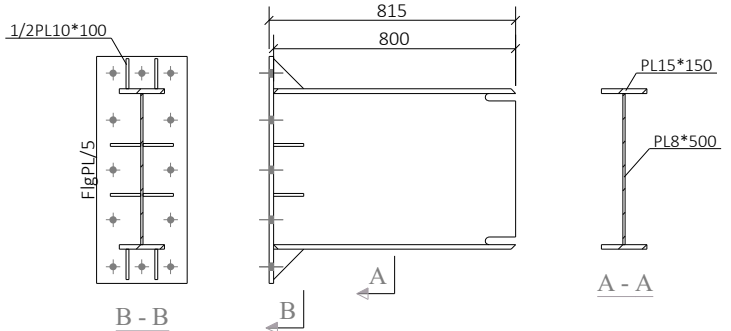


No. 6, Marked PG/1005


TITLE			
دستک پل			
CLIENT			
CONTRACTOR		ISSUED	
MODELLED BY	EN ALMASI	SCALE	1:25
DRAWING No	[21]	REVISION No.	0

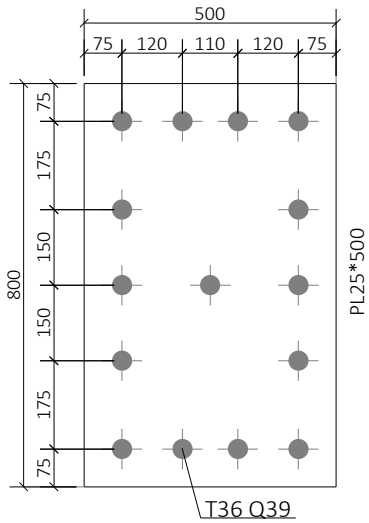


No. 2, Marked BaPL/1

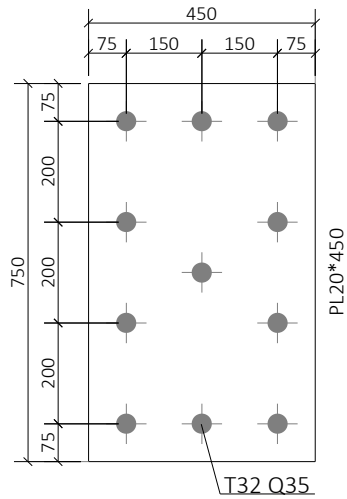


No. 9, Marked BaPL/4

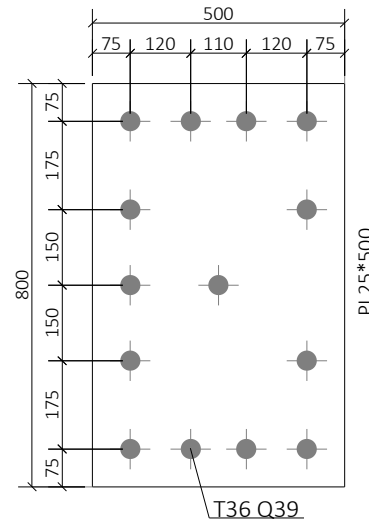


No. 4, Marked BaPL/11

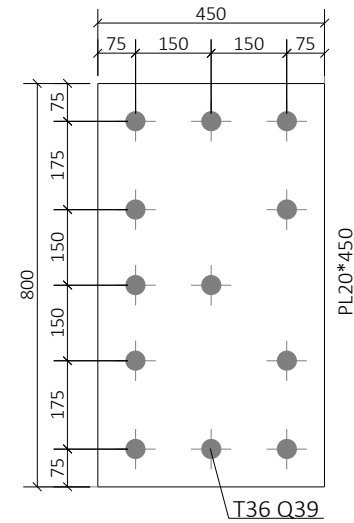

No. 4, Marked BaPL/21

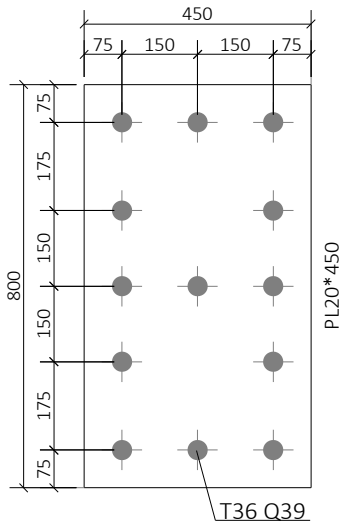


No. 3, Marked BaPL/2

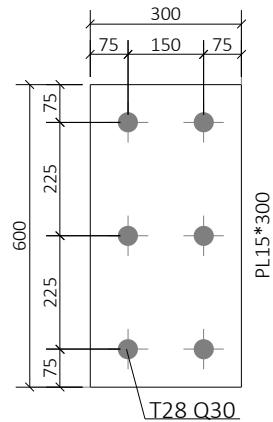


No. 2, Marked BaPL/3


TITLE		کف ستون			
CLIENT					
CONTRACTOR			ISSUED		
MODELLED BY		EN ALMASI		SCALE 1:15	A4
DRAWING No		[22]		REVISION No. 0	

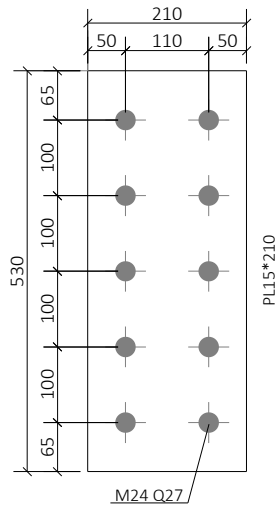


No. 8, Marked FlgPL-Bc/1

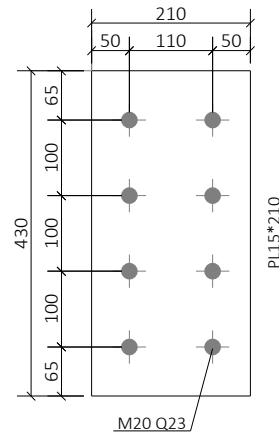


No. 4, Marked FlgPL-Bc/2

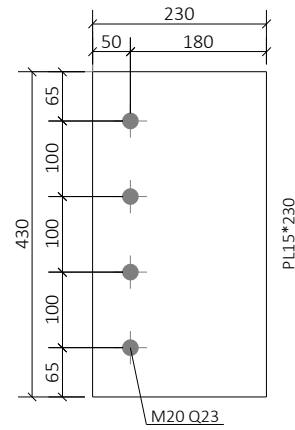


No. 4, Marked FlgPL-Bc/3

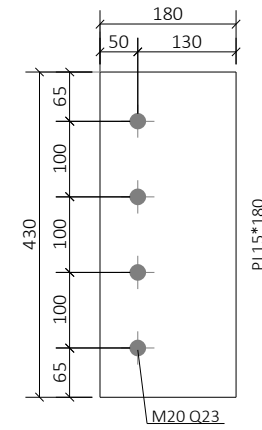


No. 4, Marked FlgPL-Bc/4

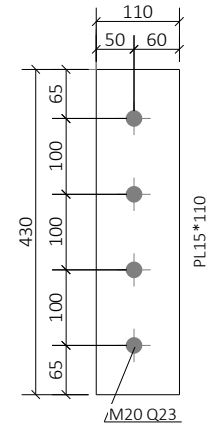


No. 2, Marked FlgPL-Bc/5

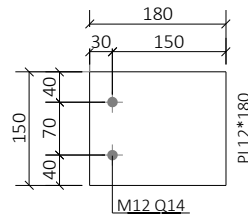


No. 16, Marked FlgPL-Bc/6

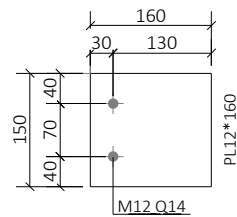


No. 6, Marked FlgPL-Bc/7

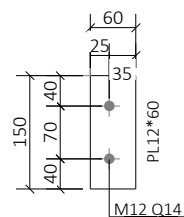


No. 6, Marked FlgPL-Bc/8

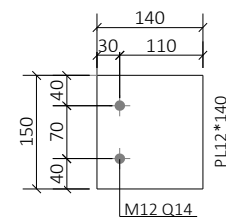


No. 4, Marked FlgPL-Bc/10

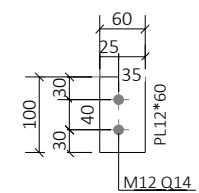


No. 16, Marked FlgPL-Bc/9

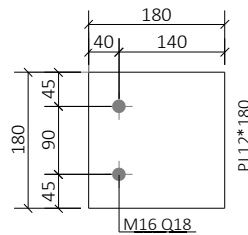

No. 35, Marked FlgPL-Bc/11

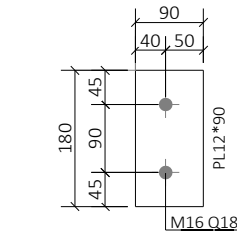


No. 153, Marked FlgPL-Bc/12

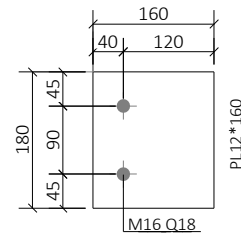


No. 4, Marked FlgPL-Bc/13


TITLE		پلاک تیر		
CLIENT				
CONTRACTOR		ISSUED		
MODELLED BY	EN ALMASI	SCALE 1:10		A4
DRAWING No	[23]	REVISION No. 0		

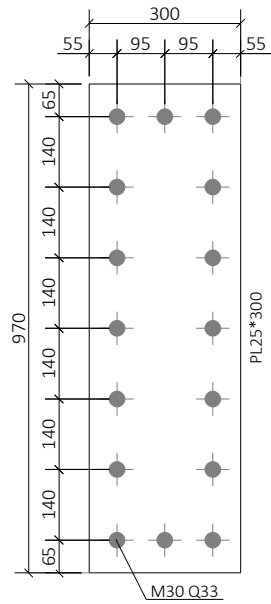


No. 24, Marked FlgPL/1

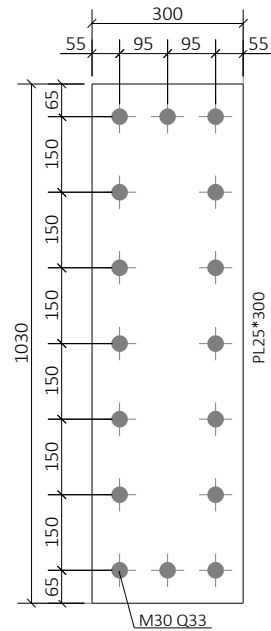


No. 4, Marked FlgPL/2

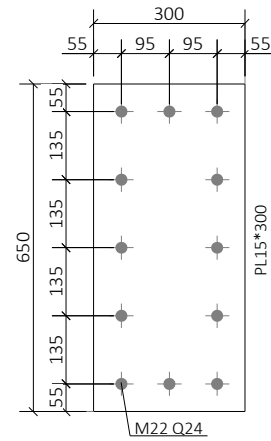


No. 16, Marked FlgPL/4

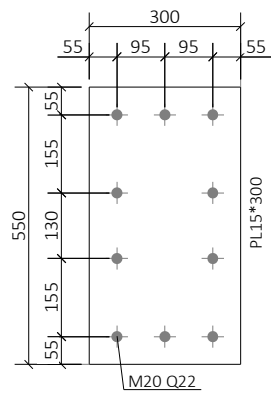

No. 40, Marked FlgPL/3

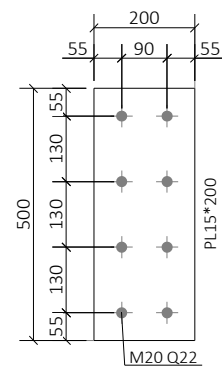


No. 60, Marked FlgPL/6

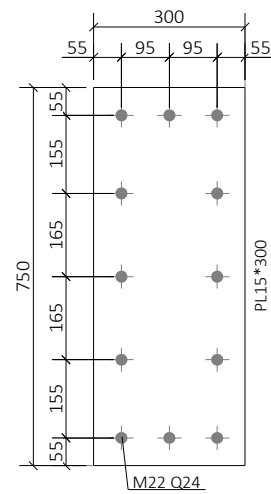


No. 12, Marked FlgPL/5


TITLE		فلنج	
CLIENT			
CONTRACTOR		ISSUED	
MODELLED BY	EN ALMASI	SCALE 1:15	A4
DRAWING No	[24]	REVISION No. 0	

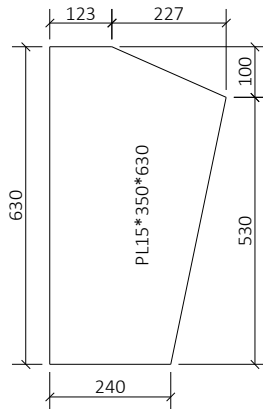


No. 4, Marked GusPL/1

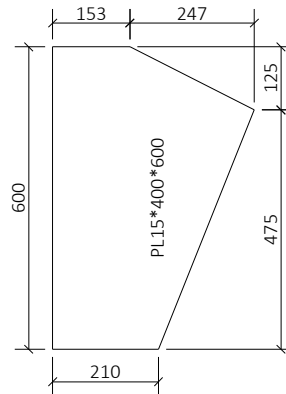


No. 4, Marked GusPL/3

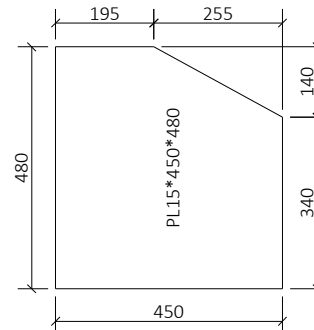


No. 4, Marked GusPL/5

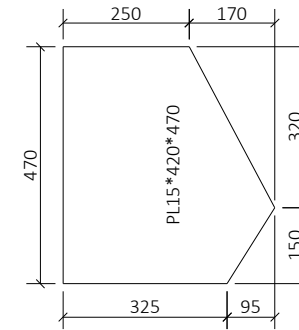


No. 4, Marked GusPL/7

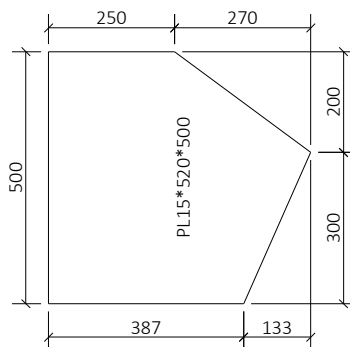


No. 8, Marked GusPL/2

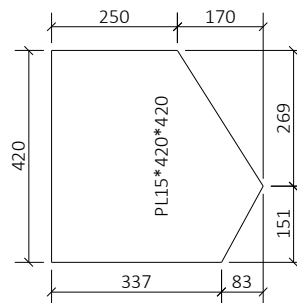


No. 4, Marked GusPL/4

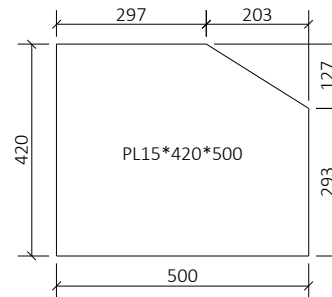

No. 8, Marked GusPL/6

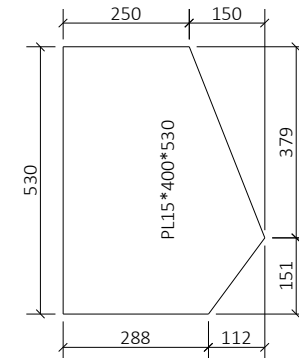


No. 4, Marked GusPL/9

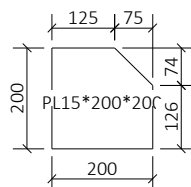


No. 4, Marked GusPL/8


TITLE		گاست	
CLIENT			
CONTRACTOR		ISSUED	
MODELLED BY	EN ALMASI	SCALE	1:15
DRAWING No	[25]	REVISION No.	0
A4			

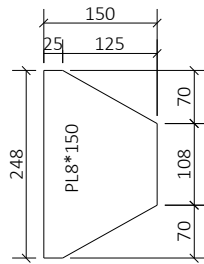


No. 14, Marked WePL/1

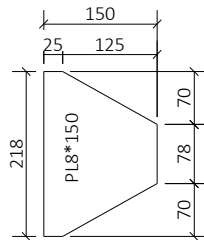


No. 12, Marked WePL/2

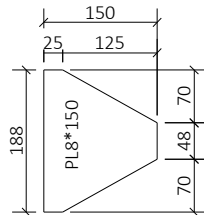


No. 24, Marked WePL/3

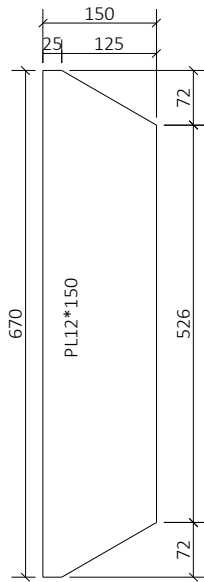


No. 12, Marked WePL/4

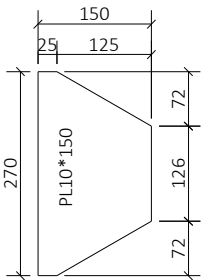


No. 6, Marked WePL/6

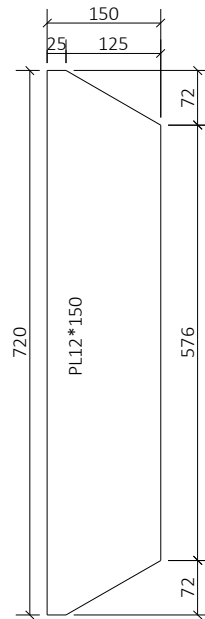

No. 2, Marked WePL/5

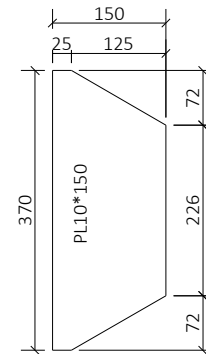

No. 8, Marked WePL/7

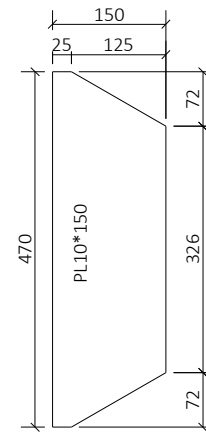

No. 6, Marked WePL/8

TITLE		ورق جان		
CLIENT				
CONTRACTOR		ISSUED		
MODELLED BY	EN ALMASI	SCALE 1:10		A4
DRAWING No	[26]	REVISION No. 0		